

R401.3 Drainage.
Surface drainage shall be diverted to a storm sewer conveyance or other approved point of collection that does not create a hazard. Lots shall be graded to drain surface water away from foundation walls. The grade shall fall not fewer than 6 inches (152 mm) within the first 10 feet (3048 mm).

Exception: Where lot lines, walls, slopes or other physical barriers prohibit 6 inches (152 mm) of fall within 10 feet (3048 mm), drains or swales shall be constructed to ensure drainage away from the structure. Impervious surfaces within 10 feet (3048 mm) of the building foundation shall be sloped not less than 2 percent away from the building.

JOY AVE. (PUBLIC)

PROPERTY LINE

N 0° 35' 37" E
93.43'

10'-0"

32'-0.78"

20'-0"

DRIVEWAY

NEW HOUSE

ROOF LINE

PROPERTY LINE

27'-11.34"

PROPERTY LINE

S 89° 24' 23" E
165.00'

10'-0"

20'-0"

N 79° 15' 35" W
109.89'

PROPERTY LINE

28'-42"

N 79° 18' 39" W
28.42'

PROPERTY LINE

S 0° 35' 37" W
150.33'

WATKINS STREET (PUBLIC)

1 SITE PLAN
3/32" = 1'-0"

↑



NOTE: RISEN HOME DESIGN PLANS DO NOT CARRY AN ENGINEER'S AND/OR ARCHITECT'S STAMP(S) SOME CONDITIONS MAY ARISE DURING DESIGN. AND/OR CONSTRUCTION THAT MAY REQUIRE AN ARCHITECT'S AND/OR ENGINEER'S STAMP TO COMPLY WITH LOCAL BUILDING CODES. THE CONTRACTOR IS TO VERIFY THESE CONDITIONS AND SECURE REQUIRED STAMPS PRIOR TO CONSTRUCTION

GENERAL CONDITIONS	
<u>DRAWINGS & SPECIFICATIONS</u> IT IS THE INTENT OF THE DRAWINGS AND SPECIFICATIONS TO BE GUIDELINES FOR CONSTRUCTION. THE CONTRACTOR IS RESPONSIBLE FOR DETERMINING ANY QUESTIONS AND MEANINGS IN THE WORKING DRAWINGS AND SPECIFICATIONS AND THE CONTRACTOR SHALL NOTIFY THE DESIGNER IN WRITING OF ANY ERRORS, OMISSIONS, OR UNSUITABLE DETAILING WHICH MAY CAUSE CONSTRUCTION PROBLEMS. THE DESIGNER'S LIABILITY REGARDING ERRORS AND/OR OMISSIONS WILL BE LIMITED TO THE CORRECTION OF THE ORIGINAL DRAWINGS. CONSULTANT'S LIABILITY IS THE SAME.	



**BROWNSTONE
15/2 RIVER WALK CROSSING SUB.
MIDDLETON, ID
SITE PLAN**


These Drawings contain confidential proprietary information and are the property of Risen Home Design. These drawings are NOT to be reproduced, copied whole or in part, disclosed, used for construction or any other purpose without prior written permission from Risen Home Design.

REVISIONS

[illegible]

SHEET TITLE
SITE PLAN

RHD PROJECT NUMBER:		RHD-1323	
DRAWN BY: MM		DATE: 4/14/2025	
CHECKED BY: -		DATE: 4/14/2025	
DRAWING NUMBER:			REV:
A1.0			1

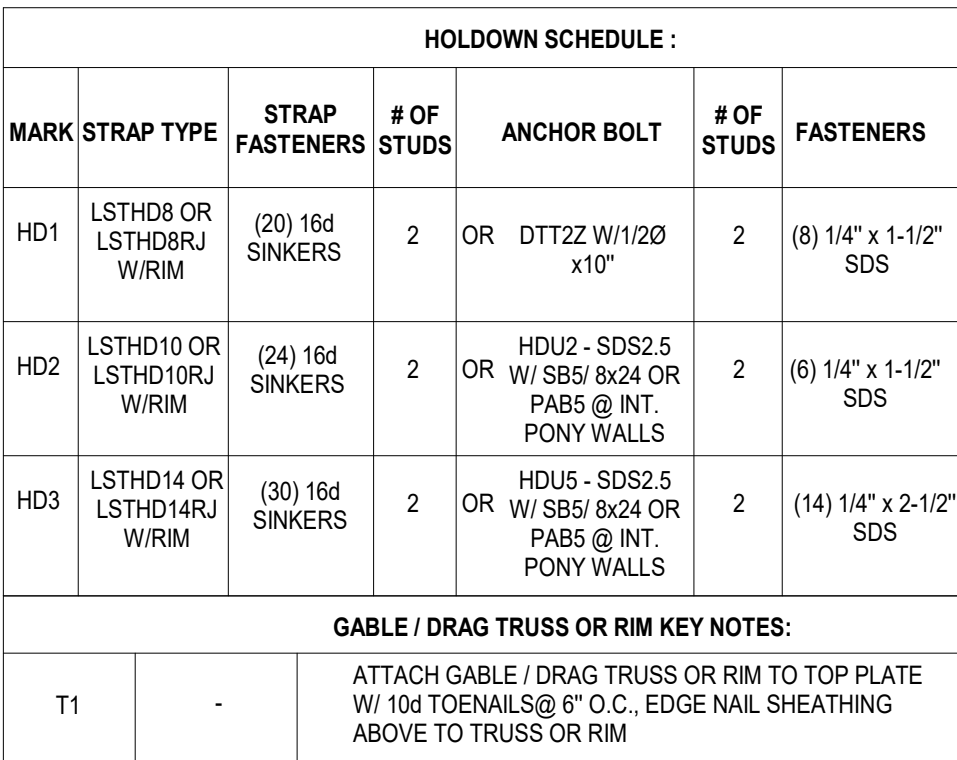


1 FOUNDATION PLAN
1/4" = 1'-0"

NOTE: RISEN HOME DESIGN PLANS DO NOT CARRY AN ENGINEER'S AND/OR ARCHITECT'S STAMP(S) SOME CONDITIONS MAY ARISE DURING DESIGN, AND/OR CONSTRUCTION THAT MAY REQUIRE AN ARCHITECT'S AND/OR ENGINEER'S STAMP TO COMPLY WITH LOCAL BUILDING CODES. THE CONTRACTOR IS TO VERIFY THESE CONDITIONS AND SECURE REQUIRED STAMPS PRIOR TO CONSTRUCTION

1. ASSUMED SOIL BEARING PRESSURE OF 1500 P.S.F.
2. ALL CONC. TO BEAR ON FIRM, NATURAL, UNDISTURBED SOIL.
3. CONCRETE COMPRESSIVE STRENGTH AT 28 DAYS TO BE:
WALLS NOT EXPOSED TO WEATHER 3500 PSI
WALLS EXPOSED TO WEATHER 4000 PSI
PORCHES, STEPS & GARAGE SLAB 3500PSI
4. EXTEND FOOTING BELOW FROST LINE, (24" MIN. INTO NATURAL SOIL FOR 1 STORY AND 2 STORY CONSTRUCTION
5. THE GRADE ABOVE FROM THE FOUNDATION WALLS FOR ALL A MIN. 6" WITHIN THE FIRST FEET.
6. 1/2" DIA. X 1" ANCHOR BOLTS TO BE USED @ 6'-0" O.C. & 7" MIN. INTO CONC. & 1/2" MAX FROM ANY CORNER W/ 2" DIA. WASHERS & 1/2" DIA. NUTS (CONC. STEM WALLS)
7. 18" MIN. GRAVEL SPREAD 12" MIN. AROUND 6" MIN. BULK VAPOR BARRIER THROUGHOUT LAP JOINTS 12" MIN. EXTEND UP STEM WALL & STAPLE TO MUD SILL.
8. SUGGESTED REBAR PLACEMENT TO BE: 2-#4 HORIZONTAL REBAR IN FOOTING AND VERTICAL REBAR @ 6'-0" O.C. IN ALL 2' EXTERIOR CONCRETE STEM WALLS, ACTUAL REBAR INSTALLATION TO FOLLOW LOCAL REQUIREMENTS.
9. SUGGESTED REBAR PLACEMENT TO BE: 2-#4 HORIZONTAL REBAR IN FOOTING AND 2-#4 HORIZONTAL REBAR IN STEM WALL EQUALLY SPACED AND VERTICAL REBAR @ 6'-0" O.C. IN ALL 2' EXTERIOR CONCRETE STEM WALLS, ACTUAL REBAR INSTALLATION TO FOLLOW LOCAL REQUIREMENTS.
10. BASEMENT CONCRETE WALLS TO FOLLOW LOCAL REQUIREMENTS AND OR PER APPROVED STRUCTURAL ENGINEERING DRAWINGS.
11. ALL CONCRETE PORCHES TO BE DOWELED TO EXTERIOR STEM WALL WITH #4 REBAR @ 2'-0" O.C.
12. CONTRACTOR TO VERIFY ALL MEASUREMENTS AND SQUARENESS OF CORNERS PRIOR TO POURING AND AFTER COMPLETION OF FINAL WORK. ALL FINISHED WORK (TOP OF STEM WALLS, TOP OF FOOTINGS, SLABS, PORCHES) TO BE FINISHED AS LEVEL AS POSSIBLE.
13. ADD SIMPSON HANCHADZ THE DOWN STRAP TO ALL GARAGE WING WALLS AND FOUNDATION WALL LESS THAN 2' LONG, IF REQUIRED PER LOCAL BUILDING DEPARTMENT.

- 1 METAL WALL HOLDUPN STRAP (SIMPSON STDH14)
W/ ONE 4" REBAR IN SHEAR CONE OF STEM WALL.
SEE BRACING NOTES ON FLOOR PLAN.
SEE FLOOR PLAN TO COORDINATE EXACT
LOCATION ON WINDOWS AND DOORS.
- 2 CONTINUOUS FOUNDATION WALL BLOCK OUT AS
REQUIRED.
- 3 CRAWL SPACE ACCESS.
- 4 4" CONCRETE SLAB ON 4" COMPACT GRAVEL BASE
W/ 6" THICKENED SLAB EDGE TO FROSTLINE
W/ 4" x 18" BAR @ 24" O.C.
- 5 ALL FOUNDATIONS, FOOTINGS, AND BALCONY/ROOF
SUPPORT PIERS TO MAINTAIN A MINIMUM DEPTH OF 24"
BELOW FINISH GRADE ELEVATION FOR FROST
PROTECTION.
- 6 CONC. STOOP.
- 7 SIMPSON POST BASE OR EQUAL.
- 8 24"x24" MIN. DEEP CONC. SUPPORT PIER@CONC. SLAB.
- 9 BLOCK OUT PONY WALL FOR 18"x24" CRAWL ACCESS

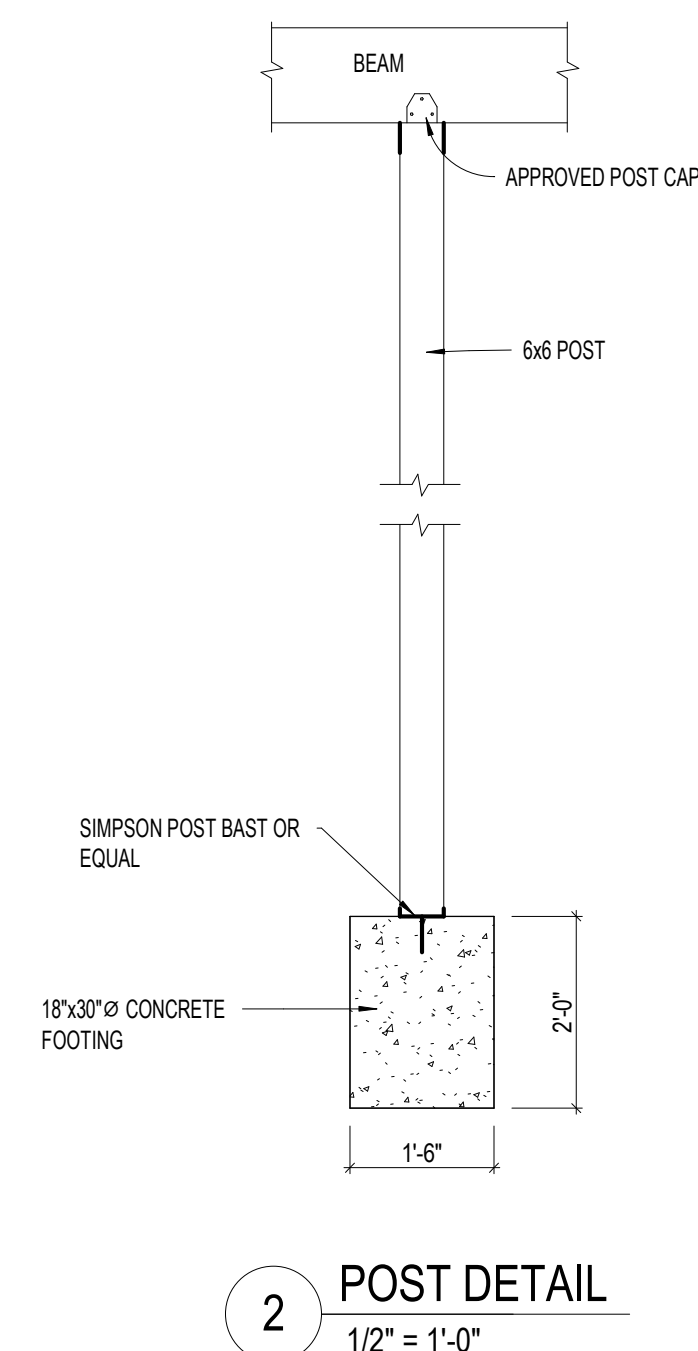

2 POST DETAIL
1/2" = 1'-0"

GENERAL CONDITIONS

DRAWINGS & SPECIFICATIONS

IT IS THE INTENT OF THE DRAWINGS AND SPECIFICATIONS TO BE GUIDELINES FOR CONSTRUCTION. THE CONTRACTOR IS RESPONSIBLE FOR DETERMINING ANY QUESTIONS AND MEANINGS IN THE WORKING DRAWINGS AND SPECIFICATIONS AND THE CONTRACTOR SHALL NOTIFY THE DESIGNER IN WRITING OF ANY ERRORS, OMISSIONS, OR UNSUITABLE DETAILING WHICH MAY CAUSE CONSTRUCTION PROBLEMS. THE DESIGNER'S LIABILITY REGARDING ERRORS AND/OR OMISSIONS WILL BE LIMITED TO THE CORRECTION OF THE ORIGINAL DRAWINGS. CONSULTANT'S LIABILITY IS THE SAME.




These Drawings contain confidential proprietary information and are the property of Risen Home Design. These drawings are NOT to be reproduced, copied whole or in part, disclosed, used for construction or any other purpose without prior written permission from Risen Home Design.

**BROWNSTONE
15/2 RIVER WALK CROSSING SUB.
MIDDLETON, ID
FOUNDATION PLAN**

[illegible]

FOUNDATION PLAN

RHD PROJECT NUMBER:		RHD-1323	
DRAWN BY: MM		DATE: 5/4/2025	
CHECKED BY: -		DATE: 5/4/2025	
DRAWING NUMBER:			REV:
A2.0			0

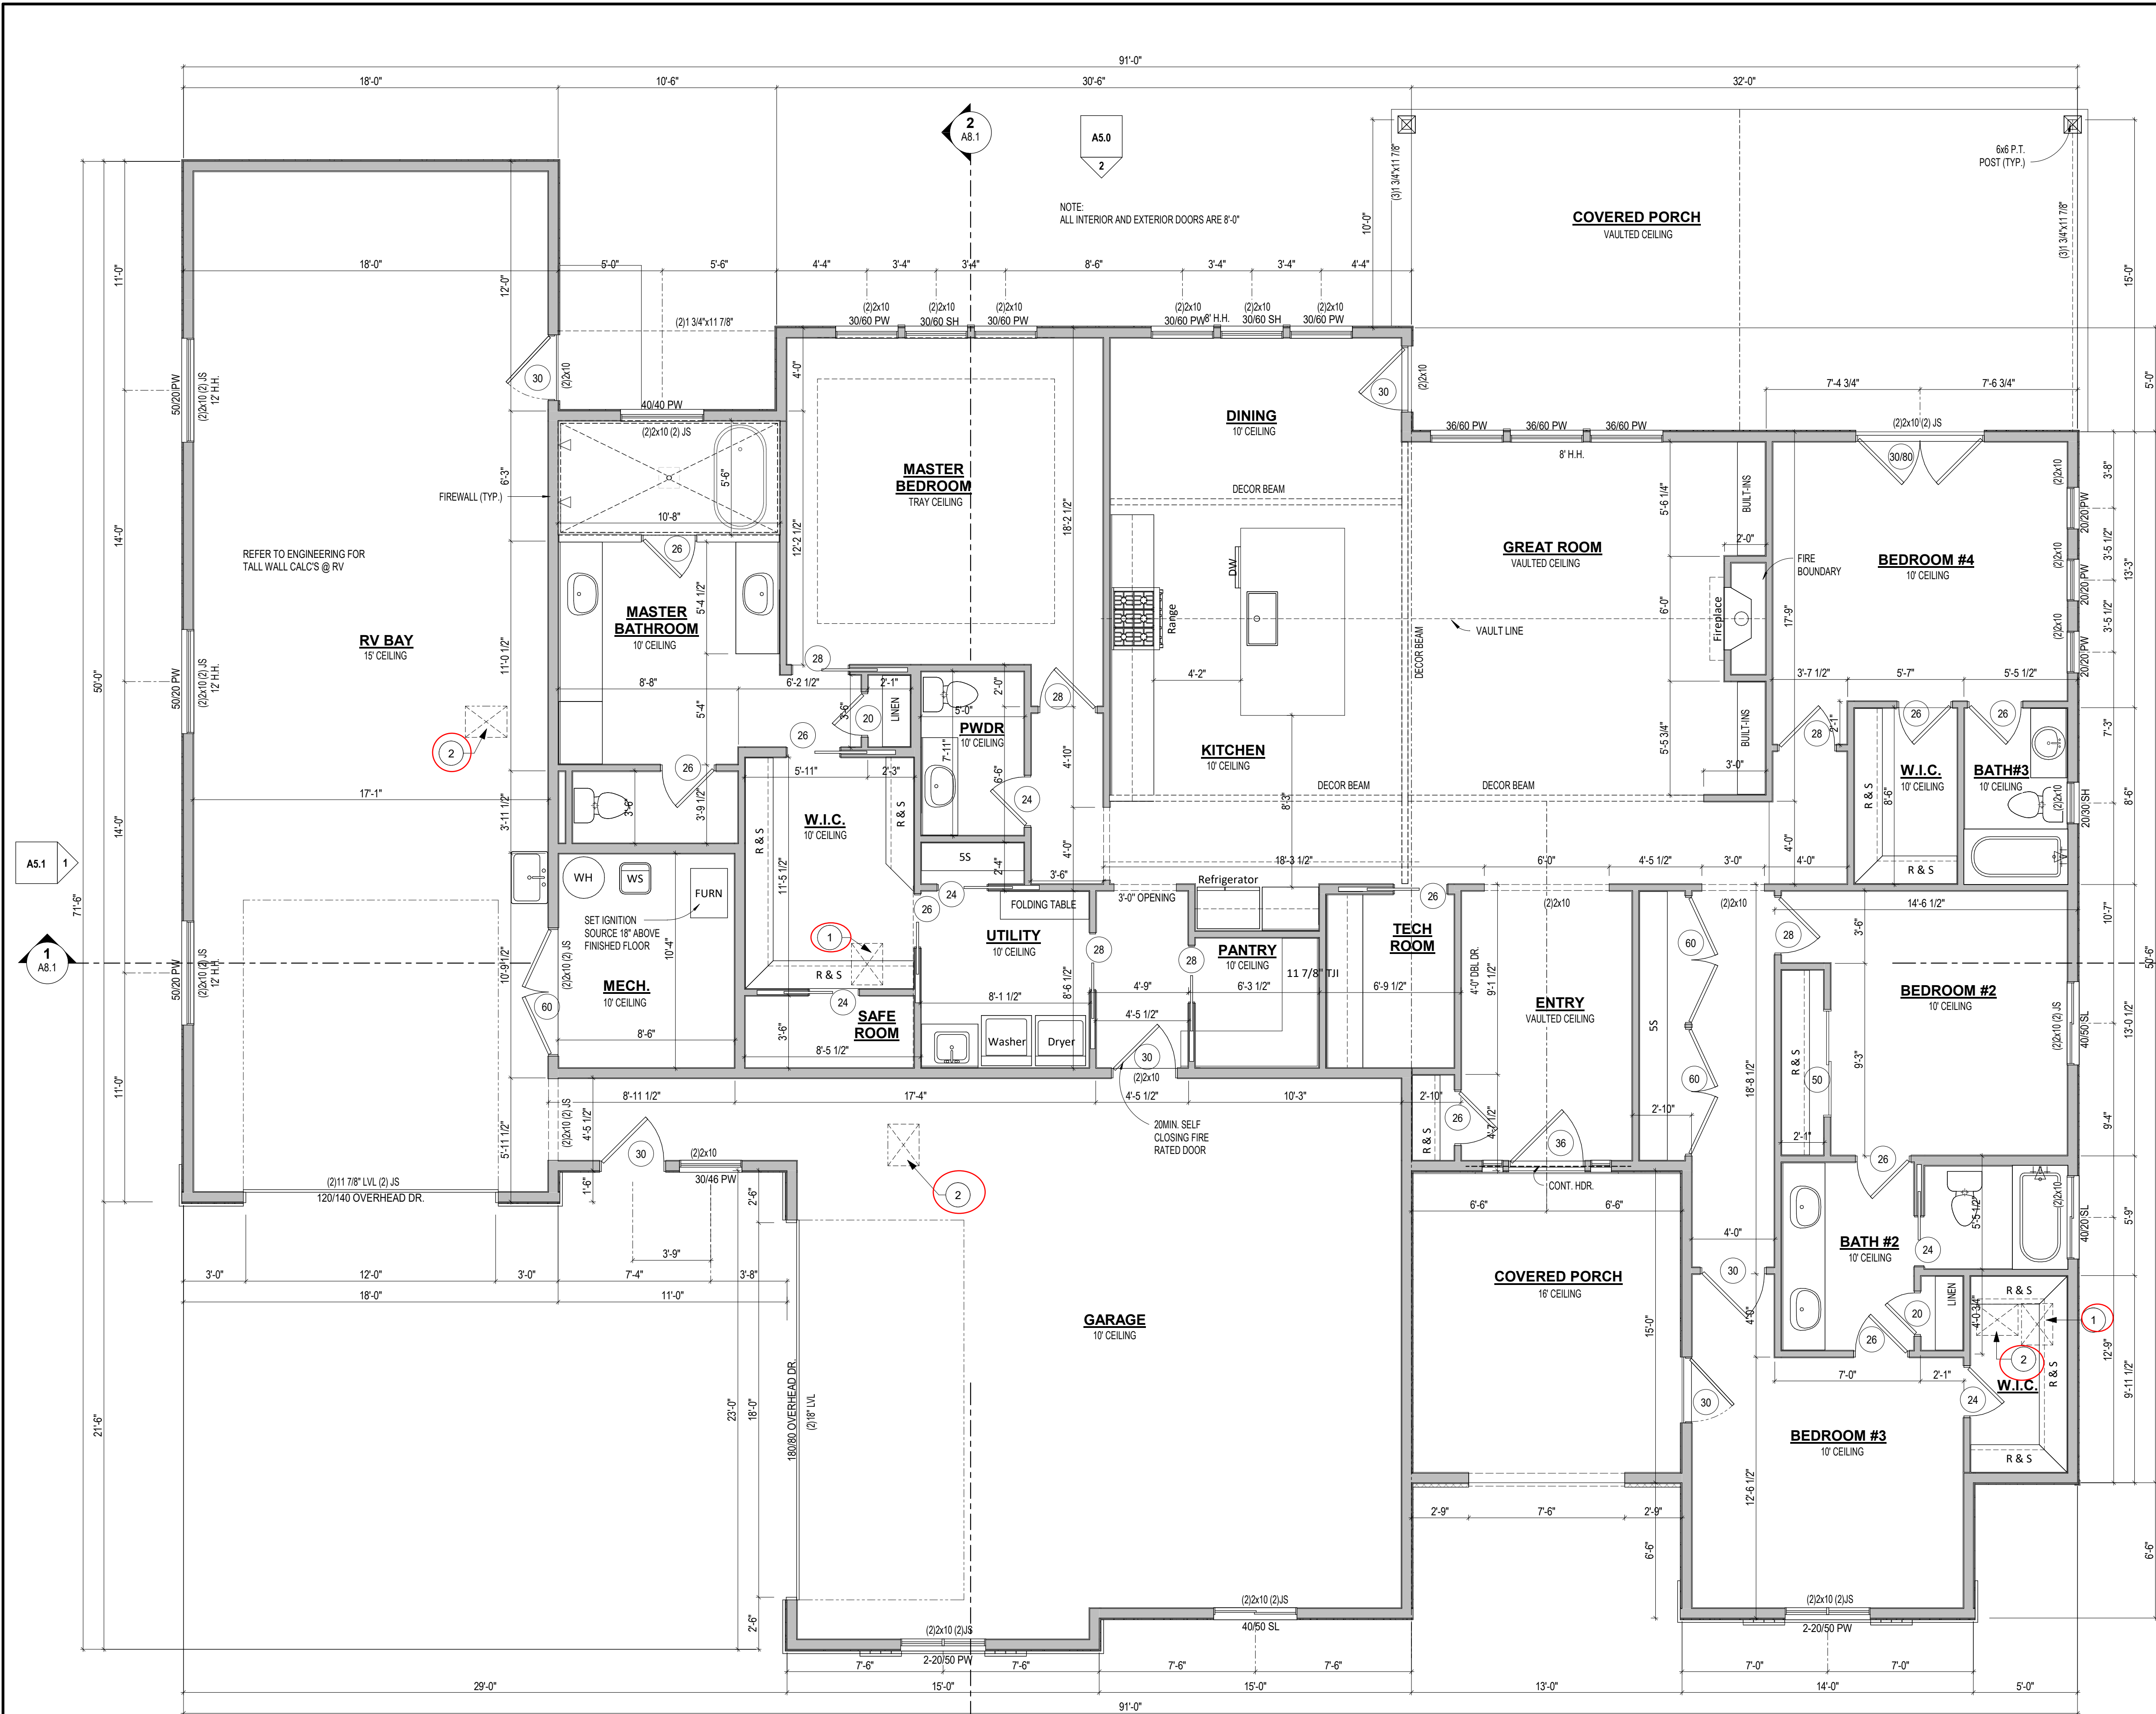

FLOOR PLAN NOTES

1. ALL STRUCTURAL LUMBER SIZED FOR #2 OR BETTER DOUG FIR LARCH.
2. 2x EXTERIOR STUD FRAMING @ 16" O.C. W/ SINGLE BOTTOM PLATE AND DOUBLE TOP PLATE.
3. 4x8 HEADERS IN ALL BEARING WALL OPENING UNLESS OTHERWISE NOTED.
4. ALLOW FOR A 22" x 30" (MIN) ATTIC AND CRAWL SPACE ACCESS.
5. ALL METAL CONNECTIONS TO BE SIMPSON CO. OR BETTER.
6. 5/8" TYPE 'X' GYP BOARD @ ALL GARAGE COMMON WALLS AND CEILINGS APPLIED TO GARAGE SIDE AND ALL WALLS, BEAMS, POSTS AND OTHER STRUCTURAL MEMBERS SUPPORTING FIRE PROTECTED HORIZONTAL STRUCTURAL MEMBERS.
7. DOORS BETWEEN GARAGE AND DWELLING ARE TO BE SELF CLOSING AND TIGHT FITTING SOLID WOOD DOOR 1 3/8" THICK OR A DOOR W/ A FIRE PROTECTION RATING OF NOT LESS THAN 20 MINUTES.
8. 1/2" GYPSUM BOARD TO BE INSTALLED ON INSIDE WALLS OF HOUSE.
9. ALL WINDOWS TO HAVE BREATHER TUBES INSTALLED.
10. ROOF SYSTEM TO BE PRE-ENGINEERED MANUFACTURED ROOF TRUSSES UNLESS OTHERWISE NOTED.
11. ALL CONSTRUCTION PRACTICES USED IN THE CONSTRUCTION OF THIS DWELLING SHALL BE DONE IN ACCORDANCE W/ THE 2018 WHERE APPLICABLE.
12. VENT RANGE HOOD, FANS, AND DRYER TO OUTSIDE AIR. CONTRACTOR TO VERIFY ALL CONDITIONS AND DIMENSIONS PRIOR TO COMMENCING WORK.
13. ALL RESCUE WINDOWS FROM SLEEPING AREAS MUST MEET THE FOLLING REQUIREMENTS:
 1. SHALL HAVE A NET CLEAR OPENING OF 5.1 SQ. FT.
 2. MINIMUM HEIGHT OF 24".
 3. MINIMUM WIDTH OF 20".
 4. FINISHED SILL HEIGHT OF NOT MORE THAN 4".
14. EXTERIOR DIMENSIONS ARE TO FACE OF STUD WALL. INTERIOR DIMENSIONS ARE TO FACE OF STUD WALL.
15. ALL FURNACE SWITCHES, PILOTS, AND BURNERS TO BE MINIMUM 18" ABOVE FINISHED FLOOR.

SHEET NOTES

- 1 CRAWL SPACE ACCESS. COORDINATE WITH JOIST LAYOUT.
- 2 ATTIC SPACE ACCESS. COORDINATE WITH TRUSS LAYOUT.

DOOR/WINDOW TAG EXAMPLE

DOOR TAG	WINDOW TAG
26	40/56 SH = 4'-0" x 5'-6" SINGLE HUNG

SQ/FT.

LIVING AREA	2868 SF
GARAGE	948 SF
RV BAY	883 SF
FRONT PORCH	195 SF
BACK PATIO	514 SF

NOTE: VERIFY ALL WINDOW/DOOR ROUGH OPENING AND HEADER HEIGHT AND THE SAME FOR TRIM PACKAGE. VERIFY STANDARD HEIGHTS WITH CONTRACTOR BEFORE FRAMING.

SEE 2018 IRC

- R302.7 PROVIDE UNDERSTAIR PROTECTION AS REQUIRED
R302.11 PROVIDE FIREBLOCKING AS REQUIRED
R303.7 PROVIDE SWITCHING AND ILLUMINATION AS REQUIRED
R305 PROVIDE SUFFICIENT CEILING HEIGHTS
R311.7 MEET STAIRWAY REQUIREMENTS
R312 MEET GUARD REQUIREMENTS

1 1st FLOOR PLAN
1/4" = 1'-0"

TABLE R402.1.1 INSULATION AND FENESTRATION REQUIREMENTS BY COMPONENT									
CLIMATE ZONE	FENESTRATION U-FACTOR	SKYLIGHT U-FACTOR	GLAZED FENESTRATION SHGC	CEILING R-VALUE	WOOD FRAM WALL R-VALUE	MASS WALL R-VALUE	FLOOR R-VALUE	BASEMENT WALL R-VALUE	SLAB R-VALUE
5 AND MARINE 4	0.35 0.32	0.55	NR	49	20 OR 13+5 ^h	13/17	30 ^g	15/19	10, 2 ft

NOTE: RISEN HOME DESIGN PLANS DO NOT CARRY AN ENGINEER'S AND/OR ARCHITECT'S STAMP(S) SOME CONDITIONS MAY ARISE DURING DESIGN, AND/OR CONSTRUCTION THAT MAY REQUIRE AN ARCHITECT'S AND/OR ENGINEER'S STAMP TO COMPLY WITH LOCAL BUILDING CODES. THE CONTRACTOR IS TO VERIFY THESE CONDITIONS AND SECURE REQUIRED STAMPS PRIOR TO CONSTRUCTION

DRAWINGS & SPECIFICATIONS
IT IS THE INTENT OF THE DRAWINGS AND SPECIFICATIONS TO BE GUIDELINES FOR CONSTRUCTION. THE CONTRACTOR IS RESPONSIBLE FOR DETERMINING ANY QUESTIONS AND MEANINGS IN THE WORKING DRAWINGS AND SPECIFICATIONS AND THE CONTRACTOR SHALL NOTIFY THE DESIGNER IN WRITING OF ANY ERRORS, OMISSIONS, OR UNSUITABLE DETAILING WHICH MAY CAUSE CONSTRUCTION PROBLEMS. THE DESIGNER'S LIABILITY REGARDING ERRORS AND/OR OMISSIONS WILL BE LIMITED TO THE CORRECTION OF THE ORIGINAL DRAWINGS. CONSULTANT'S LIABILITY IS THE SAME.

GENERAL CONDITIONS



BROWNSTONE
15/2 RIVER WALK CROSSING SUB.
MIDDLETON, ID
1st FLOOR PLAN

These Drawings contain confidential proprietary information and are the property of Risen Home Design. These drawings are NOT to be reproduced, copied whole or in part, disclosed, used for construction or any other purpose without prior written permission from Risen Home Design.

REVISIONS	
NO.	DESCRIPTION
1	ISSUE FOR A PRELIMINARY REVIEW
2	ISSUE FOR A PRELIMINARY REVIEW
3	ISSUE FOR CONSTRUCTION

SHEET TITLE	
1st FLOOR PLAN	
RHD PROJECT NUMBER: RHD-1323	
DRAWN BY: MM	DATE: 4/11/2025
CHECKED BY: -	DATE: 4/11/2025
DRAWING NUMBER: A3.0	REV: 0




GENERAL CONDITIONS

DRAWINGS & SPECIFICATIONS



IT IS THE INTENT OF THE DRAWINGS AND SPECIFICATIONS TO BE GUIDELINES FOR CONSTRUCTION. THE CONTRACTOR IS RESPONSIBLE FOR DETERMINING ANY QUESTIONS AND MEANINGS IN THE WORKING DRAWINGS AND SPECIFICATIONS AND THE CONTRACTOR SHALL NOTIFY THE DESIGNER IN WRITING OF ANY ERRORS, OMISSIONS, OR UNSAIFIABLE DETAILING WHICH MAY CAUSE CONSTRUCTION PROBLEMS. THE DESIGNER'S LIABILITY REGARDING ERRORS AND/OR OMISSIONS WILL BE LIMITED TO THE CORRECTION OF THE ORIGINAL DRAWINGS. CONSULTANT'S LIABILITY IS THE SAME.

SHEET TITLE	
WALL BRACING	
RHD PROJECT NUMBER:	RHD-1323
DRAWN BY: MM	DATE: 5/4/2025
CHECKED BY: -	DATE: 5/4/2025
DRAWING NUMBER:	REV:
A4.0	0


Figure 1. Construction Details for APA Portal-Frame Design with Hold Downs

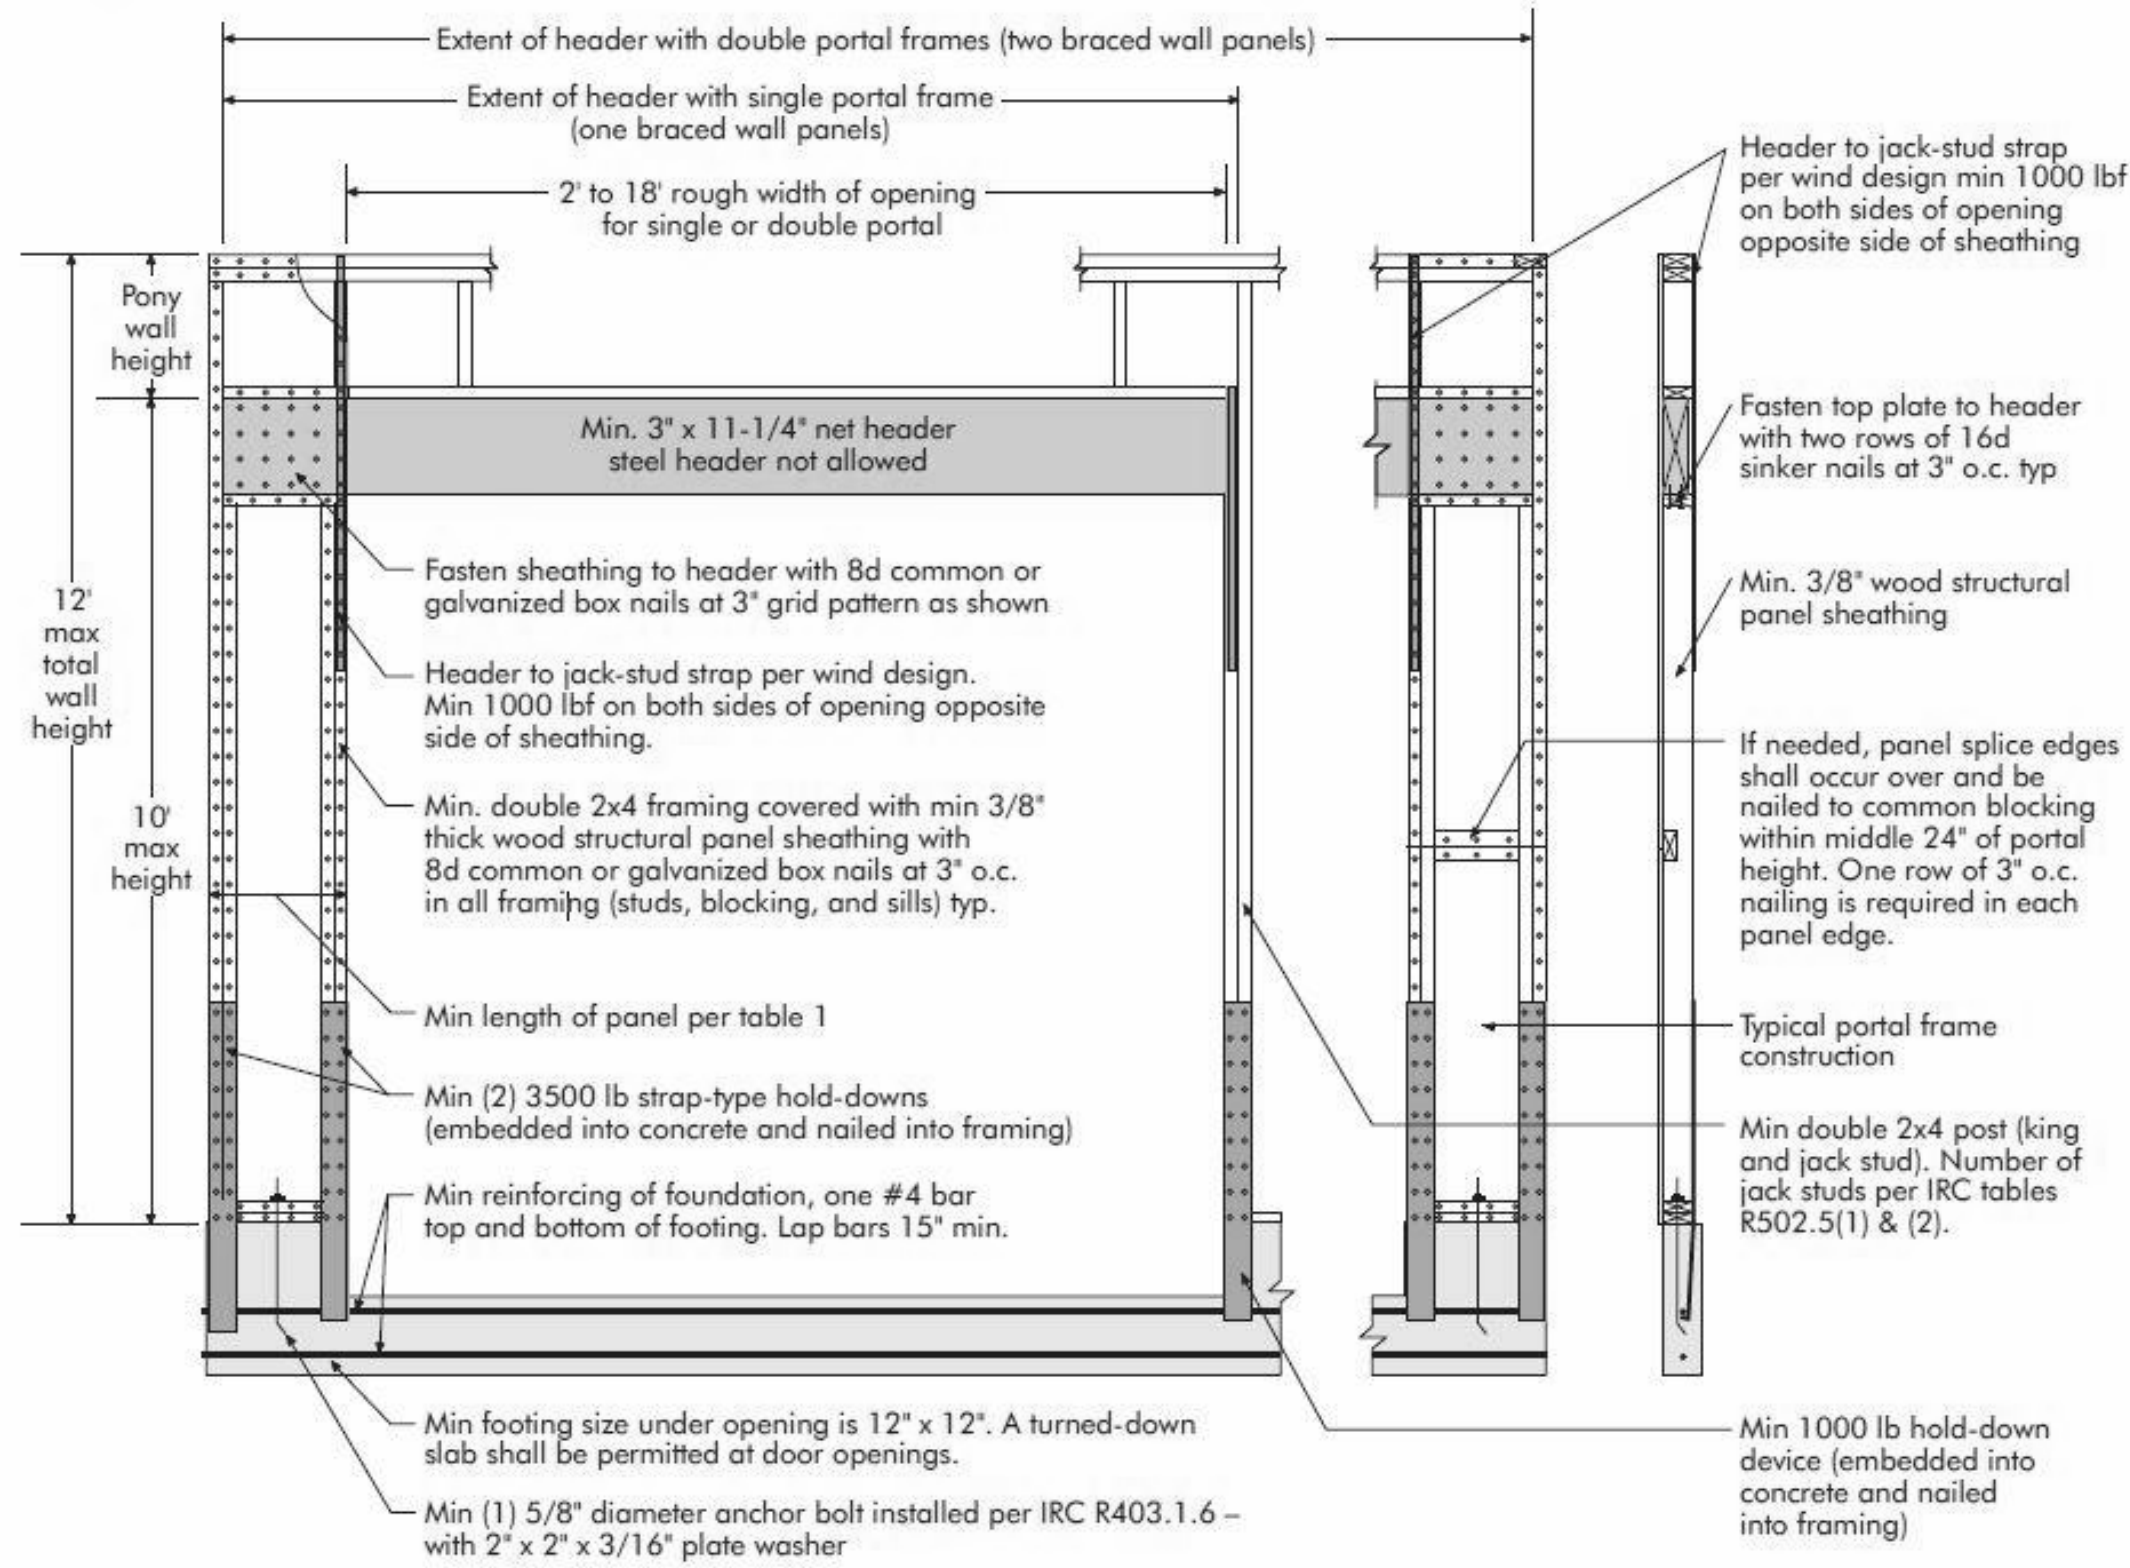


1 APA PORTAL-FRAME DETAIL
1/4" = 1'-0"

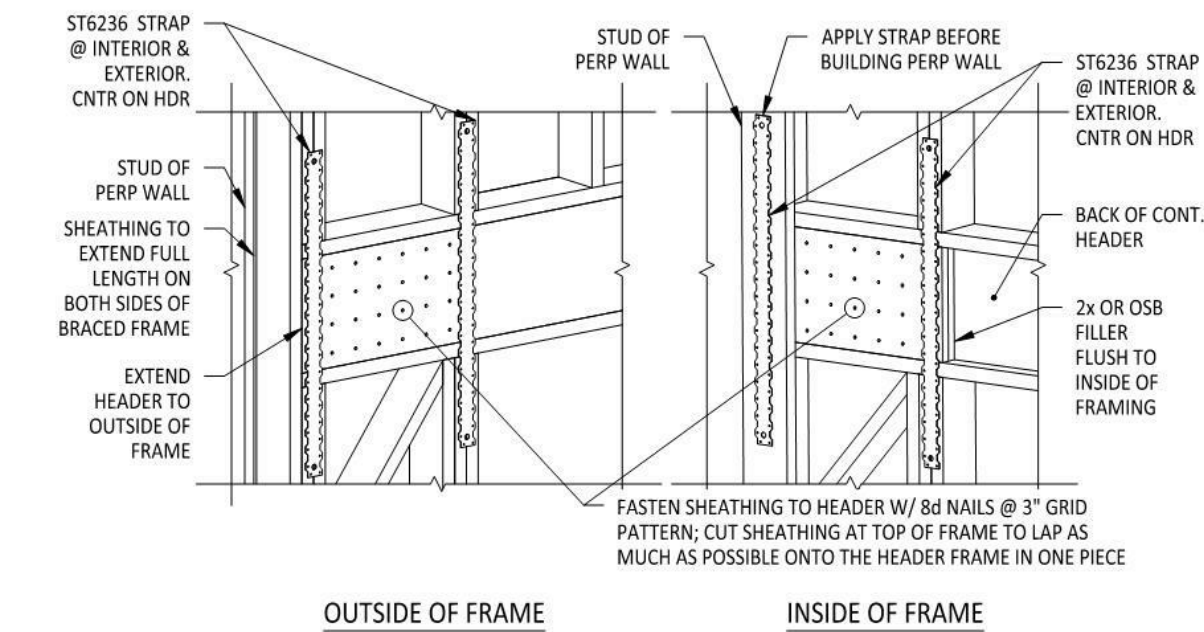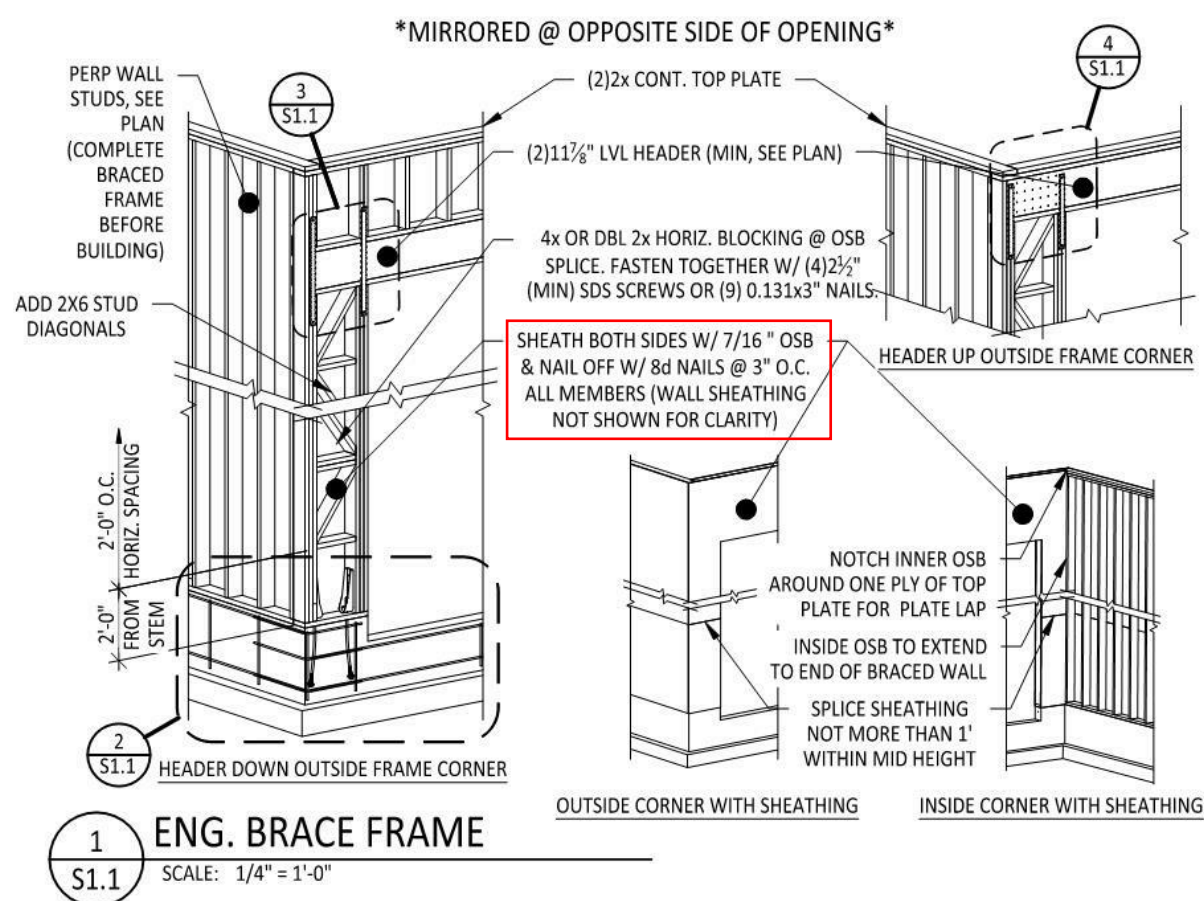


3 S1.1 ENG. BRACE FRAME
SCALE: 3/4" = 1'-0"

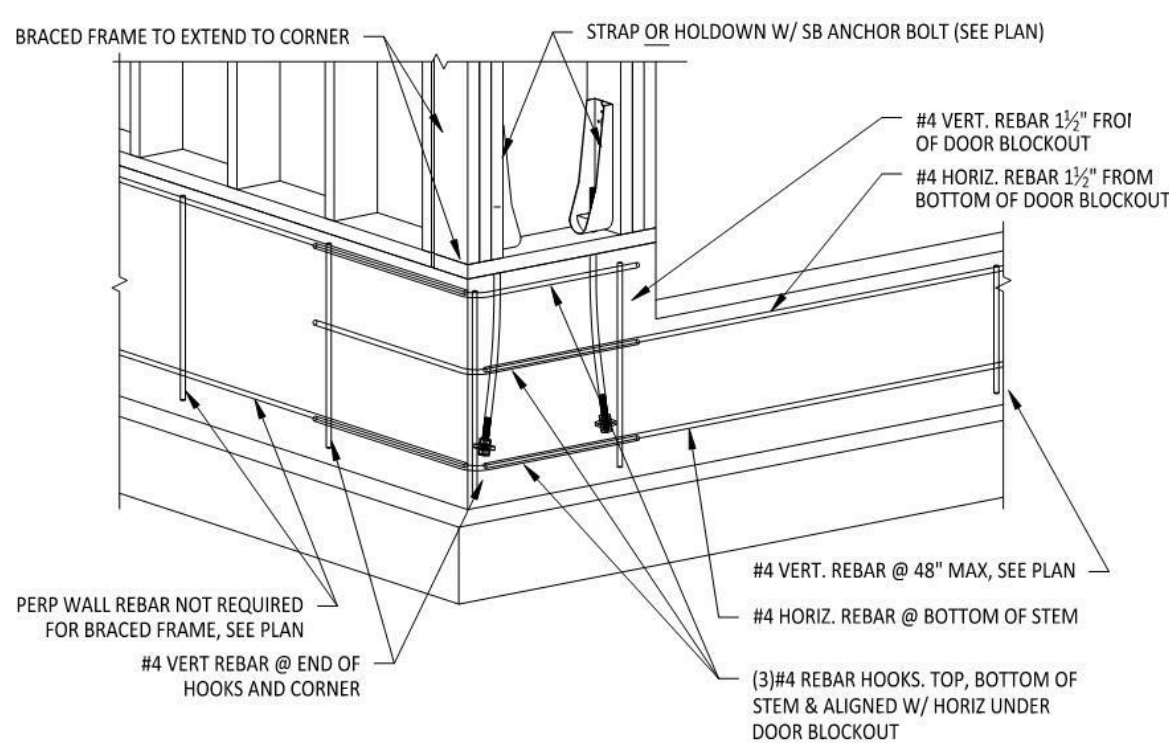


2 S1.1 ENG. BRACE FRAME
SCALE: 3/4" = 1'-0"

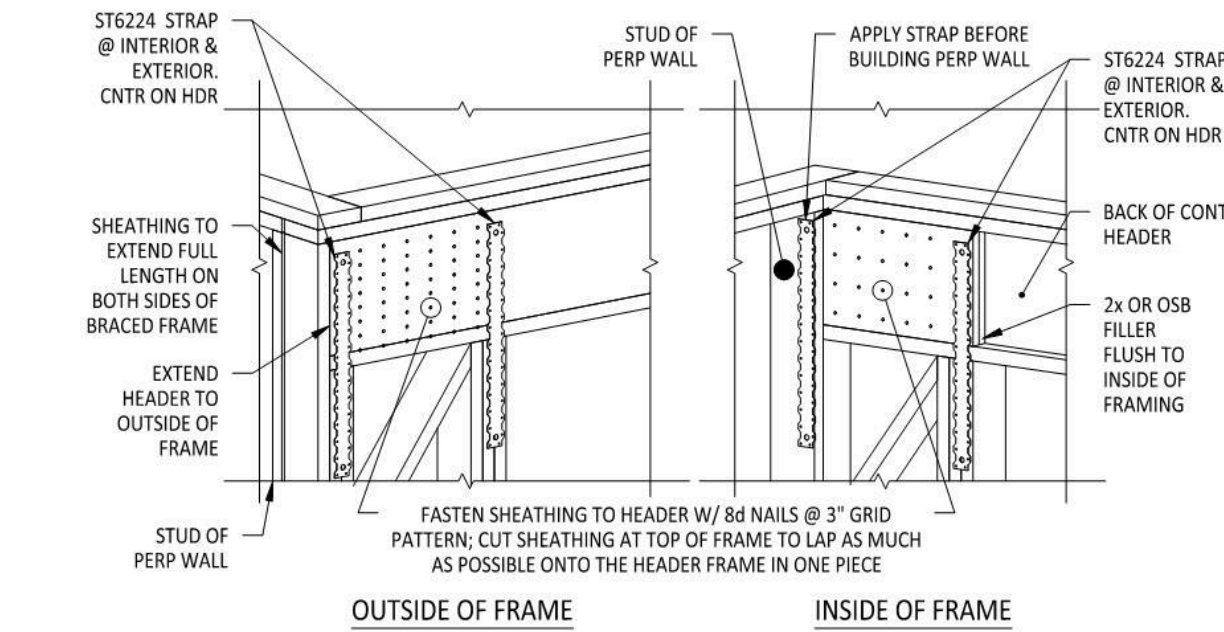


4 S1.1 ENG. BRACE FRAME
SCALE: 3/4" = 1'-0"

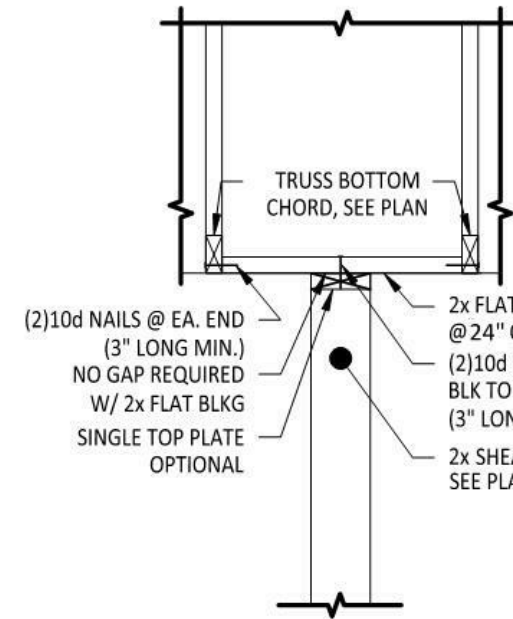

TRUSS TO SHEAR WALL CONNECTION DETAIL
SCALE: 1/4" = 1'-0"

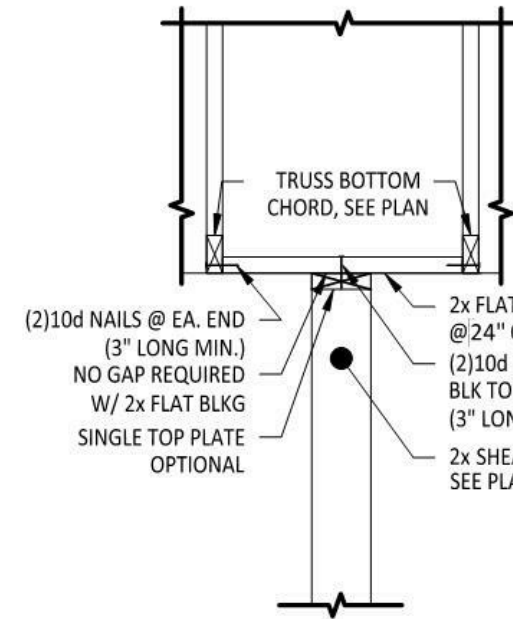

TRUSS TO SHEAR WALL CONNECTION DETAIL
SCALE: 1/4" = 1'-0"

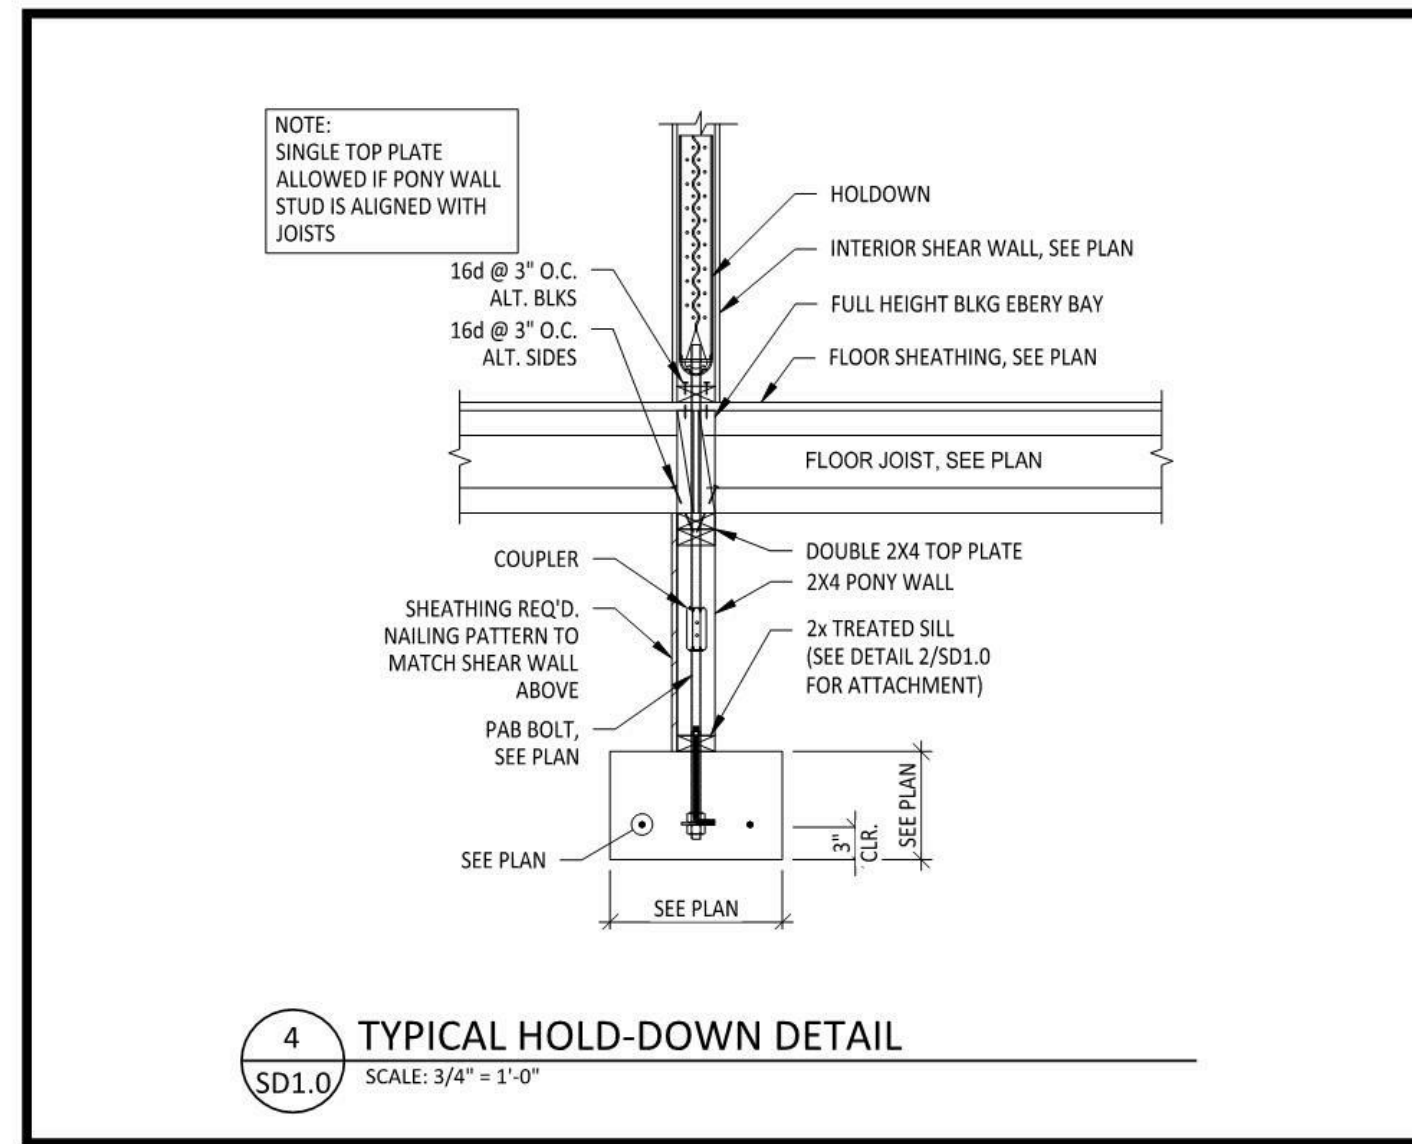

4 SD1.0 TYPICAL HOLD-DOWN DETAIL
SCALE: 3/4" = 1'-0"

NOTE: RISEN HOME DESIGN PLANS DO NOT CARRY AN ENGINEER'S AND/OR ARCHITECT'S STAMP(S). SOME CONDITIONS MAY ARISE DURING DESIGN, AND/OR CONSTRUCTION THAT MAY REQUIRE AN ARCHITECT'S AND/OR ENGINEER'S STAMP TO COMPLY WITH LOCAL BUILDING CODES. THE CONTRACTOR IS TO VERIFY THESE CONDITIONS AND SECURE REQUIRED STAMPS PRIOR TO CONSTRUCTION.

DRAWINGS & SPECIFICATIONS	
IT IS THE INTENT OF THE DRAWINGS AND SPECIFICATIONS TO BE GUIDELINES FOR CONSTRUCTION. THE CONTRACTOR IS RESPONSIBLE FOR DETERMINING ANY QUESTIONS AND MEANINGS IN THE WORKING DRAWINGS AND SPECIFICATIONS AND THE CONTRACTOR SHALL NOTIFY THE DESIGNER IN WRITING OF ANY ERRORS, OMISSIONS, OR UNSUITABLE DETAILING WHICH MAY CAUSE CONSTRUCTION PROBLEMS. THE DESIGNER'S LIABILITY REGARDING ERRORS AND/OR OMISSIONS WILL BE LIMITED TO THE CORRECTION OF THE ORIGINAL DRAWINGS. CONSULTANT'S LIABILITY IS THE SAME.	

GENERAL CONDITIONS	
RHD PROJECT NUMBER: RHD-1323	
DRAWN BY: MM	DATE: 5/4/2025
CHECKED BY: -	DATE: 5/4/2025
DRAWING NUMBER: A4.1	REV: 0




BROWNSTONE
15/2 RIVER WALK CROSSING SUB.
MIDDLETON, ID
BRACING DETAILS

These Drawings contain confidential proprietary information and are the property of Risen Home Design. These drawings are NOT to be reproduced, copied whole or in part, disclosed, used for construction or any other purpose without prior written permission from Risen Home Design.



R806 - PROVIDE ADEQUATE ATTIC VENTILATION.

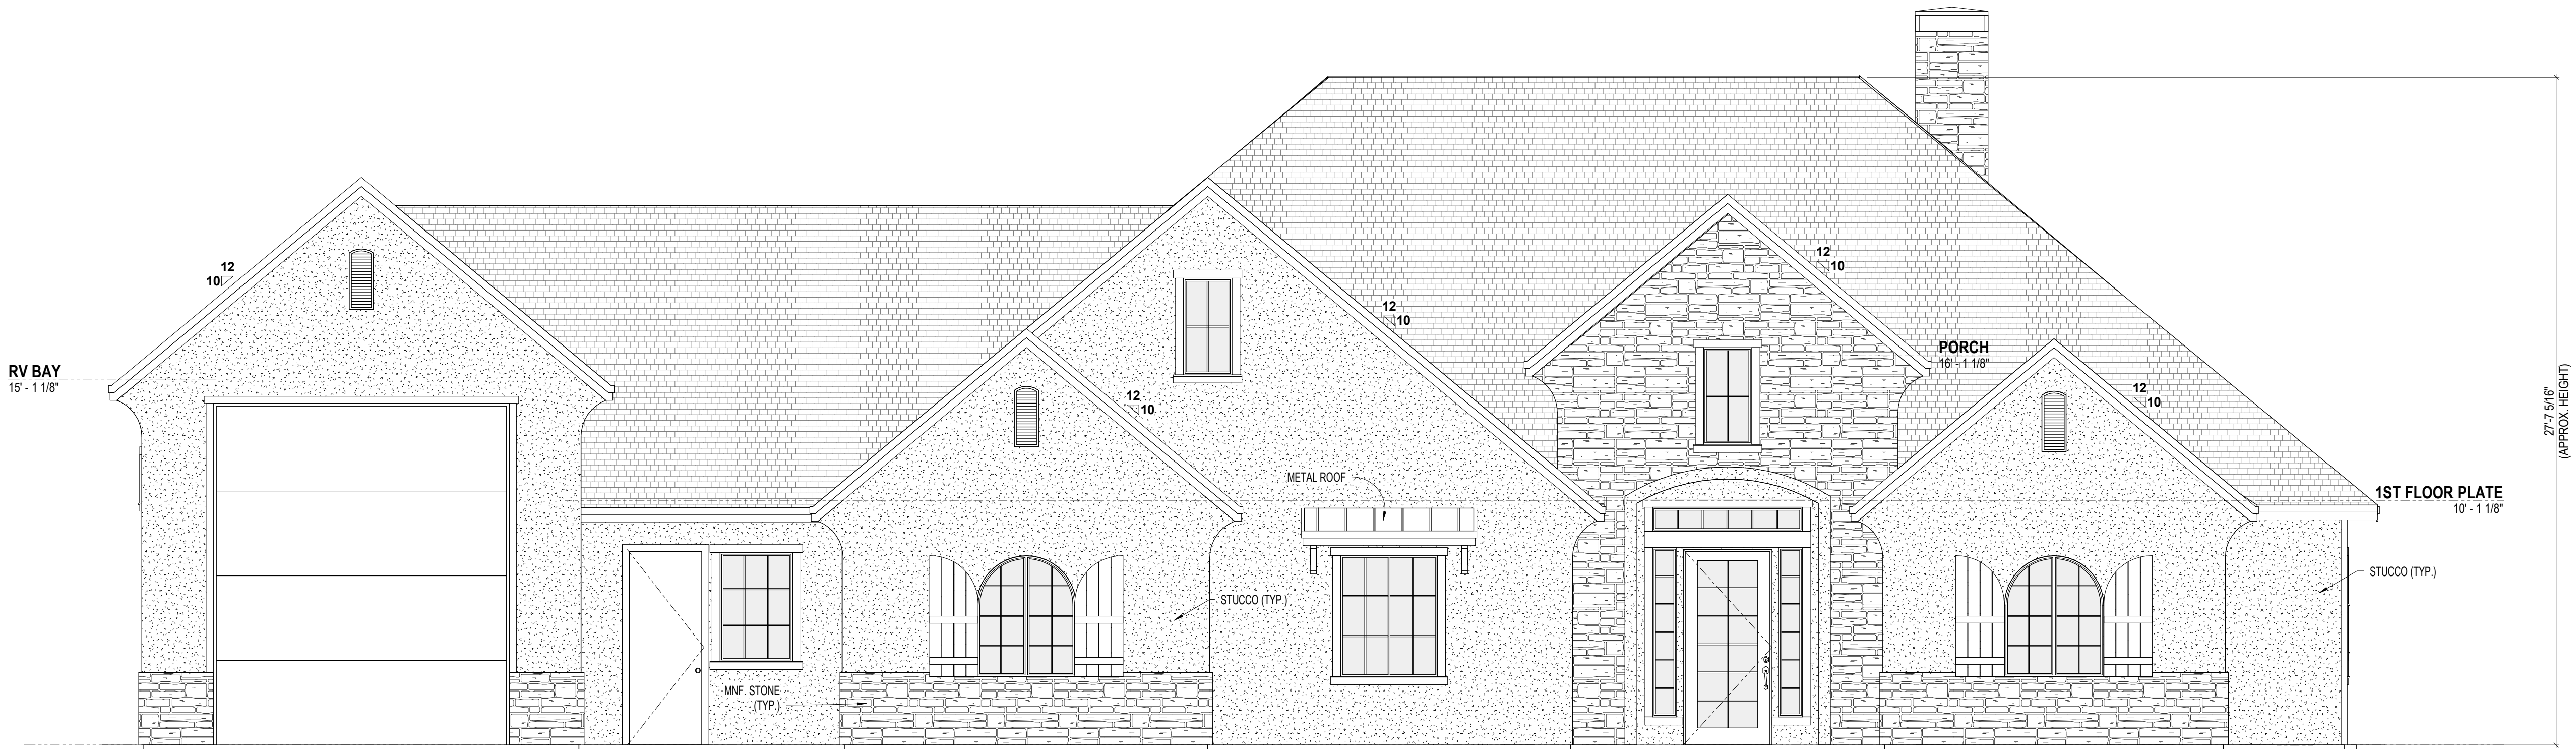


1 FRONT VIEW
1/4" = 1'-0"



2 BACK VIEW
1/4" = 1'-0"

NOTE: RISEN HOME DESIGN PLANS DO NOT CARRY AN ENGINEER'S AND/OR ARCHITECT'S STAMP(S) SOME CONDITIONS MAY ARISE DURING DESIGN, AND/OR CONSTRUCTION THAT MAY REQUIRE AN ARCHITECT'S AND/OR ENGINEER'S STAMP TO COMPLY WITH LOCAL BUILDING CODES. THE CONTRACTOR IS TO VERIFY THESE CONDITIONS AND SECURE REQUIRED STAMPS PRIOR TO CONSTRUCTION

DRAWINGS & SPECIFICATIONS
IT IS THE INTENT OF THE DRAWINGS AND SPECIFICATIONS TO BE GUIDELINES FOR CONSTRUCTION. THE CONTRACTOR IS RESPONSIBLE FOR DETERMINING ANY QUESTIONS AND MEANINGS IN THE WORKING DRAWINGS AND SPECIFICATIONS AND THE CONTRACTOR SHALL NOTIFY THE DESIGNER IN WRITING OF ANY ERRORS, OMISSIONS, OR UNSUITABLE DETAILING WHICH MAY CAUSE CONSTRUCTION PROBLEMS. THE DESIGNER'S LIABILITY REGARDING ERRORS AND/OR OMISSIONS WILL BE LIMITED TO THE CORRECTION OF THE ORIGINAL DRAWINGS. CONSULTANT'S LIABILITY IS THE SAME.

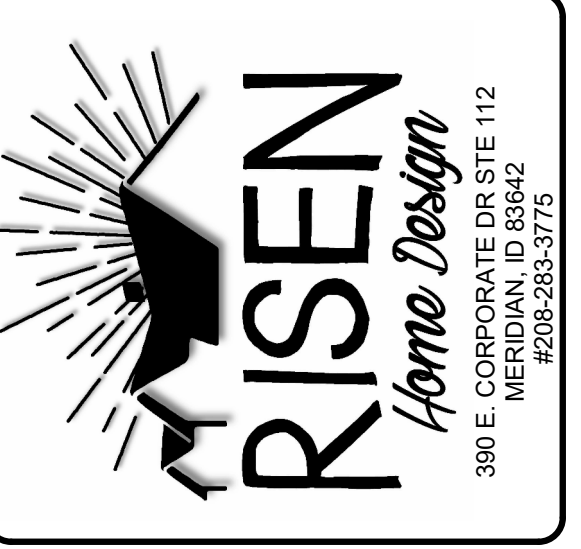

BLACKSTONE
HOMES

These Drawings contain confidential proprietary information and are the property of Risen Home Design. These drawings are NOT to be reproduced, copied whole or in part, disclosed, used for construction or any other purpose without prior written permission from Risen Home Design.

BROWNSTONE

15/2 RIVER WALK CROSSING SUB.

MIDDLETON, ID

ELEVATIONS

REVISIONS	
NO.	DESCRIPTION
1	DATE
2	4/11/2025
3	4/11/2025
SHEET TITLE

ELEVATIONS

RHD PROJECT NUMBER: RHD-1323

DRAWN BY: MM DATE: 4/11/2025

CHECKED BY: - DATE: 4/11/2025

DRAWING NUMBER: A5.0 REV: 0



These Drawings contain confidential proprietary information and are the property of Risen Home Design. These drawings are NOT to be reproduced, copied whole or in part, disclosed, used for construction or any other purpose without prior written permission from Risen Home Design.

[illegible]

SHEET TITLE ELEVATIONS

RHD PROJECT NUMBER:		RHD-1323	
DRAWN BY: MM		DATE: 4/11/2025	
CHECKED BY: -		DATE: 4/11/2025	
DRAWING NUMBER:			REV:
A5.1			0

NOTE: RISEN HOME DESIGN PLANS DO NOT CARRY AN ENGINEER'S AND/OR ARCHITECT'S STAMP(S) SOME CONDITIONS MAY ARISE DURING DESIGN. AND/OR CONSTRUCTION THAT MAY REQUIRE AN ARCHITECT'S AND/OR ENGINEER'S STAMP TO COMPLY WITH LOCAL BUILDING CODES. THE CONTRACTOR IS TO VERIFY THESE CONDITIONS AND SECURE REQUIRED STAMPS PRIOR TO CONSTRUCTION

DRAWINGS & SPECIFICATIONS
IT IS THE INTENT OF THE DRAWINGS AND SPECIFICATIONS TO BE GUIDELINES FOR CONSTRUCTION. THE CONTRACTOR IS RESPONSIBLE FOR DETERMINING ANY QUESTIONS AND MEANINGS IN THE WORKING DRAWINGS AND SPECIFICATIONS AND THE CONTRACTOR SHALL NOTIFY THE DESIGNER IN WRITING OF ANY ERRORS, OMISSIONS, OR UNSUITABLE DETAILING WHICH MAY CAUSE CONSTRUCTION PROBLEMS. THE DESIGNER'S LIABILITY REGARDING ANY OMISSIONS AND/OR ERRORS ASSIGNED TO THE CORRECTION OF THE ORIGINAL DRAWINGS, CONSULTANT'S LIABILITY IS THE SAME.



GENERAL CONDITIONS

DRAWINGS & SPECIFICATIONS

DRAWINGS & SPECIFICATIONS


IT IS THE INTENT OF THE DRAWINGS AND SPECIFICATIONS TO BE GUIDELINES FOR CONSTRUCTION. THE CONTRACTOR IS RESPONSIBLE FOR DETERMINING ANY QUESTIONS AND DISCREPANCIES IN THE WORKS, THE DRAWINGS AND SPECIFICATIONS, AND THE CONTRACTOR SHALL NOTIFY THE DESIGNER IN WRITING OF ANY ERRORS, OMISSIONS, OR UNSUITABLE DETAILING WHICH MAY CAUSE CONSTRUCTION PROBLEMS. THE DESIGNER'S LIABILITY REGARDING ERRORS AND/OR OMISSIONS WILL BE LIMITED TO THE CORRECTION OF THE ORIGINAL DRAWINGS. CONSULTANT'S LIABILITY IS THE SAME.

VENTILATION REQUIREMENTS 1:300								
AREA	SQFT	1:300	TOTAL REQD	INTAKE REQD 55%	SOFFIT VENTS 10 SQ. IN. PER LIN FT.	EXHAUST REQD 45%	RIDGE VENT 12.5 SQ. IN. PER LIN FT.	BAFFLE REQD (18.7)
1st FLOOR PLAN	2,856	9.32	1371	754	75	617	49.36	37
RV BAY	883	2.94	423	233	23	190	15.2	11
GARAGE	948	3.2	461	254	25	144	11.52	12
FRONT PORCH	195	.65	94	-	-	-	-	-
BACK PATIO	514	1.7	245	-	-	-	-	-

VENTILATION

- VENT EACH ENCLOSED ATTIC AND RAFTER BAY IRC 806.1
- 1/8in TO 1/4in MESH SCREEN OVER OPENING IRC 806.1
- NET OPENING AREA MIN 11/150in OF VENTED AREA OR 1/300in IF
- 50%-80% OF VENTING NEAR TOP OR VAPOR RETARDER 106.2
- MIN. 1in CLEARANCE TO SHEATHING NEAR VENTS IRC 106.3

- VENT EACH ENCLOSED ATTIC AND RAFTER BAY IRC 806.1
- [1/8in TO] 1/4in MESH SCREEN OVER OPENING IRC 806.1
- NET OPENING AREA MIN 1/150th OF VENTING AREA OR 1/300th IF 50%-60% OF VENTING NEAR TOP OR VAPOR RETARDER IRC 806.2
- MIN. 1in CLEARANCE TO SHEATHING NEAR VENTS IRC 806.3

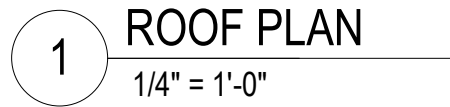


NOTE: RISEN HOME DESIGN PLANS DO NOT CARRY AN ENGINEER'S AND/OR ARCHITECT'S STAMP(S) SOME CONDITIONS MAY ARISE DURING DESIGN. AND/OR CONSTRUCTION THAT MAY REQUIRE AN ARCHITECT'S AND/OR ENGINEER'S STAMP TO COMPLY WITH LOCAL BUILDING CODES. THE CONTRACTOR IS TO VERIFY THESE CONDITIONS AND SECURE REQUIRED STAMPS PRIOR TO CONSTRUCTION

1. TRUSS LAYOUT AND DESIGN TO BE SPECIFIED BY LOCAL TRUSS COMPANY. BUILDING CONTRACTOR TO VERIFY ALL TRUSS LAYOUTS WITH TRUSS COMPANY BEFORE ORDERING. ALL TRUSS PROBLEMS TO BE ADDRESSED BY CONTRACTOR AND TRUSS COMPANY.
2. ALL ROOF AND SOFFIT VENTS TO BE INSTALLED ACCORDING TO U.B.C. AND APPLICABLE LOCAL CODES.
3. ALL TOTAL SPANS MAY VARY DEPENDING ON GIRDER TRUSS PLACEMENT. (IF NEEDED).
4. WINDOW HEADERS, GARAGE DOOR HEADER AND MICRO-LAM BEAMS UNDER ROOF LOAD TO BE SPECIFIED BY LOCAL TRUSS COMPANY.
5. TRUSS COMPANY TO CONFIRM DESIGN ROOF SNOW LOAD SHOWN WITH COUNTY REQUIREMENTS OF THIS HOUSE LOCATION.


LOCATION: (CITY) MIDDLETON (COUNTY) CANYON

- DESIGN ROOF SNOW LOAD: 25PSF
- DESIGN WIND SPEED: 115MPH
- DESIGN WIND EXPOSURE TYPE: C1
- DESIGN EARTH QUAKE ZONE: D1
- FROST DEPTH: 24"

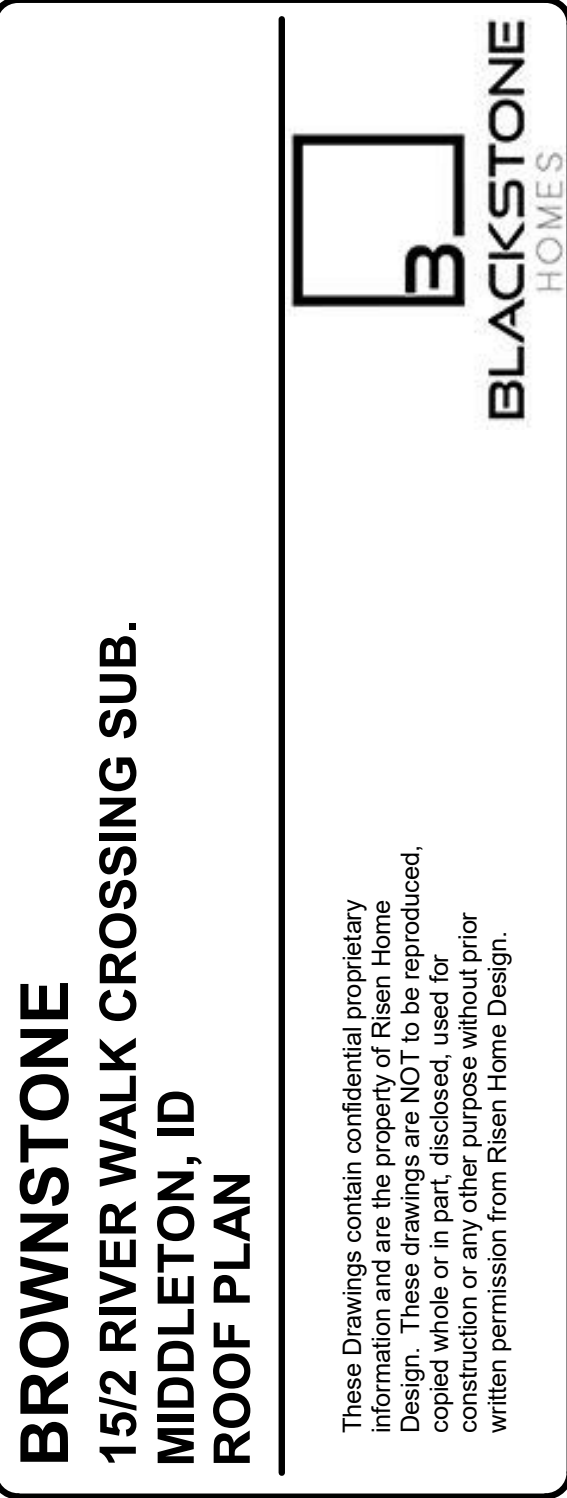[illegible]

RHD PROJECT NUMBER:		RHD-1323
DRAWN BY:	MM	DATE: 5/4/2025
CHECKED BY:	-	DATE: 5/4/2025
DRAWING NUMBER:		REV:
A6.0		0

IT IS THE INTENT OF THE DRAWINGS AND SPECIFICATIONS TO BE GUIDELINES FOR CONSTRUCTION. THE CONTRACTOR IS RESPONSIBLE FOR DETERMINING ANY QUESTIONS AND MEANINGS IN THE WORKING DRAWINGS AND SPECIFICATIONS AND THE CONTRACTOR SHALL NOTIFY THE DESIGNER IN WRITING OF ANY ERRORS, OMISSIONS, OR UNSUITABLE DETAILING WHICH MAY CAUSE CONSTRUCTION PROBLEMS. THE DESIGNER'S LIABILITY REGARDING ERRORS AND/OR OMISSIONS WILL BE LIMITED TO THE CORRECTION OF THE ORIGINAL DRAWINGS. CONSULTANT'S LIABILITY IS THE SAME.

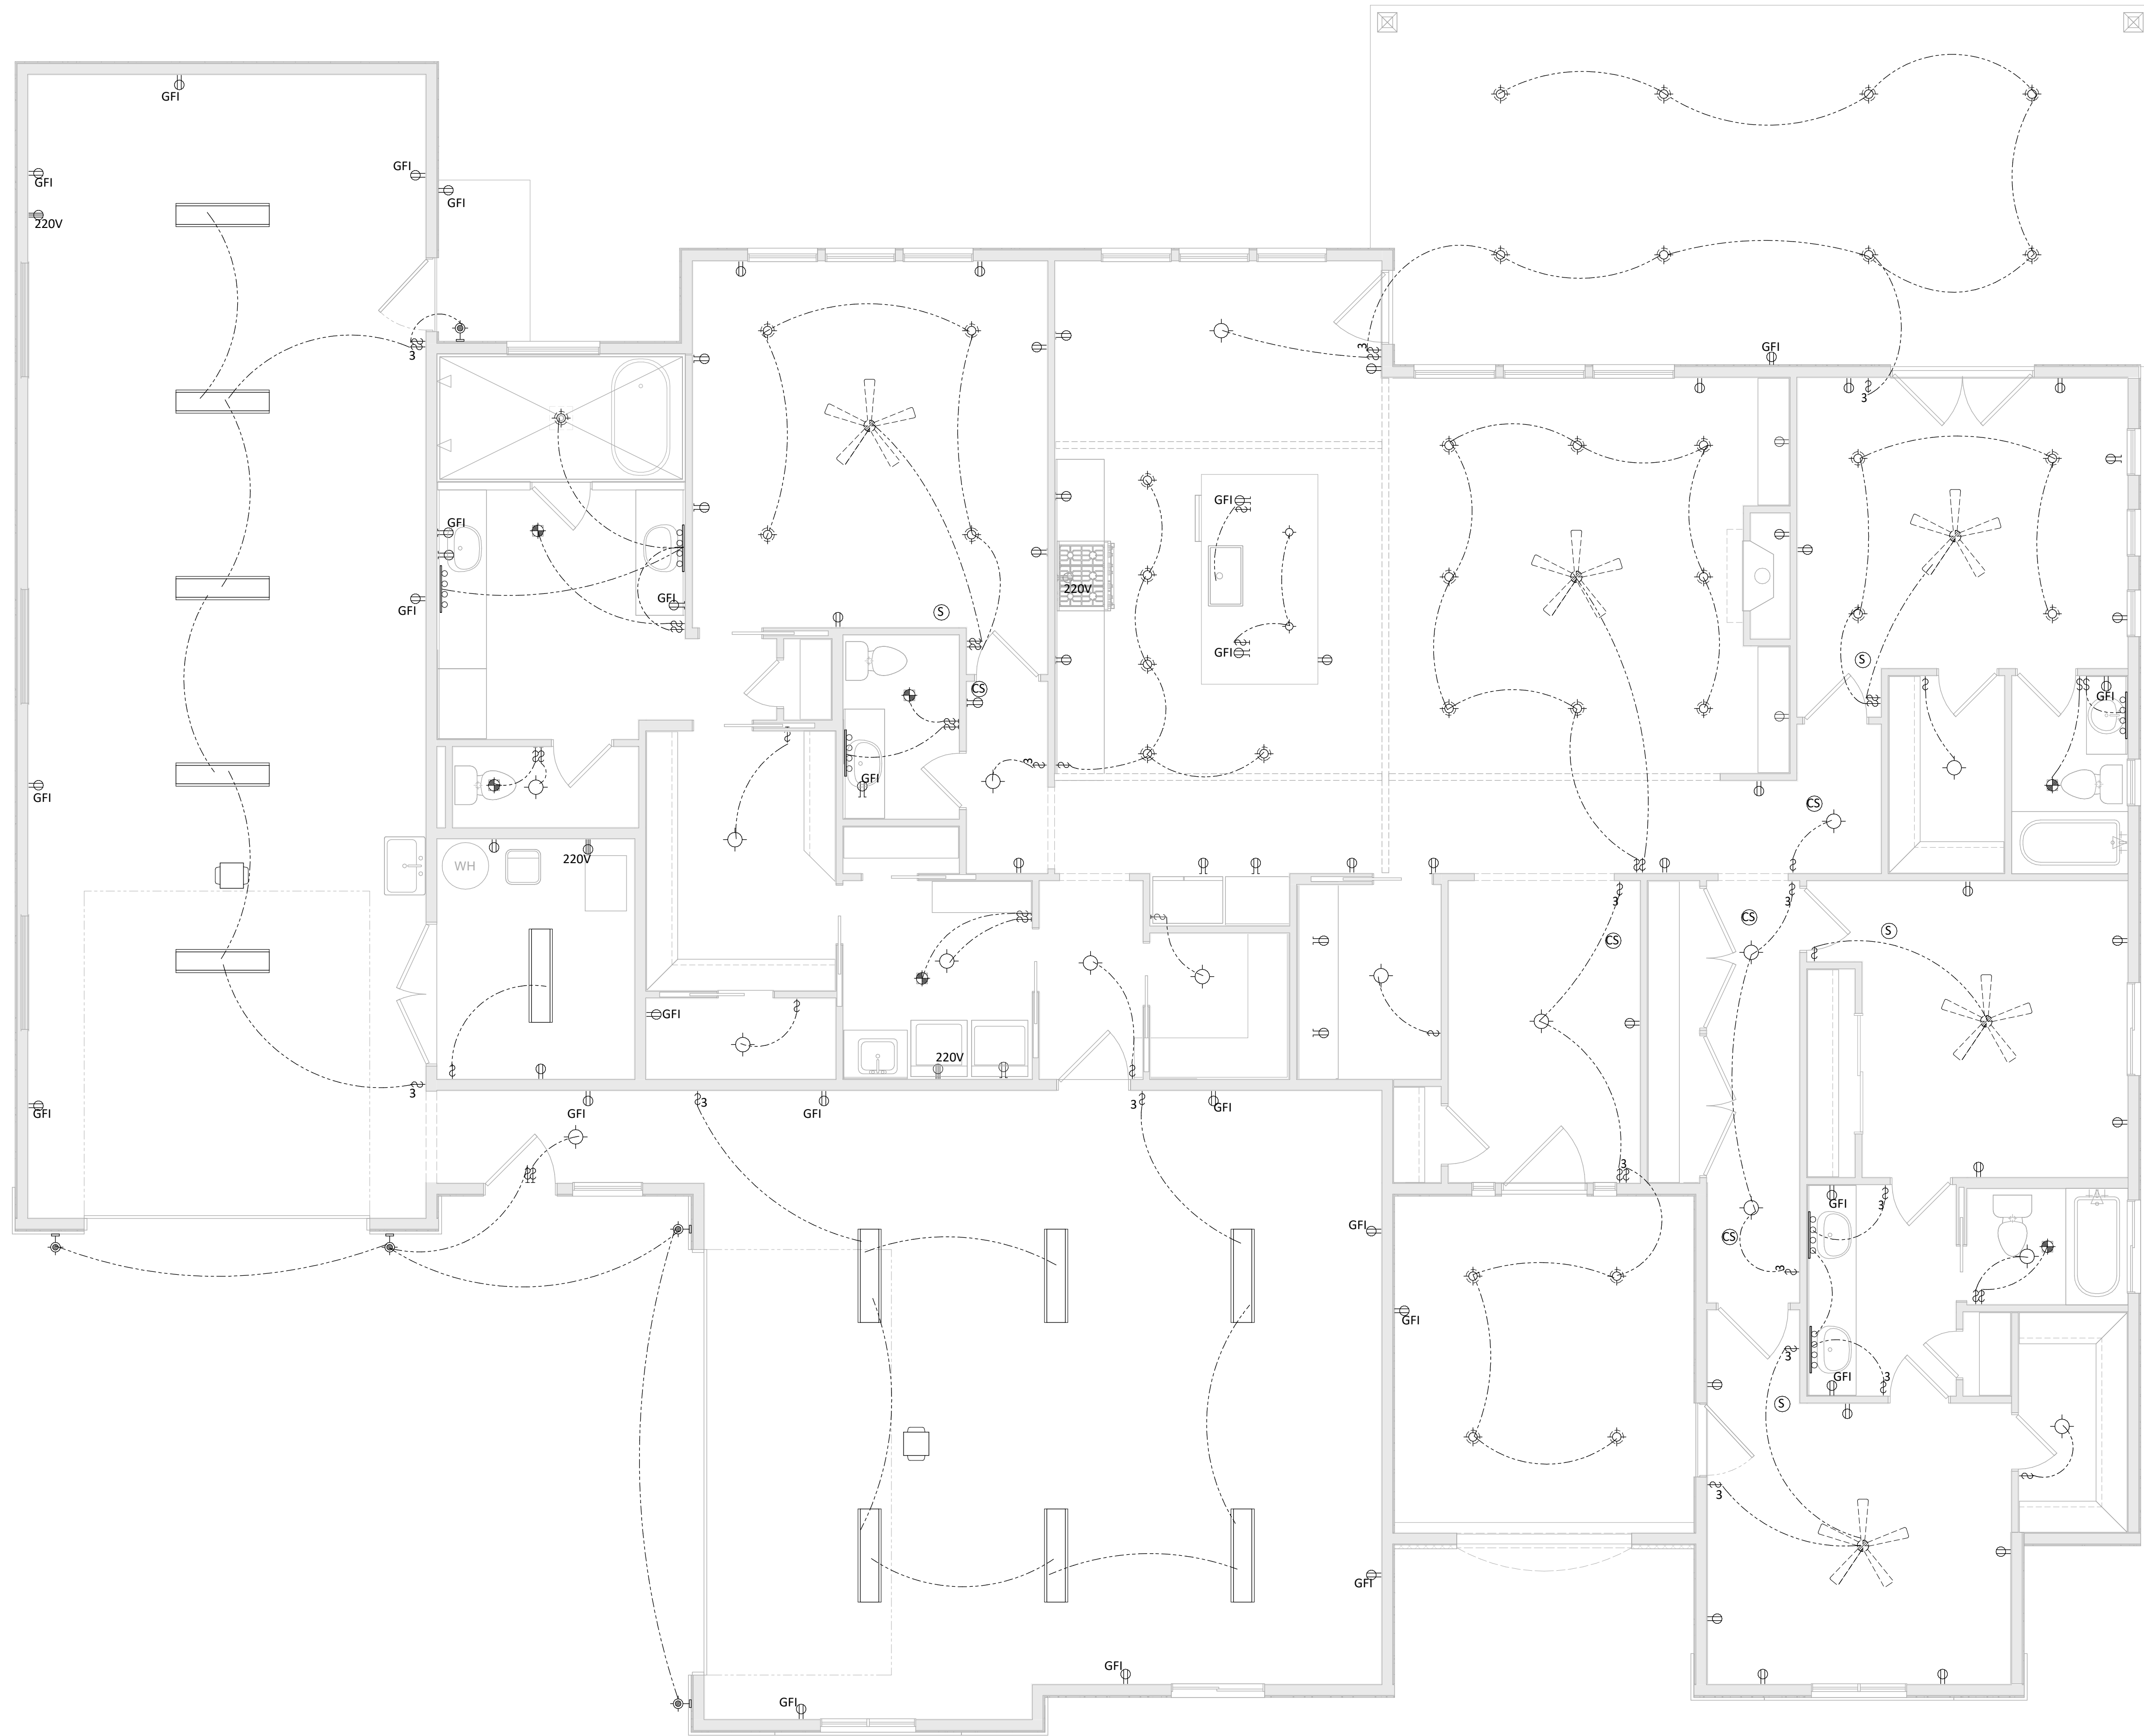

ELECTRICAL LEGEND			
	SINGLE POLE SWITCH		DOOR BELL BUTTON
	3-WAY SWITCH		DOOR BELL CHIME
	4-WAY SWITCH		GARAGE DOOR BUTTON
	DIMMER SWITCH		GARAGE DOOR OPENER
	220V OUTLET		WEATHERPROOF OUTLET
	DUPLEX OUTLET		CEILING OUTLET
	GROUND FAULT OUTLET		FLOOR OUTLET
	SMOKE DETECTOR		CARBON MONOXIDE & SMOKE DETECTOR
	CARBON MONOXIDE DETECTOR		TELEPHONE OUTLET
	TELEVISION OUTLET		GARBAGE DISPOSAL
	SERVICE PANEL		ACCENT LIGHT
	SERVICE METER		SINGLE SCONCE
	WALL MOUNT LIGHT		DOUBLE SCONCE
	FLOOD LIGHT		STAR LIGHT
	STRIP LIGHT		BATH FAN
	BATH FAN & LIGHT		UNDER CABINET LIGHT
	CLOSET LIGHT		KEYLESS LIGHT
	PULL CHAIN LIGHT		HANGING LIGHT
	FLUSH MOUNT LIGHT		MINIATURE PLUG LIGHT
	HANGING PENDANT LIGHT		RECESSED EYERALL LIGHT
	RECESSED CAN LIGHT		FLUORESCENT LIGHT RECTANGULAR
	CEILING FAN		LIGHT w/ FAN ROUGH
	LIGHTED CEILING FAN		LIGHT & FAN ROUGH

CO/ Smoke
Detector Required
IRC R314.3 & or
R315.3

Hose Bibs are
required to be 12" off
of the finish grade
per Middleton Code
BOD6

1 1ST FLOOR ELECTRICAL PLAN
1/4" = 1'-0"

NOTE: RISEN HOME DESIGN PLANS DO NOT CARRY AN ENGINEER'S AND/OR ARCHITECT'S STAMP(S) SOME CONDITIONS MAY ARISE DURING DESIGN, AND/OR CONSTRUCTION THAT MAY REQUIRE AN ARCHITECT'S AND/OR ENGINEER'S STAMP TO COMPLY WITH LOCAL BUILDING CODES. THE CONTRACTOR IS TO VERIFY THESE CONDITIONS AND SECURE REQUIRED STAMPS PRIOR TO CONSTRUCTION

GENERAL CONDITIONS			
DRAWINGS & SPECIFICATIONS			
IT IS THE INTENT OF THE DRAWINGS AND SPECIFICATIONS TO BE GUIDELINES FOR CONSTRUCTION. THE CONTRACTOR IS RESPONSIBLE FOR DETERMINING ANY QUESTIONS AND MEANINGS IN THE WORKING DRAWINGS AND SPECIFICATIONS AND THE CONTRACTOR SHALL NOTIFY THE DESIGNER IN WRITING OF ANY ERRORS, OMISSIONS, OR UNSUITABLE DETAILING WHICH MAY CAUSE CONSTRUCTION PROBLEMS. THE DESIGNER'S LIABILITY REGARDING ERRORS AND/OR OMISSIONS WILL BE LIMITED TO THE CORRECTION OF THE ORIGINAL DRAWINGS. CONSULTANT'S LIABILITY IS THE SAME.			

390 E. CORPORATE DR STE 112
MERCIDIAN, ID 83842
#208-283-3775

BROWNSTONE
15/2 RIVER WALK CROSSING SUB.
MIDDLETON, ID
FLOOR ELECTRICAL PLAN

These Drawings contain confidential proprietary information and are the property of Risen Home Design. These drawings are NOT to be reproduced, copied whole or in part, disclosed, used for construction or any other purpose without prior written permission from Risen Home Design.

REVISIONS	
NO.	DATE
0	5/4/2025

SHEET TITLE	
ELECTRICAL PLAN	
RHD PROJECT NUMBER: RHD-1323	
DRAWN BY: MM	DATE: 5/4/2025
CHECKED BY: -	DATE: 5/4/2025
DRAWING NUMBER: A7.0	REV: 0




These Drawings contain confidential proprietary information and are the property of Risen Home Design. These drawings are NOT to be reproduced, copied whole or in part, disclosed, used for construction or any other purpose without prior written permission from Risen Home Design.


[illegible]

CUT SECTION VIEWS


RHD PROJECT NUMBER:		RHD-1323	
DRAWN BY: MM		DATE: 5/4/2025	
CHECKED BY: -		DATE: 5/4/2025	
DRAWING NUMBER:			REV:
A8.1			0

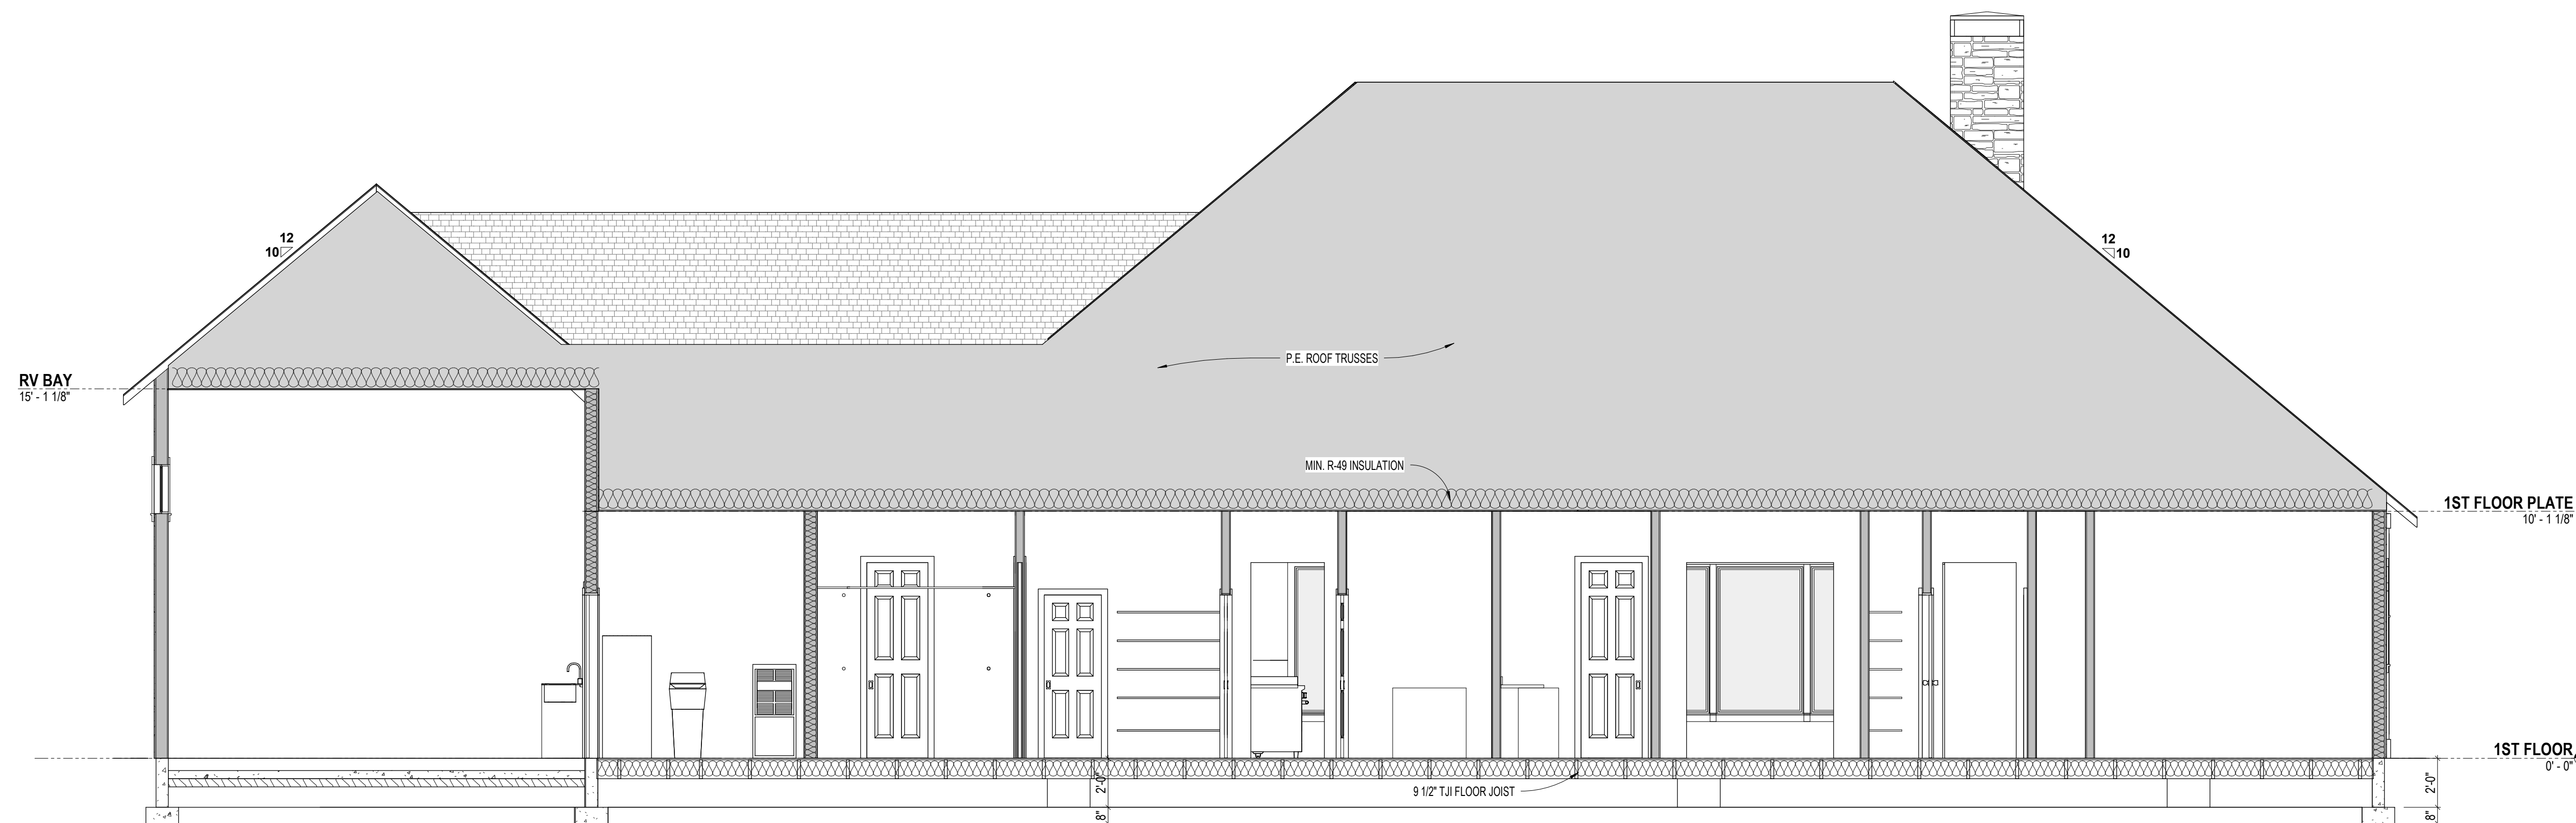

1 BUILDING SECTION-1
1/4" = 1'-0"

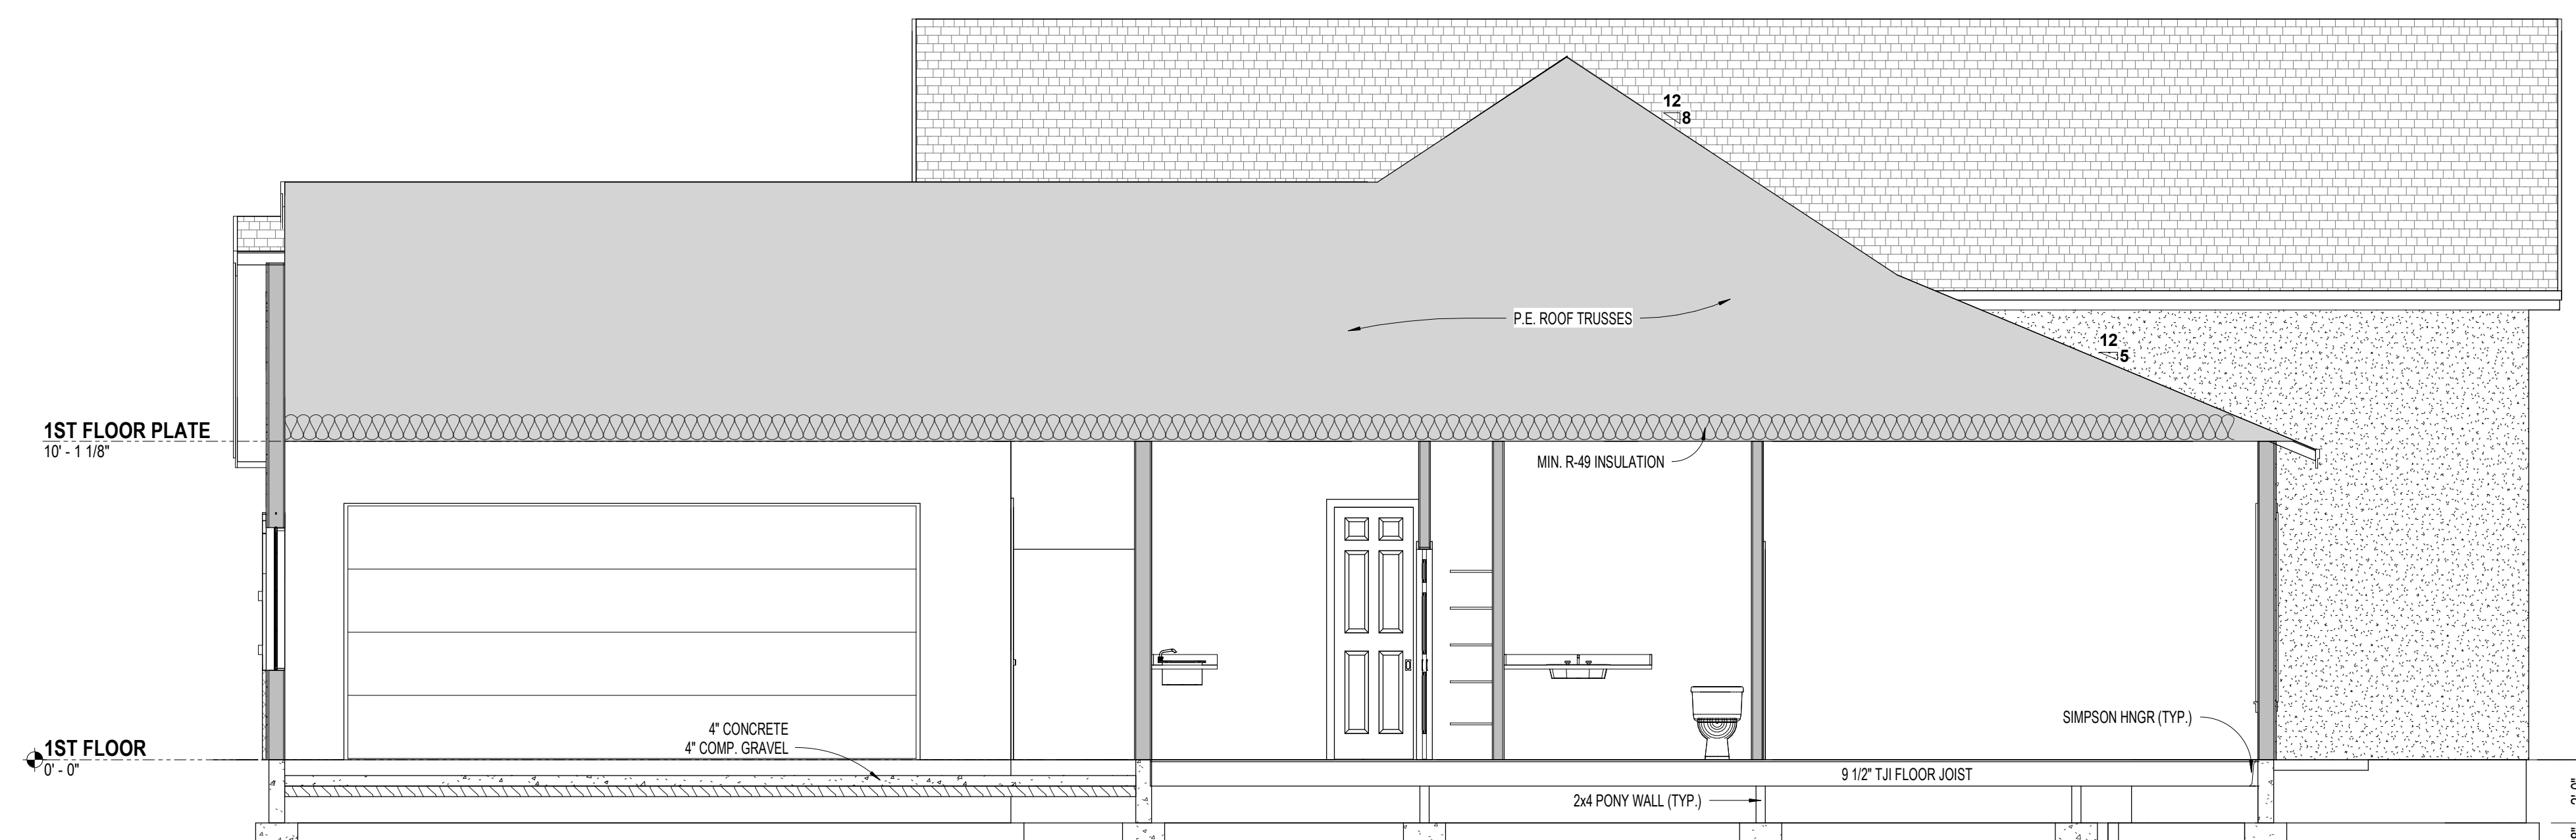

2 BUILDING SECTION-2
1/4" = 1'-0"

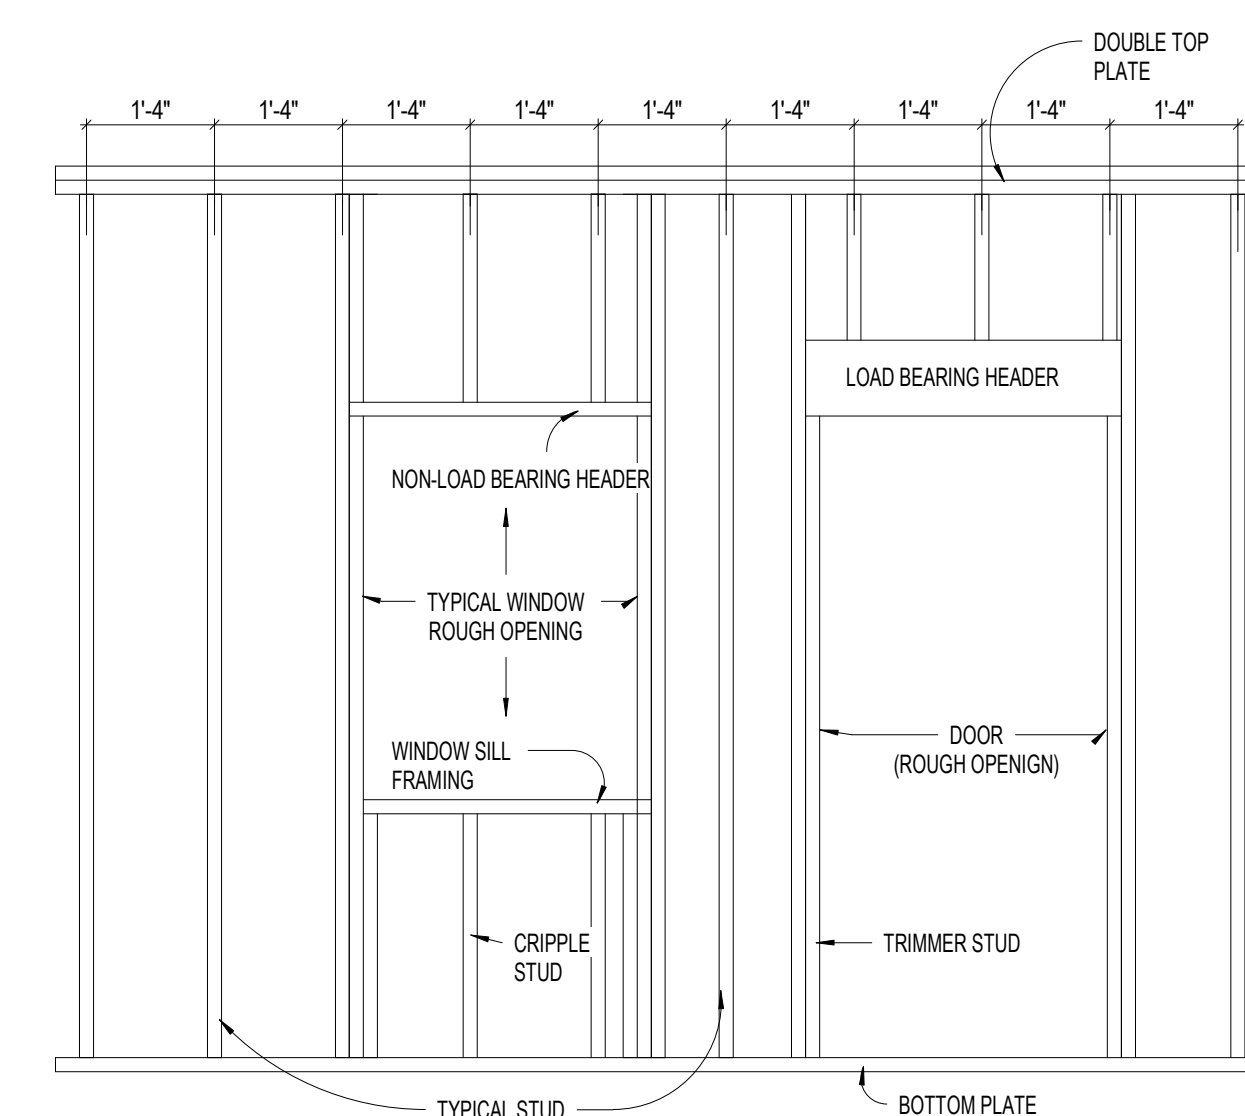

3 FRAMING DETAIL
1/2" = 1'-0"

NOTE: RISEN HOME DESIGN PLANS DO NOT CARRY AN ENGINEER'S AND/OR ARCHITECT'S STAMP(S) SOME CONDITIONS MAY ARISE DURING DESIGN. AND/OR CONSTRUCTION THAT MAY REQUIRE AN ARCHITECT'S AND/OR ENGINEER'S STAMP TO COMPLY WITH LOCAL BUILDING CODES. THE CONTRACTOR IS TO VERIFY THESE CONDITIONS AND SECURE REQUIRED STAMPS PRIOR TO CONSTRUCTION

DRAWINGS & SPECIFICATIONS

IT IS THE INTENT OF THE DRAWINGS AND SPECIFICATIONS TO BE GUIDELINES FOR CONSTRUCTION. THE CONTRACTOR IS RESPONSIBLE FOR DETERMINING ANY QUESTIONS AND MEANINGS IN THE WORKING DRAWINGS AND SPECIFICATIONS AND THE CONTRACTOR SHALL NOTIFY THE DESIGNER IN WRITING OF ANY ERRORS, OMISSIONS, OR UNSUITABLE DETAILING WHICH MAY CAUSE CONSTRUCTION PROBLEMS. THE DESIGNER'S LIABILITY REGARDING ERRORS AND/OR OMISSIONS WILL BE LIMITED TO THE CORRECTION OF THE ORIGINAL DRAWINGS. CONSULTANT'S LIABILITY IS THE SAME.