

DRAWINGS & SPECIFICATIONS

IT IS THE INTENT OF THE DRAWINGS AND SPECIFICATIONS TO BE GUIDELINES FOR CONSTRUCTION. THE CONTRACTOR IS RESPONSIBLE FOR DETERMINING ANY QUESTIONS AND MEANINGS IN THE WORKING DRAWINGS AND SPECIFICATIONS AND THE CONTRACTOR SHALL NOTIFY THE DESIGNER IN WRITING OF ANY QUESTIONS, OMISSIONS, OR UNUSABLE DETAILS WHICH MAY CAUSE CONSTRUCTION PROBLEMS. THE DESIGNER'S LIABILITY REGARDING ERRORS AND/OR OMISSIONS WILL BE LIMITED TO THE CORRECTION OF THE ORIGINAL DRAWINGS. CONSULTANT'S LIABILITY IS THE SAME.

This is page 1 of 2




1



IT IS THE INTENT OF THE DRAWINGS AND SPECIFICATIONS TO BE GUIDELINES FOR CONSTRUCTION. THE CONTRACTOR IS RESPONSIBLE FOR DETERMINING ANY QUESTIONS AND MEANINGS IN THE WORKING DRAWINGS AND SPECIFICATIONS AND THE CONTRACTOR SHALL NOTIFY THE DESIGNER IN WRITING OF ANY ERRORS, OMISSIONS, OR UNSUITABLE DETAILING WHICH MAY CAUSE CONSTRUCTION PROBLEMS. THE DESIGNER'S LIABILITY REGARDING ERRORS AND/OR OMISSIONS WILL BE LIMITED TO THE CORRECTION OF THE ORIGINAL DRAWINGS. CONSULTANT'S LIABILITY IS THE SAME.

DRAWING NUMBER:	REV
-----------------	-----

REV
0

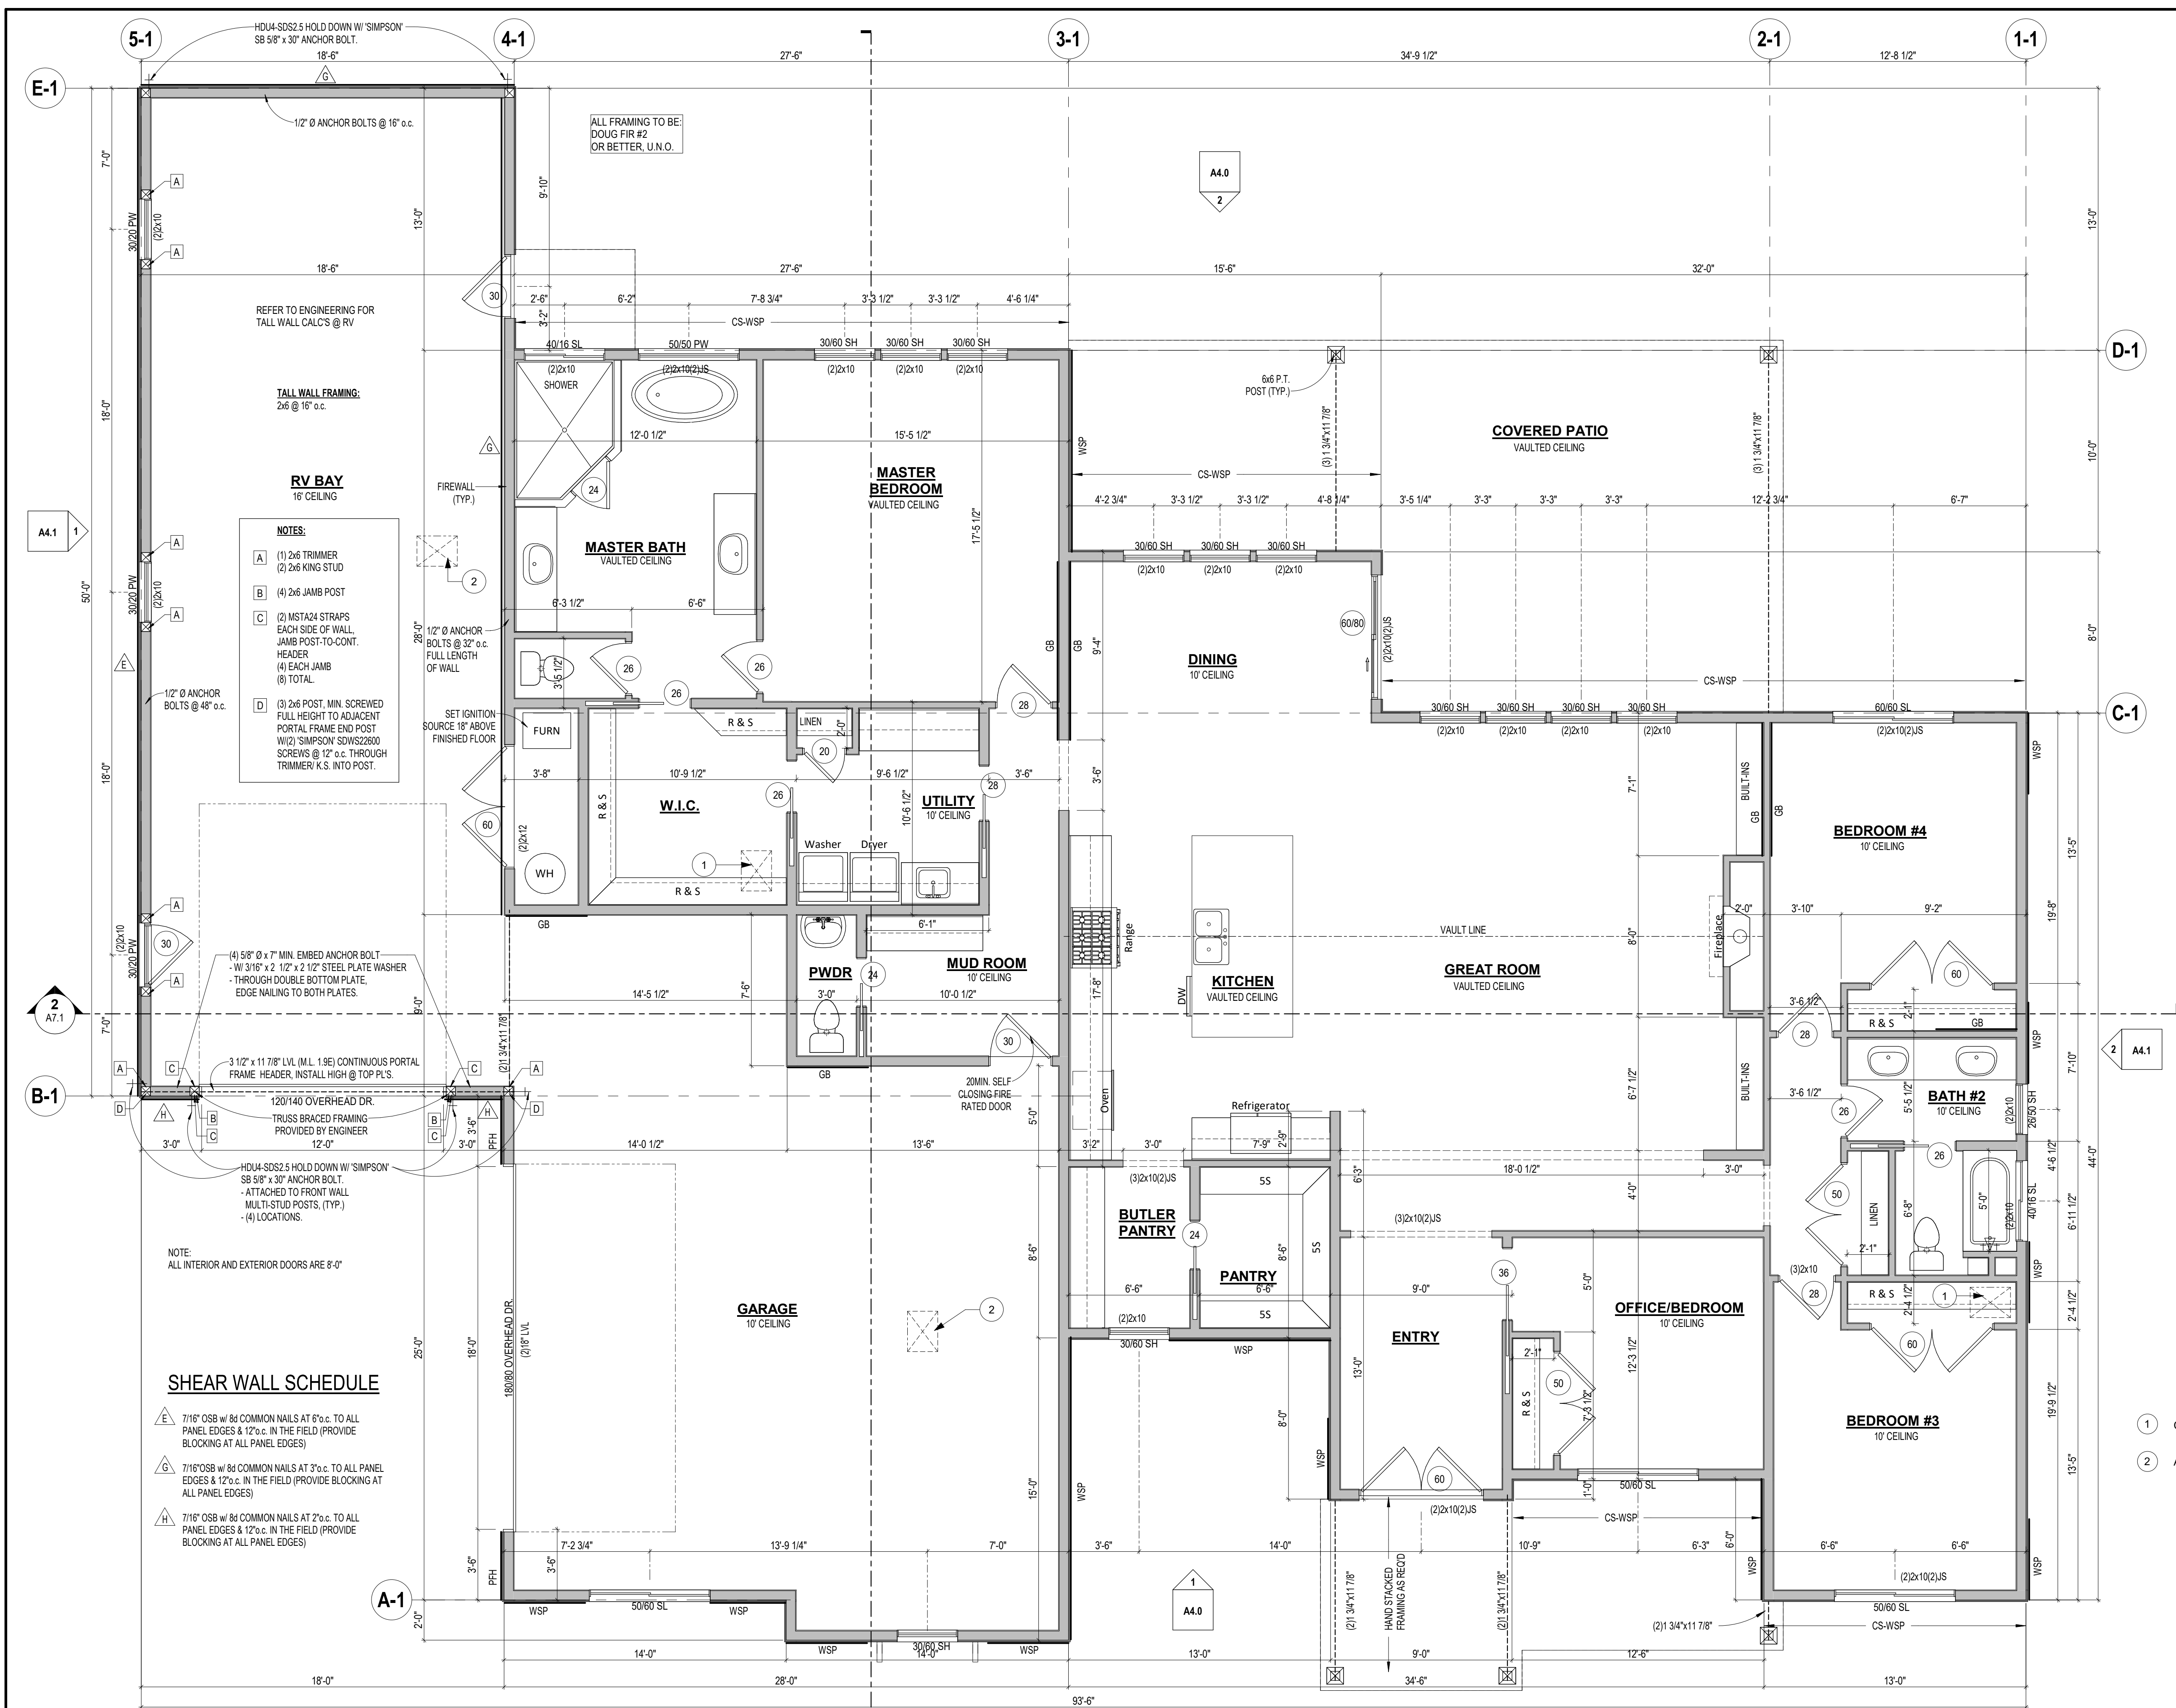

FLOOR PLAN NOTES

- ALL STRUCTURAL LUMBER SIZED FOR #2 OR BETTER DOUG FIR LARCH
- 2x EXTERIOR STUD FRAMING @ 16" O.C. W/ SINGLE BOTTOM PLATE AND DOUBLE TOP PLATE
- 4x8 HEADERS IN ALL BEARING WALL OPENING UNLESS OTHERWISE NOTED
- ALLOW FOR A 22" x 30" (MIN) ATTIC AND CRAWL SPACE ACCESS
- ALL METAL CONNECTIONS TO BE SIMPSON CO. OR BETTER
- 5/8" TYPE 'X' GYP BOARD @ ALL GARAGE COMMON WALLS AND CEILINGS APPLIED TO GARAGE SIDE AND ALL WALLS, BEAMS, POSTS AND OTHER STRUCTURAL MEMBERS SUPPORTING FIRE PROTECTED HORIZONTAL STRUCTURAL MEMBERS
- DOORS BETWEEN GARAGE AND DWELLING ARE TO BE SELF CLOSING AND TIGHT FITTING SOLID WOOD DOOR 1 3/8" THICK OR A DOOR W/ A FIRE PROTECTION RATING OF NOT LESS THAN 20 MINUTES
- 1/2" GYPSUM BOARD TO BE INSTALLED ON INSIDE WALLS OF HOUSE
- ALL WINDOWS TO HAVE BREATHER TUBES INSTALLED
- ROOF SYSTEM TO BE PRE-ENGINEERED MANUFACTURED ROOF TRUSSES UNLESS OTHERWISE NOTED
- ALL CONSTRUCTION PRACTICES USED IN THE CONSTRUCTION OF THIS DWELLING SHALL BE DONE IN ACCORDANCE W/ THE 2018 WHERE APPLICABLE
- VENT RANGE HOOD, FANS, AND DRYER TO OUTSIDE AIR. CONTRACTOR TO VERIFY ALL CONDITIONS AND DIMENSIONS PRIOR TO COMMENCING WORK
- ALL RESCUE WINDOWS FROM SLEEPING AREAS MUST MEET THE FOLLOWING REQUIREMENTS:
 - SHALL HAVE A NET CLEAR OPENING OF 5.1 SQ. FT.
 - MINIMUM HEIGHT OF 24"
 - MINIMUM WIDTH OF 20"
 - FINISHED SILL HEIGHT OF NOT MORE THAN 44"
- EXTERIOR DIMENSIONS ARE TO FACE OF STUD WALL. INTERIOR DIMENSIONS ARE TO FACE OF STUD WALL
- ALL FURNACE SWITCHES, PILOTS, AND BURNERS TO BE MINIMUM 18" ABOVE FINISHED FLOOR

GENERAL NOTES

ALL EXTERIOR WALL SHALL BE SHEATHED w/7/16" OSB. ATTACH WITH MIN. 16 GA. X 1 3/4" LEO STAPLES AT 6" o.c. TO ALL SUPPORTED PANEL EDGES AND AT 6" o.c. IN THE FIELD. U.N.O.

STAPLES SHALL NOT BE SUBSTITUTED FOR COMMON NAILS AT SHEAR PANELS. ALL SHEAR PANELS SHALL HAVE DOUBLE STUDS AT ENDS FOR EDGE NAILING AND ATTACHMENT OF STRAPS AND/OR HOLD DOWNS, TYP.

ALL HOLD DOWNS SHALL ALIGN AT DOUBLE STUDS AT ENDS OF SHEAR PANELS, TYP.

PROVIDE 'SIMPSON' H/ AT ALL TRUSS BEARING LOCATIONS. ALL SHEATHING SHALL BE CONTINUOUS TO FLOOR/PLATE BEHIND ALL ATTACHED ROOF FRAMING INTO WALL.

PROVIDE DOUBLE STUD ABOVE AND BELOW ALIGNED AT STRAPS BETWEEN FLOORS FOR STRAP ATTACHMENT. WITH PANEL EDGE NAILING FOR FULL HEIGHT OF DOUBLE STUD.

PROVIDE GALVANIZED NAILS INTO PRESERVATION TREATED SILL PLATES. NAIL SIZE AND SPACING TO MATCH SHEAR WALL SPECIFIED. PROVIDE 8d GALVANIZED NAILS AT SAME SPACING WHERE STAPLES USED.

AT MINIMUM, PROVIDE REINFORCING BARS IN FOUNDATION AT HOLD DOWN LOCATIONS PER MANUFACTURERS REQUIREMENTS

SQ./FT.

LIVING	2781 SF
GARAGE	869 SF
RV BAY	945 SF
FRONT PORCH	200 SF
BACK PATIO	532 SF

DOOR/WINDOW TAG EXAMPLE

DOOR TAG	WINDOW TAG
28 = 2'-6"	40/56 SH = 4'-0" x 5'-6" SINGLE HUNG

SHEET NOTES

- CRAWL SPACE ACCESS. COORDINATE WITH JOIST LAYOUT.
- ATTIC SPACE ACCESS. COORDINATE WITH TRUSS LAYOUT.

NOTE: VERIFY ALL WINDOW/DOOR ROUGH OPENING AND HEADER HEIGHT AND THE SAME FOR TRIM PACKAGE. VERIFY STANDARD HEIGHTS WITH CONTRACTOR BEFORE FRAMING.

SEE 2018 IRC

DRAWINGS & SPECIFICATIONS

IT IS THE INTENT OF THE DRAWINGS AND SPECIFICATIONS TO BE GUIDELINES FOR CONSTRUCTION. THE CONTRACTOR IS RESPONSIBLE FOR DETERMINING ANY QUESTIONS AND MEANINGS IN THE WORKING DRAWINGS AND SPECIFICATIONS AND THE CONTRACTOR SHALL NOTIFY THE DESIGNER IN WRITING OF ANY ERRORS, OMISSIONS, OR UNSUITABLE DETAILING WHICH MAY CAUSE CONSTRUCTION PROBLEMS. THE DESIGNER'S LIABILITY REGARDING ERRORS AND/OR OMISSIONS WILL BE LIMITED TO THE CORRECTION OF THE ORIGINAL DRAWINGS. CONSULTANT'S LIABILITY IS THE SAME.

GENERAL CONDITIONS

R302.7 PROVIDE UNDERSTAIR PROTECTION AS REQUIRED
R302.11 PROVIDE FIREBLOCKING AS REQUIRED
R303.7 PROVIDE SWITCHING AND ILLUMINATION AS REQUIRED
R305 PROVIDE SUFFICIENT CEILING HEIGHTS
R311.7 MEET STAIRWAY REQUIREMENTS
R312 MEET GUARD REQUIREMENTS

BRACING DETAILS

METHOD	MATERIAL	CONNECTION CRITERIA
WSP	WOOD STRUCTURAL PANEL (SEE SECTION R604)	EXTERIOR SHEATHING: SEE IRC TABLE R602(3) INTERIOR SHEATHING: SEE IRC TABLE R602(3)
PFH	INTERMITTENT PORTAL FRAME	SEE SECTION R602.10.3.3
ABW	ALTERNATE BRACED WALL	SEE SECTION R602.10.3.2
GB	GYPSUM BOARD	SEE SECTION R702.3.5

1st FLOOR PLAN

1/4" = 1'-0"

TABLE R402.1.1 INSULATION AND FENESTRATION REQUIREMENTS BY COMPONENT									
CLIMATE ZONE	FENESTRATION U-FACTOR	SKYLIGHT U-FACTOR	GLAZED FENESTRATION SHGC	CEILING R-VALUE	WOOD FRAM WALL R-VALUE	MASS WALL R-VALUE	FLOOR R-VALUE	BASEMENT WALL R-VALUE	SLAB R-VALUE
5 AND MARINE 4	0.35	0.60	NR	38	20 OR 13+5 ^h	13/17	30 ^g	10/13	10, 2 ft

NOTE: RISEN HOME DESIGN PLANS DO NOT CARRY AN ENGINEER'S AND/OR ARCHITECT'S STAMP(S) SOME CONDITIONS MAY ARISE DURING DESIGN, AND/OR CONSTRUCTION THAT MAY REQUIRE AN ARCHITECT'S AND/OR ENGINEER'S STAMP TO COMPLY WITH LOCAL BUILDING CODES. THE CONTRACTOR IS TO VERIFY THESE CONDITIONS AND SECURE REQUIRED STAMPS PRIOR TO CONSTRUCTION



WHITESTONE
LOT#29 BLK#3 PURPLE SAGE ESTATE
CALDWELL, ID
1st FLOOR PLAN

These Drawings contain confidential proprietary information and are the property of Risen Home Design. These drawings are NOT to be reproduced, copied whole or in part disclosed, used for construction or any other purpose without prior written permission from Risen Home Design.

BLACKSTONE
HOMES

REVISIONS

NO.	DESCRIPTION	DATE
0	ISSUE FOR CONSTRUCTION	10/5/2023
1	ISSUE FOR CONSTRUCTION	10/13/2023

SHEET TITLE

1st FLOOR
PLAN

RHD PROJECT NUMBER: RHD-996

DRAWN BY: MM DATE: 10/5/2023



CHECKED BY: - DATE: 10/5/2023

DRAWING NUMBER: A3.0 REV: 1



RISEN
Home Design

390 E CORPORATE DR. STE 112
MERIDIAN, ID 83642
#208-283-3775

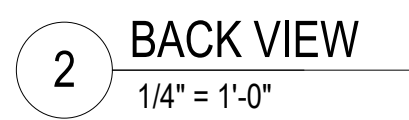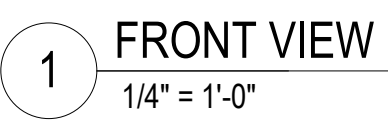


DRAWINGS & SPECIFICATIONS

IT IS THE INTENT OF THE DRAWINGS AND SPECIFICATIONS TO BE GUIDELINES FOR CONSTRUCTION. THE CONTRACTOR IS RESPONSIBLE FOR DETERMINING ANY QUESTIONS AND MEANINGS IN THE WORKING DRAWINGS AND SPECIFICATIONS AND THE CONTRACTOR SHALL NOTIFY THE DESIGNER IN WRITING OF ANY ERRORS, OMISSIONS, OR UNSUITABLE DETAILING WHICH MAY CAUSE CONSTRUCTION PROBLEMS. THE DESIGNER'S LIABILITY REGARDING ERRORS AND/OR OMISSIONS WILL BE LIMITED TO THE CORRECTION OF THE ORIGINAL DRAWINGS. CONSULTANT'S LIABILITY IS THE SAME.

[illegible]

SHEET TITLE ELEVATIONS	
RHD PROJECT NUMBER: DRAWN BY: MM CHECKED BY: - DRAWING NUMBER: RHD-996 DATE: 10/5/2023 DATE: 10/5/2023 A4.0 1	

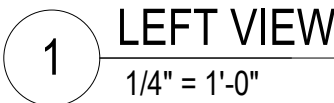


DRAWINGS & SPECIFICATIONS

IT IS THE INTENT OF THE DRAWINGS AND SPECIFICATIONS TO BE GUIDELINES FOR CONSTRUCTION. THE CONTRACTOR IS RESPONSIBLE FOR DETERMINING ANY QUESTIONS AND MEANINGS IN THE WORKING DRAWINGS AND SPECIFICATIONS AND THE CONTRACTOR MUST NOTIFY THE DESIGNER IN WRITING OF ANY ERRORS, OMISSIONS, OR UNSATISFACTORY DETAILING WHICH MAY CAUSE CONSTRUCTION PROBLEMS. THE DESIGNER'S LIABILITY REGARDING ERRORS AND/OR OMISSIONS WILL BE LIMITED TO THE CORRECTION OF THE ORIGINAL DRAWINGS. CONSULTANT'S LIABILITY IS THE SAME.



These Drawings contain confidential proprietary information and are the property of Risen Home Design. These drawings are NOT to be reproduced, copied whole or in part, disclosed, used for construction or any other purpose without prior written permission from Risen Home Design.

SHEET TITLE	
ELEVATIONS	
RHD PROJECT NUMBER:	RHD-996
DRAWN BY: MM	DATE: 10/5/2023
CHECKED BY: -	DATE: 10/5/2023
DRAWING NUMBER:	REV:
A4.1	1

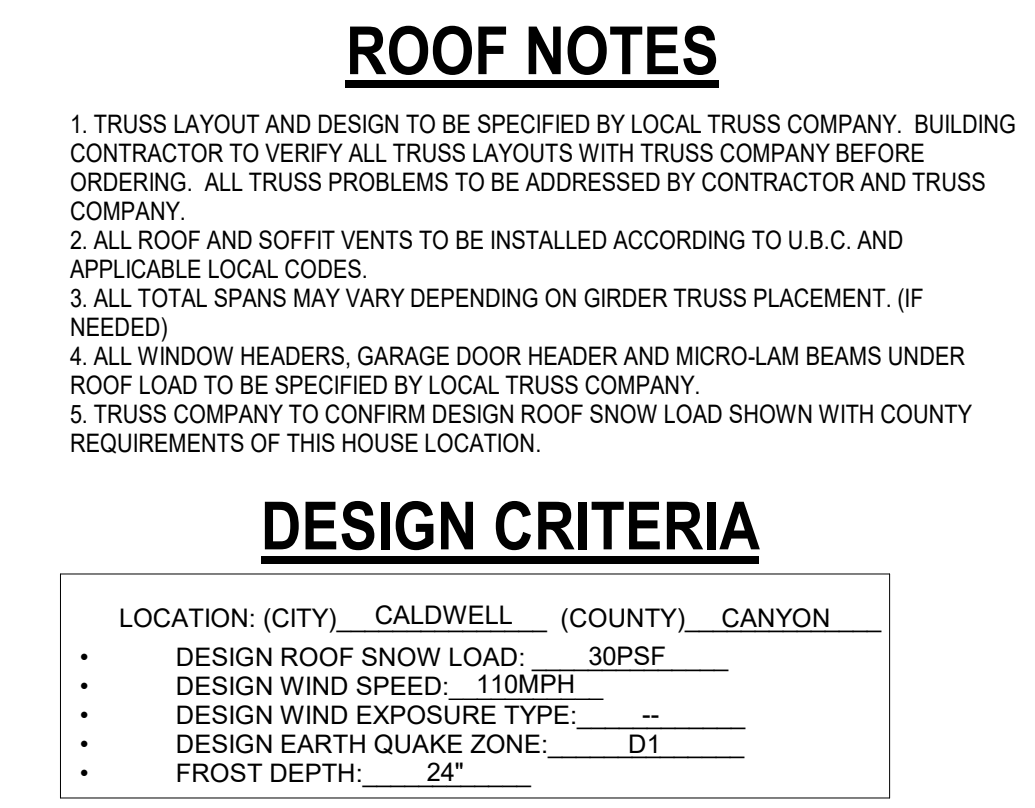

DESIGN CRITERIA

1. TRUSS LAYOUT AND DESIGN TO BE SPECIFIED BY LOCAL TRUSS COMPANY. BUILDING CONTRACTOR TO VERIFY ALL TRUSS LAYOUTS WITH TRUSS COMPANY BEFORE ORDERING. ALL TRUSS PROBLEMS TO BE ADDRESSED BY CONTRACTOR AND TRUSS COMPANY.
2. ALL ROOF AND SOFFIT VENTS TO BE INSTALLED ACCORDING TO U.B.C. AND APPLICABLE LOCAL CODES.
3. ALL TOTAL SPANS MAY VARY DEPENDING ON GIRDER TRUSS PLACEMENT. (IF NEEDED)
4. ALL WINDOW HEADERS, GARAGE DOOR HEADER AND MICRO-LAM BEAMS UNDER ROOF LOAD TO BE SPECIFIED BY LOCAL TRUSS COMPANY.
5. TRUSS COMPANY TO CONFIRM DESIGN ROOF SNOW LOAD SHOWN WITH COUNTY REQUIREMENTS OF THIS HOUSE LOCATION.

LOCATION: (CITY) CALDWELL (COUNTY) CANYON

- DESIGN ROOF SNOW LOAD: 30PSF
- DESIGN WIND SPEED: 110MPH
- DESIGN WIND EXPOSURE TYPE: --
- DESIGN EARTH QUAKE ZONE: D1
- FROST DEPTH: 24"



These Drawings contain confidential proprietary information and are the property of Risen Home Design. These drawings are NOT to be reproduced, copied whole or in part, disclosed, used for construction or any other purpose without prior written permission from Risen Home Design.

REVISIONS

SHEET TITLE
ROOF PLAN

RHD PROJECT NUMBER: RHD-996

DRAWN BY:	MM	DATE:10/5/2023
-----------	----	----------------

CHECKED BY: -	DATE: 10/5/2023
---------------	-----------------

A5.0

REV:
1

NOTE: RISEN HOME DESIGN PLANS DO NOT CARRY AN ENGINEER'S AND/OR ARCHITECT'S STAMP(S) SOME CONDITIONS MAY ARISE DURING DESIGN, AND/OR CONSTRUCTION THAT MAY REQUIRE AN ARCHITECT'S AND/OR ENGINEER'S STAMP TO COMPLY WITH LOCAL BUILDING CODES. THE CONTRACTOR IS TO VERIFY THESE CONDITIONS AND SECURE REQUIRED STAMPS PRIOR TO CONSTRUCTION

GENERAL CONDITIONS

DRAWINGS & SPECIFICATIONS

IT IS THE INTENT OF THE DRAWINGS AND SPECIFICATIONS TO BE GUIDELINES FOR CONSTRUCTION. THE CONTRACTOR IS RESPONSIBLE FOR DETERMINING ANY QUESTIONS AND MEANINGS IN THE WORKING DRAWINGS AND SPECIFICATIONS AND THE CONTRACTOR SHALL NOTIFY THE DESIGNER IN WRITING OF ANY ERRORS, OMISSIONS, OR UNSUITABLE DETAILING WHICH MAY CAUSE CONSTRUCTION PROBLEMS. THE DESIGNER'S LIABILITY REGARDING ERRORS AND/OR OMISSIONS WILL BE LIMITED TO THE CORRECTION OF THE ORIGINAL DRAWINGS. CONSULTANT'S LIABILITY IS THE SAME.



DRAWINGS & SPECIFICATIONS

IT IS THE INTENT OF THE DRAWINGS AND SPECIFICATIONS TO BE GUIDELINES FOR CONSTRUCTION. THE CONTRACTOR IS RESPONSIBLE FOR DETERMINING ANY QUESTIONS AND MEANINGS IN THE WORKING DRAWINGS AND SPECIFICATIONS AND THE CONTRACTOR SHALL NOTIFY THE DESIGNER IN WRITING OF ANY ERRORS, OMISSIONS, OR INCONSISTENCIES WHICH MAY CAUSE CONSTRUCTION PROBLEMS. THE DESIGNER'S LIABILITY REGARDING ERRORS AND/OR OMISSIONS WILL BE LIMITED TO THE CORRECTION OF THE ORIGINAL DRAWINGS. CONSULTANT'S LIABILITY IS THE SAME.



RISEN
Home Design

390 E CORPORATE DR. STE. 112
MERIDIAN, ID 83642
#208-283-3775

Blackstone Homes

These Drawings contain confidential proprietary information and are the property of Risen Home Design. These drawings are NOT to be reproduced, copied whole or in part, disclosed, used for construction or any other purpose without prior written permission from Risen Home Design.

[illegible]


RHD PROJECT NUMBER:		RHD-996	
DRAWN BY: MM		DATE: 10/5/2023	
CHECKED BY: -		DATE: 10/5/2023	
DRAWING NUMBER:			REV:
A6.0			0






These Drawings contain confidential proprietary information and are the property of Risen Home Design. These drawings are NOT to be reproduced, copied whole or in part, disclosed, used for construction or any other purpose without prior written permission from Risen Home Design.

[illegible]

SHEET TITLE	
DETAILS	
RHD PROJECT NUMBER:	RHD-996
DRAWN BY: MM	DATE: 10/5/2023
CHECKED BY: -	DATE: 10/5/2023
DRAWING NUMBER:	REV:
A7.0	0

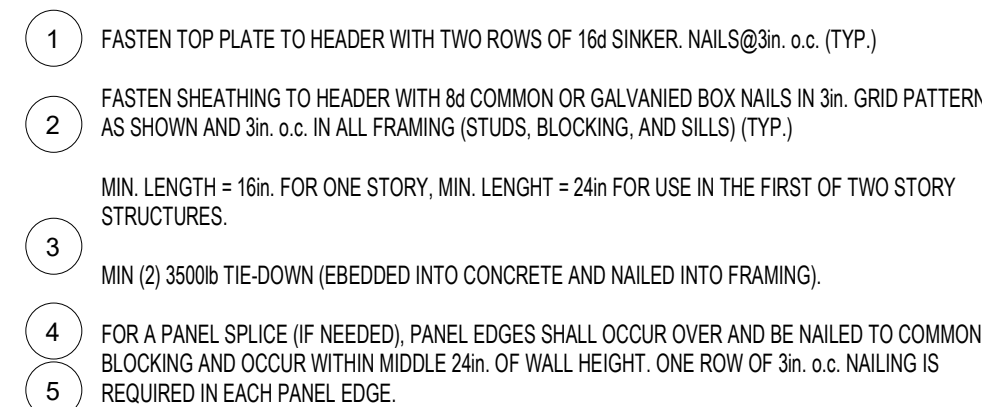

1 PORTAL FRAME HOLD-DOWN DETAIL
1/2" = 1'-0"

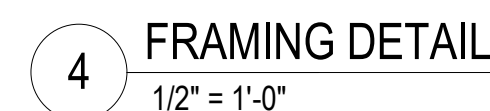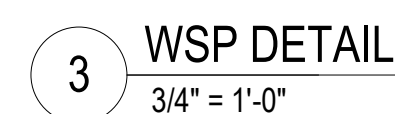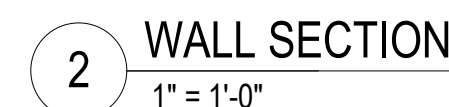

GENERAL CONDITIONS

DRAWINGS & SPECIFICATIONS

IT IS THE INTENT OF THE DRAWINGS AND SPECIFICATIONS TO BE GUIDELINES FOR CONSTRUCTION. THE CONTRACTOR IS RESPONSIBLE FOR DETERMINING ANY QUESTIONS OR MEANINGLESS DRAWINGS AND SPECIFICATIONS AND THE CONTRACTOR SHALL NOTIFY THE DESIGNER IN WRITING OF ANY ERRORS, OMISSIONS, OR UNSUITABLE DETAILING WHICH MAY CAUSE CONSTRUCTION PROBLEMS. THE DESIGNER'S LIABILITY REGARDING ERRORS AND/OR OMISSIONS WILL BE LIMITED TO THE CORRECTION OF THE ORIGINAL DRAWINGS. CONSULTANT'S LIABILITY IS THE SAME.



These Drawings contain confidential proprietary information and are the property of Risen Home Design. These drawings are NOT to be reproduced, copied whole or in part, disclosed, used for construction or any other purpose without prior written permission from Risen Home Design.



1 BUILDING
1/4" = 1'-0"



2 BUILDING
1/4" = 1'-0"

[illegible]

CUT SECTION VIEWS

RHD PROJECT NUMBER:		RHD-996	
DRAWN BY: MM		DATE: 10/5/2023	
CHECKED BY: -		DATE: 10/5/2023	
DRAWING NUMBER:			REV:
A7 1			1

NOTE: RISEN HOME DESIGN PLANS DO NOT CARRY AN ENGINEER'S AND/OR ARCHITECT'S STAMP(S) SOME CONDITIONS MAY ARISE DURING DESIGN, AND/OR CONSTRUCTION THAT MAY REQUIRE AN ARCHITECT'S AND/OR ENGINEER'S STAMP TO COMPLY WITH LOCAL BUILDING CODES. THE CONTRACTOR IS TO VERIFY THESE CONDITIONS AND SECURE REQUIRED STAMPS PRIOR TO CONSTRUCTION

DRAWINGS & SPECIFICATIONS

IT IS THE INTENT OF THE DRAWINGS AND SPECIFICATIONS TO BE GUIDELINES FOR CONSTRUCTION. THE CONTRACTOR IS RESPONSIBLE FOR DETERMINING ANY QUESTIONS AND MEANINGS IN THE WORKING DRAWINGS AND SPECIFICATIONS AND THE CONTRACTOR SHALL NOTIFY THE DESIGNER IN WRITING OF ANY ERRORS, OMISSIONS, OR UNSUITABLE DETAILING WHICH MAY CAUSE CONSTRUCTION PROBLEMS. THE DESIGNER'S LIABILITY REGARDING ERRORS AND/OR OMISSIONS WILL BE LIMITED TO THE CORRECTION OF THE ORIGINAL DRAWINGS. CONSULTANT'S LIABILITY IS THE SAME.