




RHD PROJECT NUMBER:		RHD-1169	
DRAWN BY: RMC		DATE: 7/10/2024	
CHECKED BY: MM		DATE: 7/10/2024	
DRAWING NUMBER:			REV:
A2.0			1

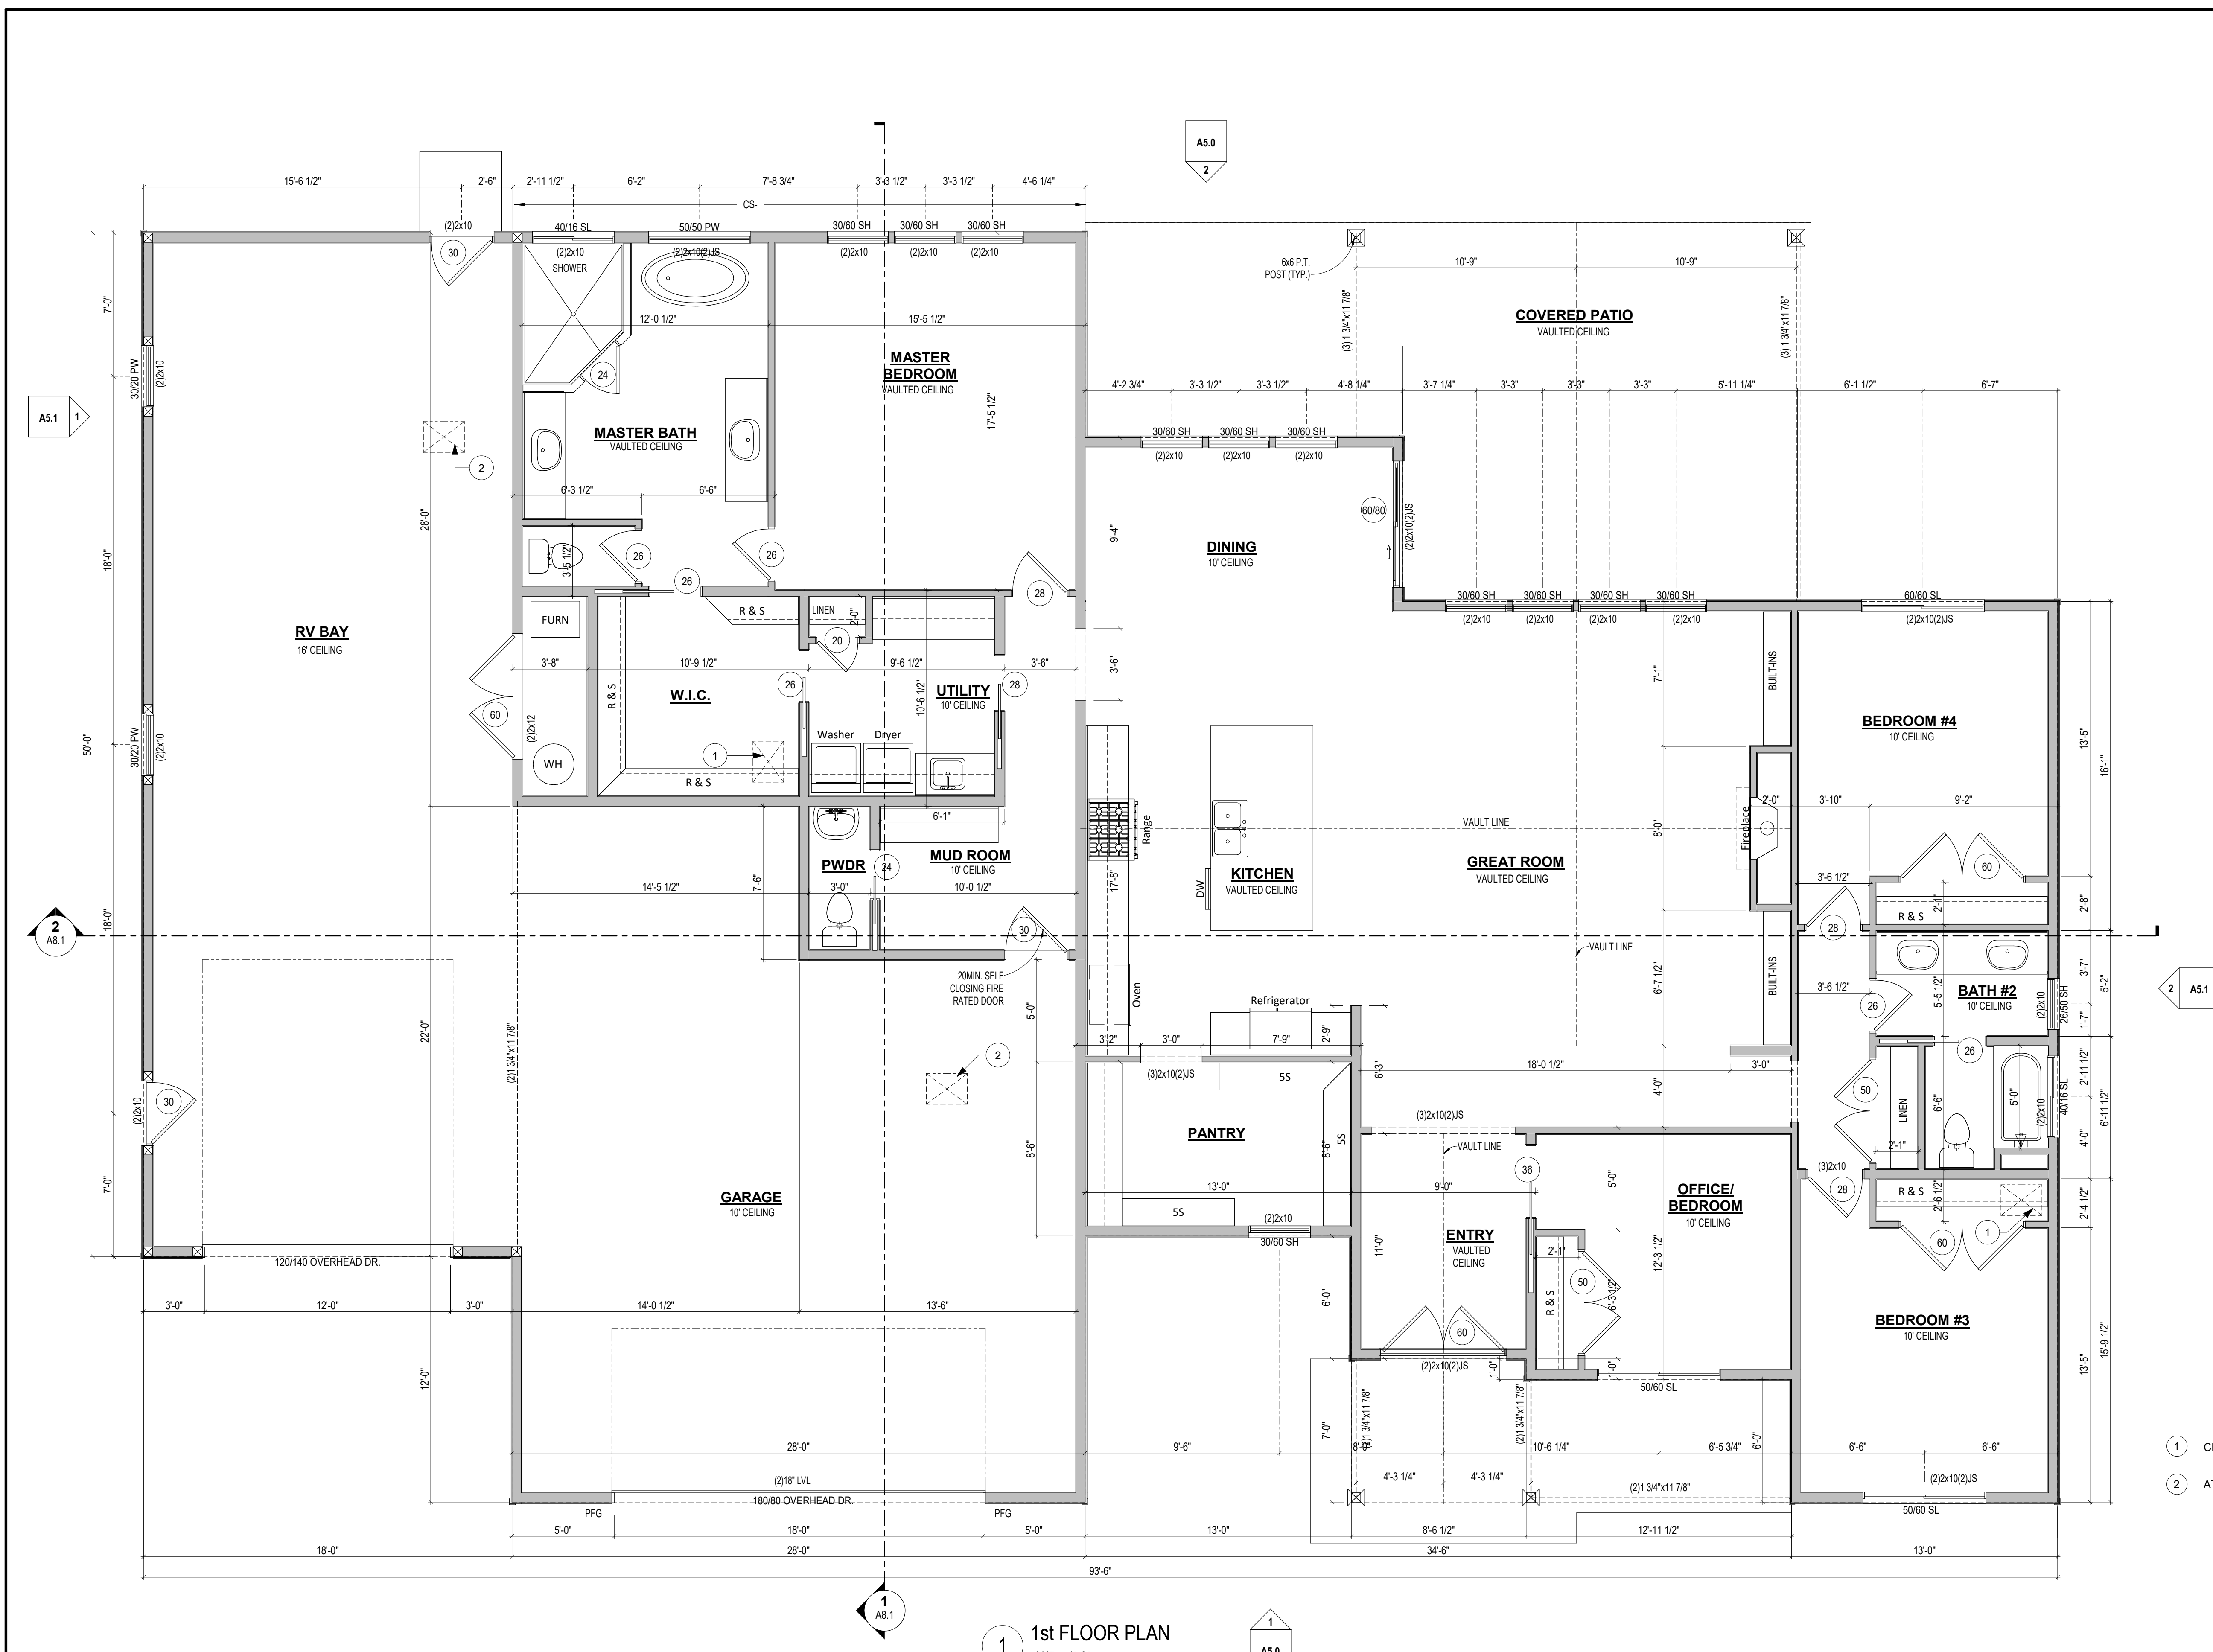

1 1st FLOOR PLAN
1/4" = 1'-0"

TABLE R402.1.1 INSULATION AND FENESTRATION REQUIREMENTS BY COMPONENT									
CLIMATE ZONE	FENESTRATION U-FACTOR	SKYLIGHT U-FACTOR	GLAZED FENESTRATION SHGC	CEILING R-VALUE	WOOD FRAM WALL R-VALUE	MASS WALL R-VALUE	FLOOR R-VALUE	BASEMENT WALL R-VALUE	SLAB R-VALUE
5 AND MARINE 4	0.35	0.60	NR	38	20 OR 13 ^{a5} ^h	13/17	30 ^g	10/13	10, 2 ft

NOTE: RISEN HOME DESIGN PLANS DO NOT CARRY AN ENGINEER'S AND/OR ARCHITECT'S STAMP(S) SOME CONDITIONS MAY ARISE DURING DESIGN, AND/OR CONSTRUCTION THAT MAY REQUIRE AN ARCHITECT'S AND/OR ENGINEER'S STAMP TO COMPLY WITH LOCAL BUILDING CODES. THE CONTRACTOR IS TO VERIFY THESE CONDITIONS AND SECURE REQUIRED STAMPS PRIOR TO CONSTRUCTION

DRAWINGS & SPECIFICATIONS	
R302.7	PROVIDE UNDERSTAIR PROTECTION AS REQUIRED
R302.11	PROVIDE FIREBLOCKING AS REQUIRED
R303.7	PROVIDE SWITCHING AND ILLUMINATION AS REQUIRED
R305	PROVIDE SUFFICIENT CEILING HEIGHTS
R311.7	MEET STAIRWAY REQUIREMENTS
R312	MEET GUARD REQUIREMENTS

FLOOR PLAN NOTES

- ALL STRUCTURAL LUMBER SIDED FOR #2 OR BETTER DOUG FIR LARCH
- 2x EXTERIOR STUD FRAMING @ 16" O.C. W/ SINGLE BOTTOM PLATE AND DOUBLE TOP PLATE
- 4x8 HEADERS IN ALL BEARING WALL OPENING UNLESS OTHERWISE NOTED
- ALLOW FOR A 22" x 30" (MIN) ATTIC AND CRAWL SPACE ACCESS
- ALL METAL CONNECTIONS TO BE SIMPSON CO. OR BETTER
- 5/8" TYPE 'X' GYP BOARD @ ALL GARAGE COMMON WALLS AND CEILINGS APPLIED TO GARAGE SIDE AND ALL WALLS, BEAMS, POSTS AND OTHER STRUCTURAL MEMBERS SUPPORTING FIRE PROTECTED HORIZONTAL STRUCTURAL MEMBERS
- DOORS BETWEEN GARAGE AND DWELLING ARE TO BE SELF CLOSING AND TIGHT FITTING SOLID WOOD DOOR 1 3/8" THICK OR A DOOR W/ A FIRE PROTECTION RATING OF NOT LESS THAN 20 MINUTES
- 1/2" GYPSUM BOARD TO BE INSTALLED ON INSIDE WALLS OF HOUSE
- ALL WINDOWS TO HAVE BREATHER TUBES INSTALLED
- ROOF SYSTEM TO BE PRE-ENGINEERED MANUFACTURED ROOF TRUSSES UNLESS OTHERWISE NOTED
- ALL CONSTRUCTION PRACTICES USED IN THE CONSTRUCTION OF THIS DWELLING SHALL BE DONE IN ACCORDANCE W/ THE 2018 WHERE APPLICABLE
- VENT RANGE HOOD, FANS, AND DRYER TO OUTSIDE AIR. CONTRACTOR TO VERIFY ALL CONDITIONS AND DIMENSIONS PRIOR TO COMMENCING WORK
- ALL RESCUE WINDOWS FROM SLEEPING AREAS MUST MEET THE FOLLOWING REQUIREMENTS:
 - SHALL HAVE A NET CLEAR OPENING OF 5.1 SQ. FT.
 - MINIMUM HEIGHT OF 24"
 - MINIMUM WIDTH OF 20"
 - FINISHED SILL HEIGHT OF NOT MORE THAN 44"
- EXTERIOR DIMENSIONS ARE TO FACE OF STUD WALL. INTERIOR DIMENSIONS ARE TO FACE OF STUD WALL
- ALL FURNACE SWITCHES, PILOTS, AND BURNERS TO BE MINIMUM 18" ABOVE FINISHED FLOOR

GENERAL NOTES

ALL EXTERIOR WALL SHALL BE SHEATHED W/7/16" OSB. ATTACH WITH MIN. 16 GA. X 1 3/4" LEG STAPLES AT 6" o.c. TO ALL SUPPORTED PANEL EDGES AND AT 6" o.c. IN THE FIELD. U.N.O.

STAPLES SHALL NOT BE SUBSTITUTED FOR COMMON NAILS AT SHEAR PANELS.

ALL SHEAR PANELS SHALL HAVE DOUBLE STUDS AT ENDS FOR EDGE NAILING AND ATTACHMENT OF STRAPS AND/OR HOLD DOWNS, TYP.

ALL HOLD DOWNS SHALL ALIGN AT DOUBLE STUDS AT ENDS OF SHEAR PANELS, TYP.

PROVIDE 'SIMPSON' H1 AT ALL TRUSS BEARING LOCATIONS.

ALL SHEATHING SHALL BE CONTINUOUS TO FLOOR/PLATE BEHIND ALL ATTACHED ROOF FRAMING INTO WALL.

PROVIDE DOUBLE STUD ABOVE AND BELOW ALIGNED AT STRAPS BETWEEN FLOORS FOR STRAP ATTACHMENT. WITH PANEL EDGE NAILING FOR FULL HEIGHT OF DOUBLE STUD.

PROVIDE GALVANIZED NAILS INTO PRESERVATION TREATED SILL PLATES. NAIL SIZE AND SPACING TO MATCH SHEAR WALL SPECIFIED. PROVIDE 6d GALVANIZED NAILS AT SAME SPACING WHERE STAPLES USED.

AT MINIMUM, PROVIDE REINFORCING BARS IN FOUNDATION AT HOLD DOWN LOCATIONS PER MANUFACTURERS REQUIREMENTS

SQ/FT.	
LIVING	2764 SF
GARAGE	841 SF
RV BAY	939 SF
FRONT PORCH	138 SF
BACK PATIO	505 SF
INTERIOR WALL-LIVING	2638 SF

DOOR/WINDOW TAG EXAMPLE

DOOR TAG	WINDOW TAG
28 = 2'-6"	40/56 SH = 4'-0" x 5'-6" SINGLE HUNG

SHEET NOTES

- CRAWL SPACE ACCESS. COORDINATE WITH JOIST LAYOUT.
- ATTIC SPACE ACCESS. COORDINATE WITH TRUSS LAYOUT.

NOTE: VERIFY ALL WINDOW/DOOR ROUGH OPENING AND HEADER HEIGHT AND THE SAME FOR TRIM PACKAGE. VERIFY STANDARD HEIGHTS WITH CONTRACTOR BEFORE FRAMING.

SEE 2018 IRC

R302.7 PROVIDE UNDERSTAIR PROTECTION AS REQUIRED

R302.11 PROVIDE FIREBLOCKING AS REQUIRED

R303.7 PROVIDE SWITCHING AND ILLUMINATION AS REQUIRED

R305 PROVIDE SUFFICIENT CEILING HEIGHTS

R311.7 MEET STAIRWAY REQUIREMENTS

R312 MEET GUARD REQUIREMENTS

GENERAL CONDITIONS



WHITESTONE
LOT#7 BLK#2 RIVERWALK CROSSING
MIDDLETON, ID
1st FLOOR PLAN

BLACKSTONE HOMES

These Drawings contain confidential proprietary information and are the property of Risen Home Design. These drawings are NOT to be reproduced, copied whole or in part, disclosed, used for construction or any other purpose without prior written permission from Risen Home Design.

REVISIONS	
NO.	DATE
A	7/4/2024
0	7/10/2024

RHD PROJECT NUMBER: RHD-1169

DRAWN BY: MM DATE: 7/4/2024

CHECKED BY: - DATE: 7/4/2024

DRAWING NUMBER: A3.0 REV: 0




BLACKSTONE
HOMES

These Drawings contain confidential proprietary information and are the property of Risen Home Design. These drawings are NOT to be reproduced, copied whole or in part, disclosed, used for construction or any other purpose without prior written permission from Risen Home Design.

[illegible]

**SHEAR WALL
PLAN**

REV:

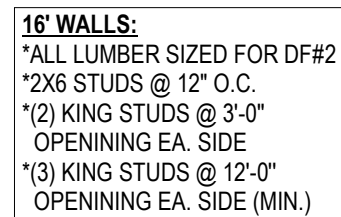

(1

TABLE 1: HOLD DOWN (HD) SCHEDULE
(FIRST FLOOR WOOD SHEAR WALL TO CONCRETE FOUNDATION)

SHEAR WALL SCHEDULE: INDIVIDUAL FULL HEIGHT WALL SEGMENTS

BRACING DETAILS

METHOD	MATERIAL	CONNECTION CRITERIA
WSP	WOOD STRUCTURAL PANEL (SEE SECTION R604)	EXTERIOR SHEATHING: SEE IRC TABLE R602(3) INTERIOR SHEATHING: SEE IRC TABLE R602(3)1
CPG	INTERMITTENT PORTAL FRAME	SEE SECTION R602.10.4.1.1
ULB	LET-IN BRACING	1x4 WOOD OR APPROVED METAL STRAPS AT 45d TO 60d ANGLES FOR MAXIMUM 16" SPACING

GENERAL CONDITIONS

DRAWINGS & SPECIFICATIONS



IT IS THE INTENT OF THE DRAWINGS AND SPECIFICATIONS TO BE GUIDELINES FOR CONSTRUCTION. THE CONTRACTOR IS RESPONSIBLE FOR DETERMINING ANY QUESTIONS AND MEANINGS IN THE WORKING DRAWINGS AND SPECIFICATIONS AND THE CONTRACTOR SHALL NOTIFY THE DESIGNER IN WRITING OF ANY ERRORS, OMISSIONS, OR UNSUITABLE DETAILING WHICH MAY CAUSE CONSTRUCTION PROBLEMS. THE DESIGNER'S LIABILITY REGARDING ERRORS AND/OR OMISSIONS WILL BE LIMITED TO THE CORRECTION OF THE ORIGINAL DRAWINGS. CONSULTANT'S LIABILITY IS THE SAME.

NOTE: RISEN HOME DESIGN PLANS DO NOT CARRY AN ENGINEER'S AND/OR ARCHITECT'S STAMP(S) SOME CONDITIONS MAY ARISE DURING DESIGN. AND/OR CONSTRUCTION THAT MAY REQUIRE AN ARCHITECT'S AND/OR ENGINEER'S STAMP TO COMPLY WITH LOCAL BUILDING CODES. THE CONTRACTOR IS TO VERIFY THESE CONDITIONS AND SECURE REQUIRED STAMPS PRIOR TO CONSTRUCTION



RISEN
Home Design

390 E CORPORATE DR. STE 112
MERIDIAN, ID 83642
#208-283-3775

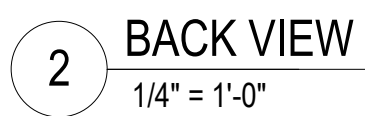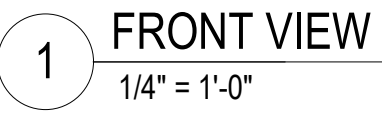


GENERAL CONDITIONS


<u>DRAWINGS & SPECIFICATIONS</u> IT IS THE INTENT OF THE DRAWINGS AND SPECIFICATIONS TO BE GUIDELINES FOR CONSTRUCTION. THE CONTRACTOR IS RESPONSIBLE FOR DETERMINING ANY QUESTIONS AND MEANINGS IN THE WORKING DRAWINGS AND SPECIFICATIONS AND THE CONTRACTOR SHALL NOTIFY THE DESIGNER IN WRITING OF ANY ERRORS, OMISSIONS, OR UNSUITABLE DETAILING WHICH MAY CAUSE CONSTRUCTION PROBLEMS. THE DESIGNER'S LIABILITY REGARDING ERRORS AND/OR OMISSIONS WILL BE LIMITED TO THE CORRECTION OF THE ORIGINAL DRAWINGS. CONSULTANT'S LIABILITY IS THE SAME.
--

[illegible]

SHEET TITLE ELEVATIONS	
RHD PROJECT NUMBER:	RHD-1169
DRAWN BY: MM	DATE: 7/4/2024
CHECKED BY: -	DATE: 7/4/2024
DRAWING NUMBER:	REV:
A5.0	0

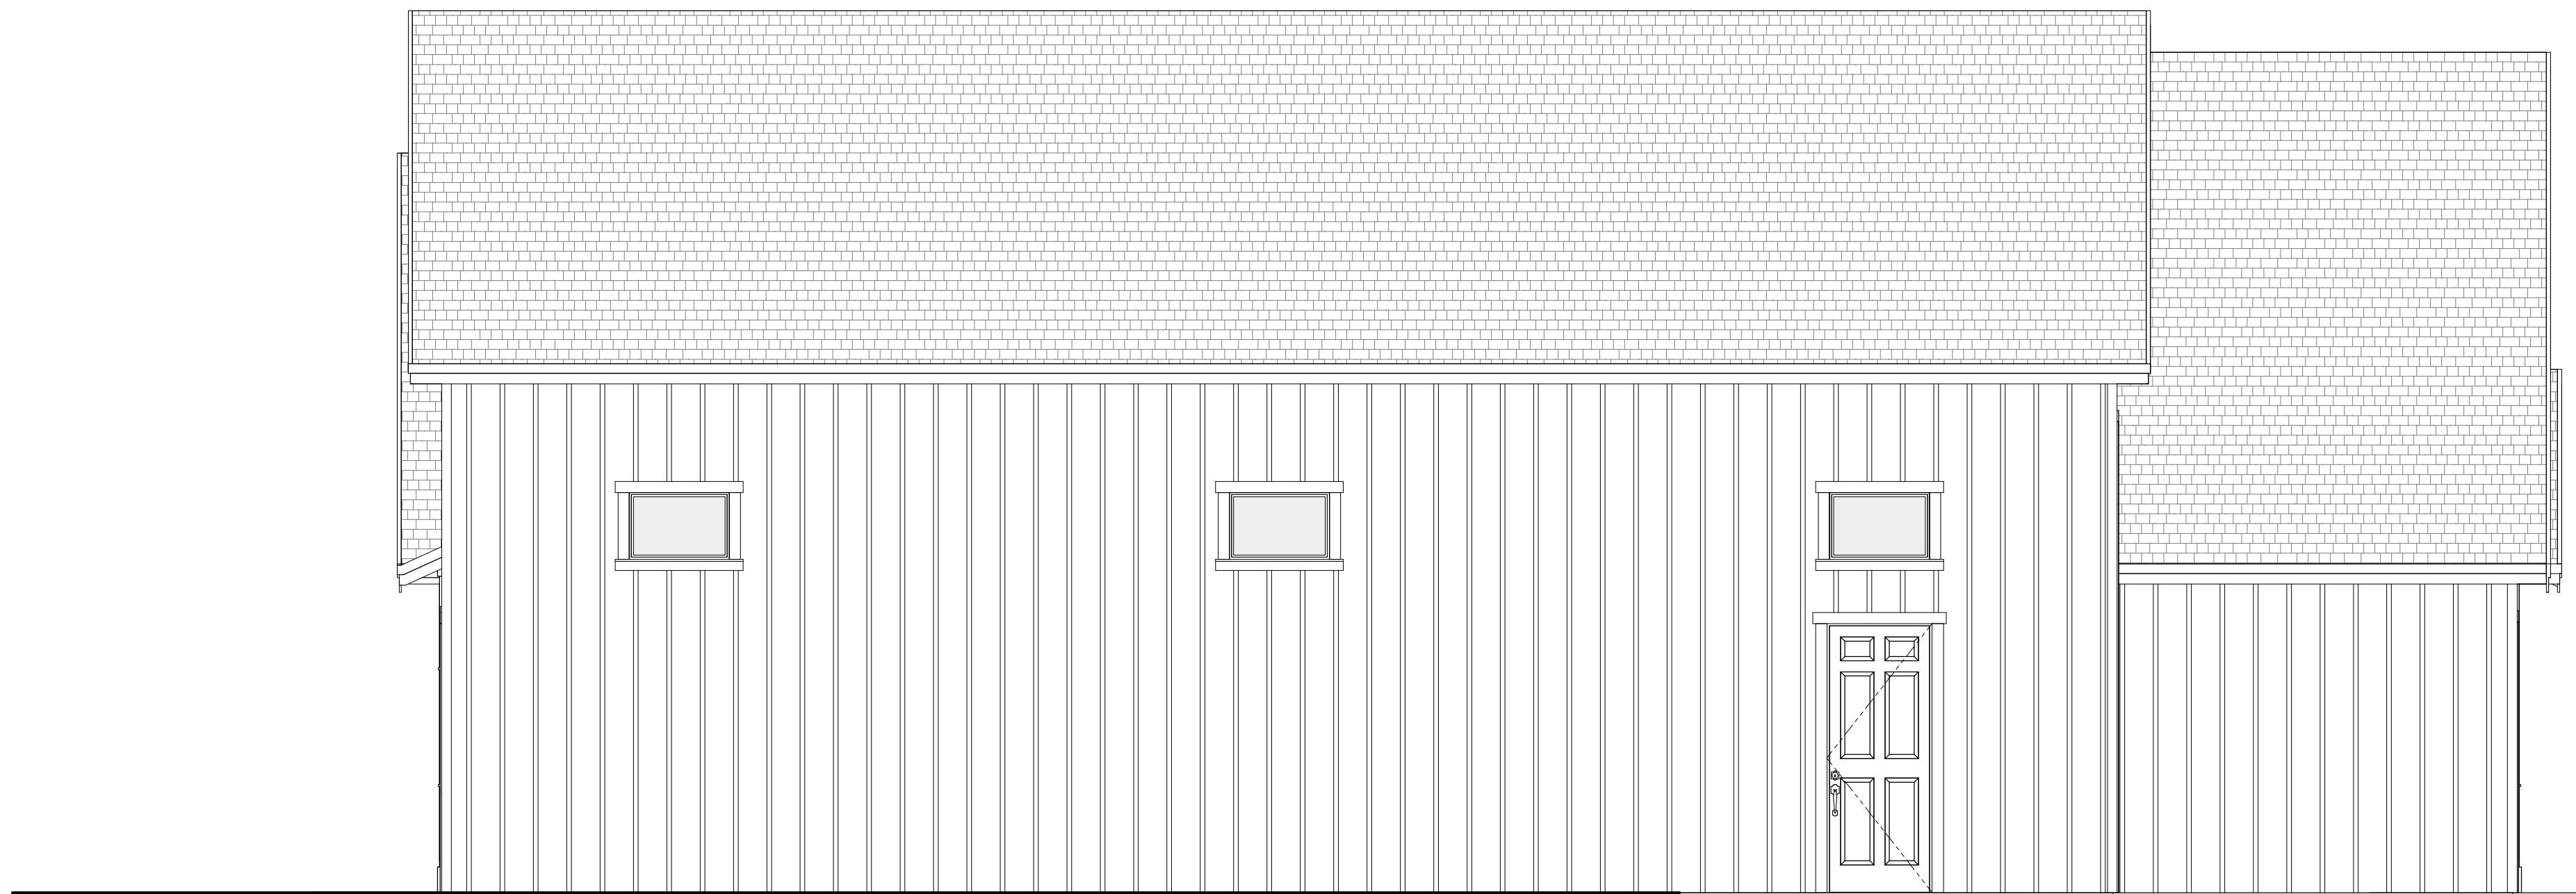

1 LEFT VIEW
1/4" = 1'-0"

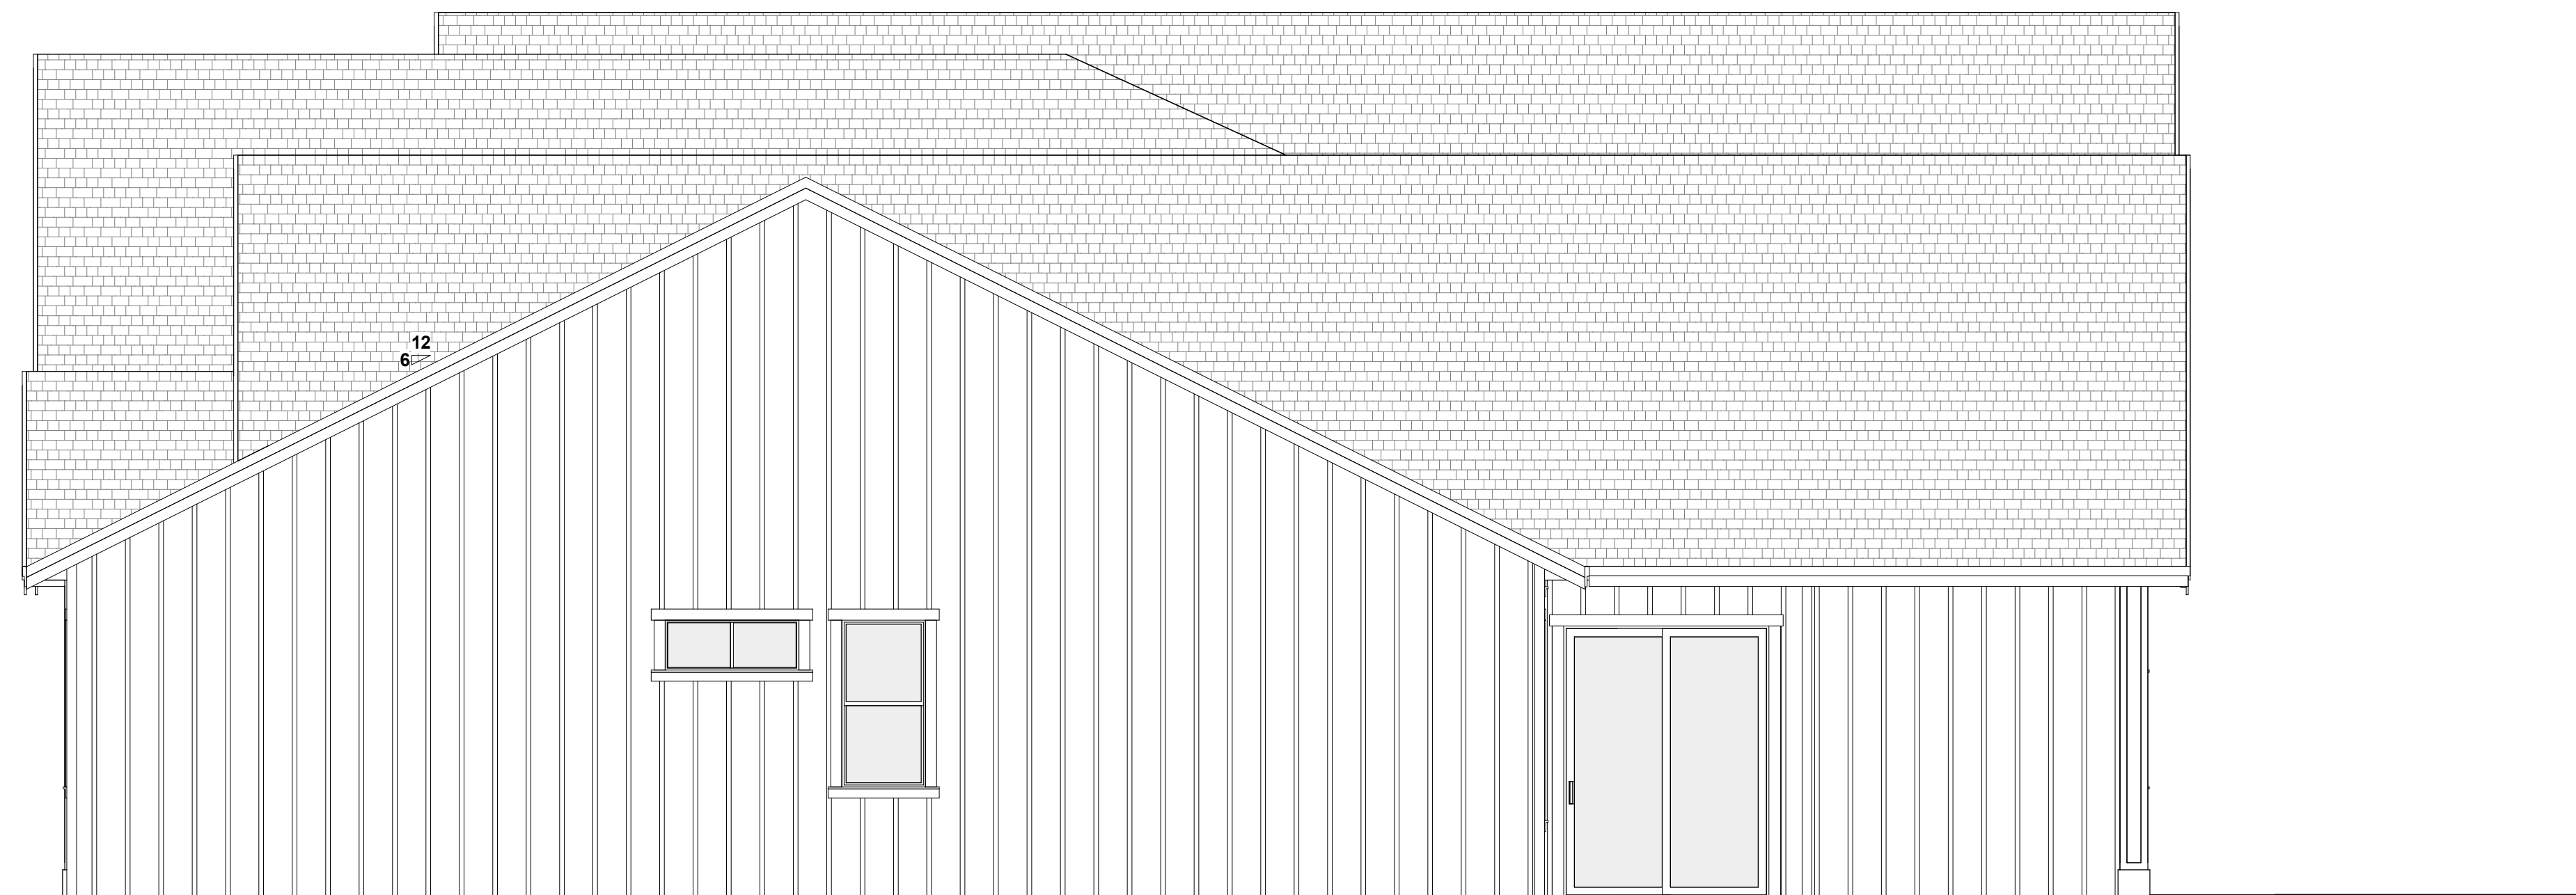

2 RIGHT VIEW
1/4" = 1'-0"

NOTE: RISEN HOME DESIGN PLANS DO NOT CARRY AN ENGINEER'S AND/OR ARCHITECT'S STAMP(S) SOME CONDITIONS MAY ARISE DURING DESIGN, AND/OR CONSTRUCTION THAT MAY REQUIRE AN ARCHITECT'S AND/OR ENGINEER'S STAMP TO COMPLY WITH LOCAL BUILDING CODES. THE CONTRACTOR IS TO VERIFY THESE CONDITIONS AND SECURE REQUIRED STAMPS PRIOR TO CONSTRUCTION

DRAWINGS & SPECIFICATIONS
IT IS THE INTENT OF THE DRAWINGS AND SPECIFICATIONS TO BE GUIDELINES FOR CONSTRUCTION. THE CONTRACTOR IS RESPONSIBLE FOR DETERMINING ANY QUESTIONS AND MEANINGS IN THE WORKING DRAWINGS AND SPECIFICATIONS AND THE CONTRACTOR SHALL NOTIFY THE DESIGNER IN WRITING OF ANY ERRORS, OMISSIONS, OR UNSUITABLE DETAILING WHICH MAY CAUSE CONSTRUCTION PROBLEMS. THE DESIGNER'S LIABILITY REGARDING ERRORS AND/OR OMISSIONS WILL BE LIMITED TO THE CORRECTION OF THE ORIGINAL DRAWINGS. CONSULTANT'S LIABILITY IS THE SAME.



WHITESTONE
LOT#7 BLK#2 RIVERWALK CROSSING
MIDDLETON, ID
ELEVATIONS

3


BLACKSTONE

HOUSES


These Drawings contain confidential proprietary information and are the property of Risen Home Design. These drawings are NOT to be reproduced, copied whole or in part, disclosed, used for construction or any other purpose without prior written permission from Risen Home Design.

REVISIONS	
NO.	DESCRIPTION
1	DATE
2	7/4/2024
3	7/10/2024
4	
5	
6	
7	
8	
9	
10	
11	
12	
13	
14	
15	
16	
17	
18	
19	
20	


SHEET TITLE	
ELEVATIONS	
RHD PROJECT NUMBER: RHD-1169	
DRAWN BY: MM	DATE: 7/4/2024
CHECKED BY: -	DATE: 7/4/2024
DRAWING NUMBER: A5.1	REV: 0

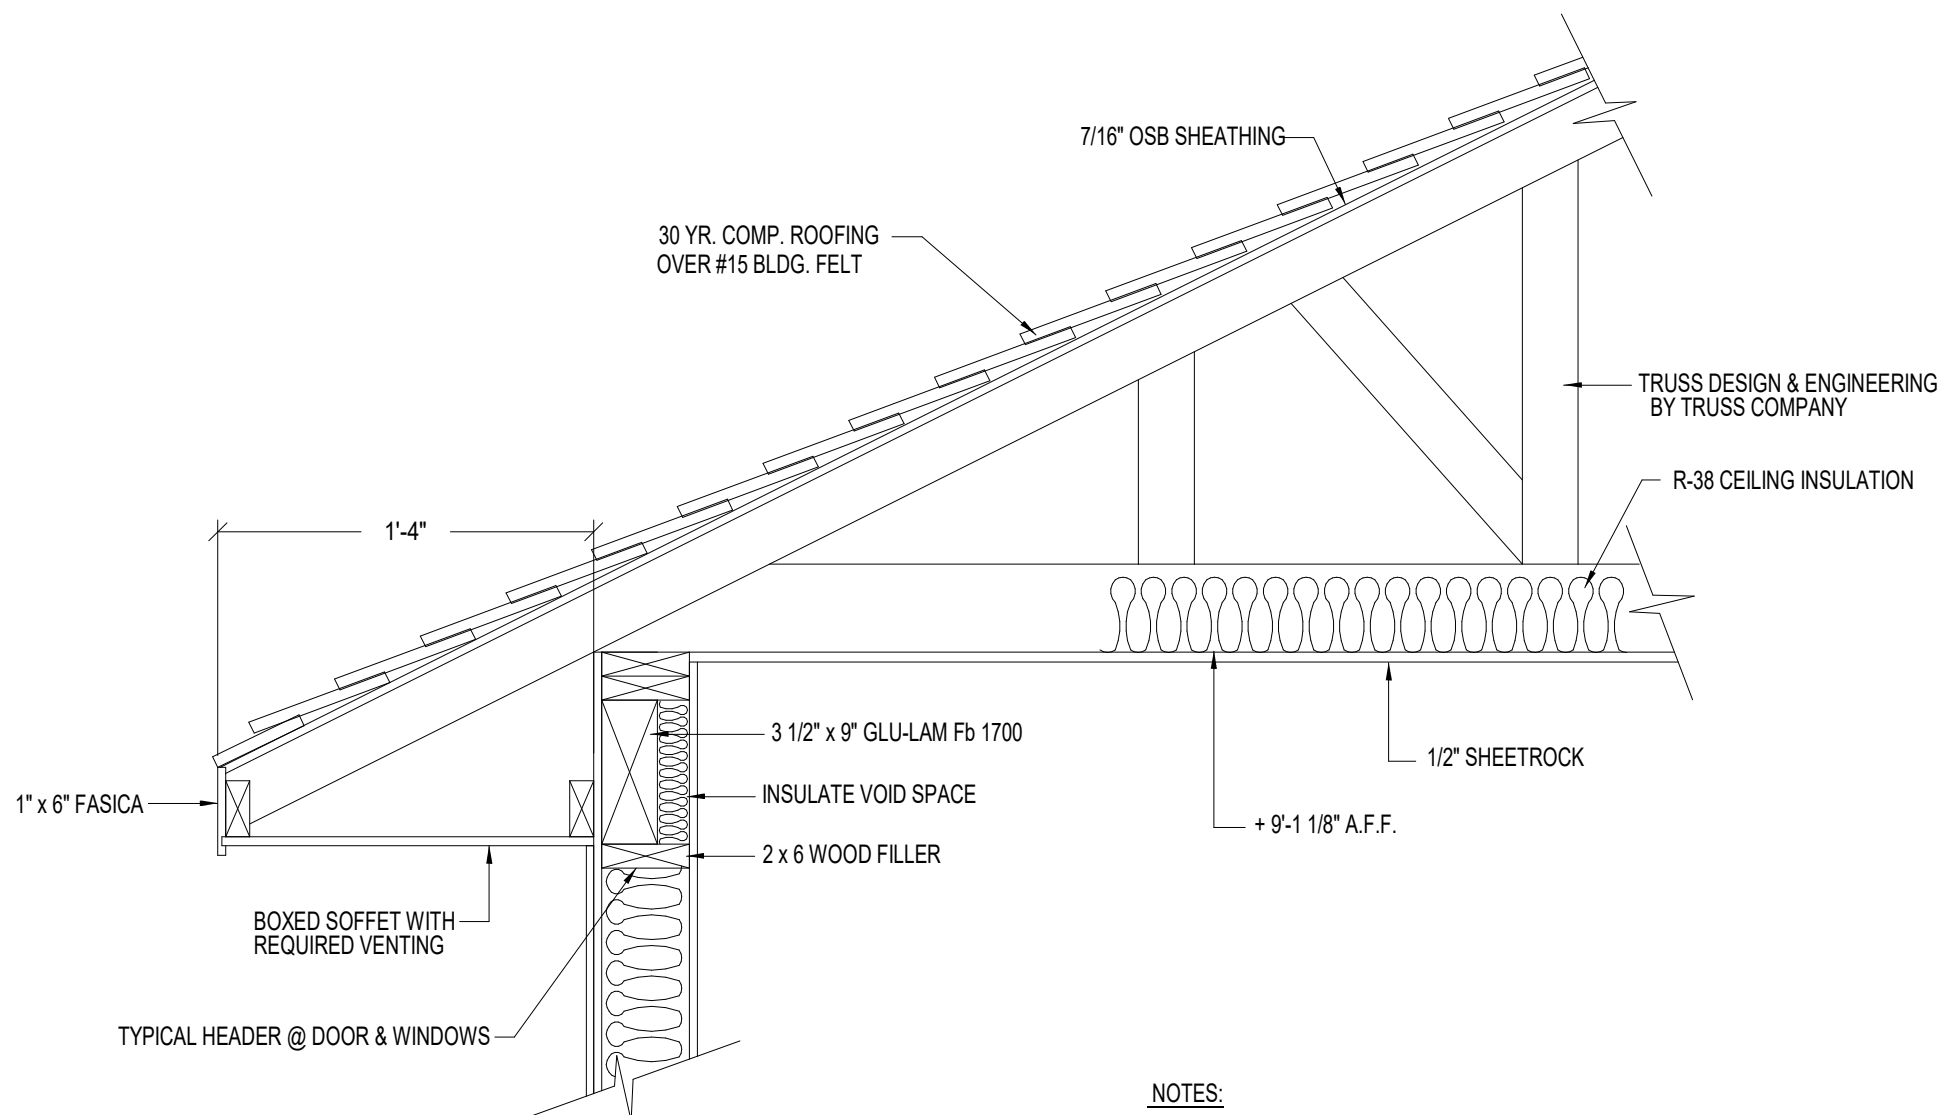


- NOTES:
- 1 X= 6" OR 8" MIN. AS REQUIRED PER LOCAL BUILDING CODE.
 - 2 SUGGESTED REBAR PLACEMENT TO BE: 2-#4 REBAR IN FOOTING AND VERTICAL #4 REBAR @ 4' O.C. IN ALL 2' EXTERIOR CONCRETE STEM WALLS. REFERENCE FOUNDATION PLAN A3.0 FOR COUNTY REQUIREMENTS AND NOTES.
 - 3 SPECIAL REBAR PLACEMENT TO BE: 2-#4 REBAR IN FOOTING AND 2-#4 HORIZ. REBAR IN STEM WALL EQUALLY SPACED AND VERTICAL #4 REBAR @ 4' O.C. IN ALL 2' EXTERIOR CONCRETE STEM WALLS. REFERENCE FOUNDATION PLAN A3.0 FOR COUNTY REQUIREMENTS AND NOTES.

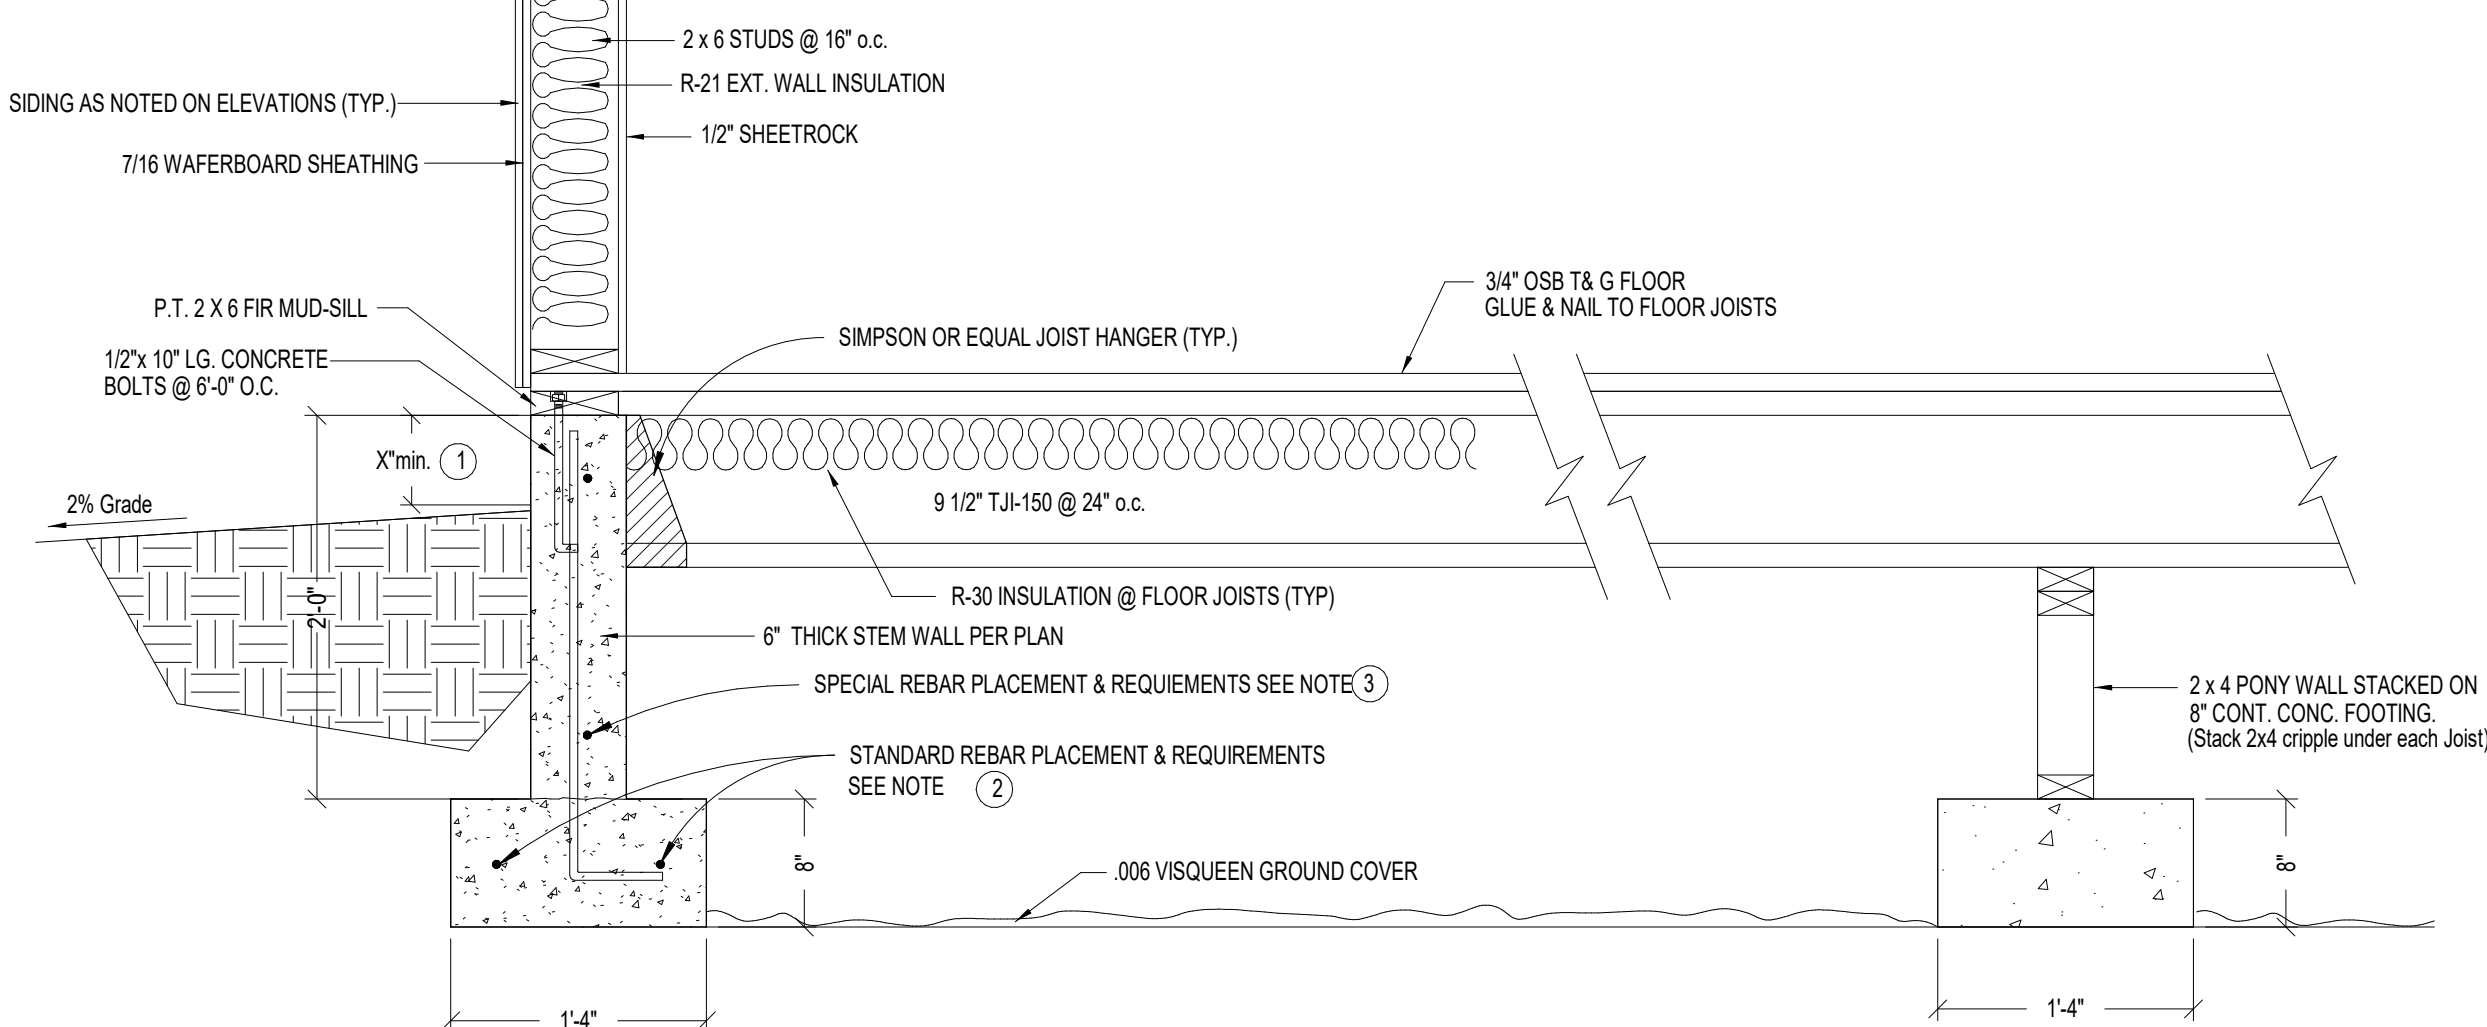


1 WALL SECTION
1" = 1'-0"

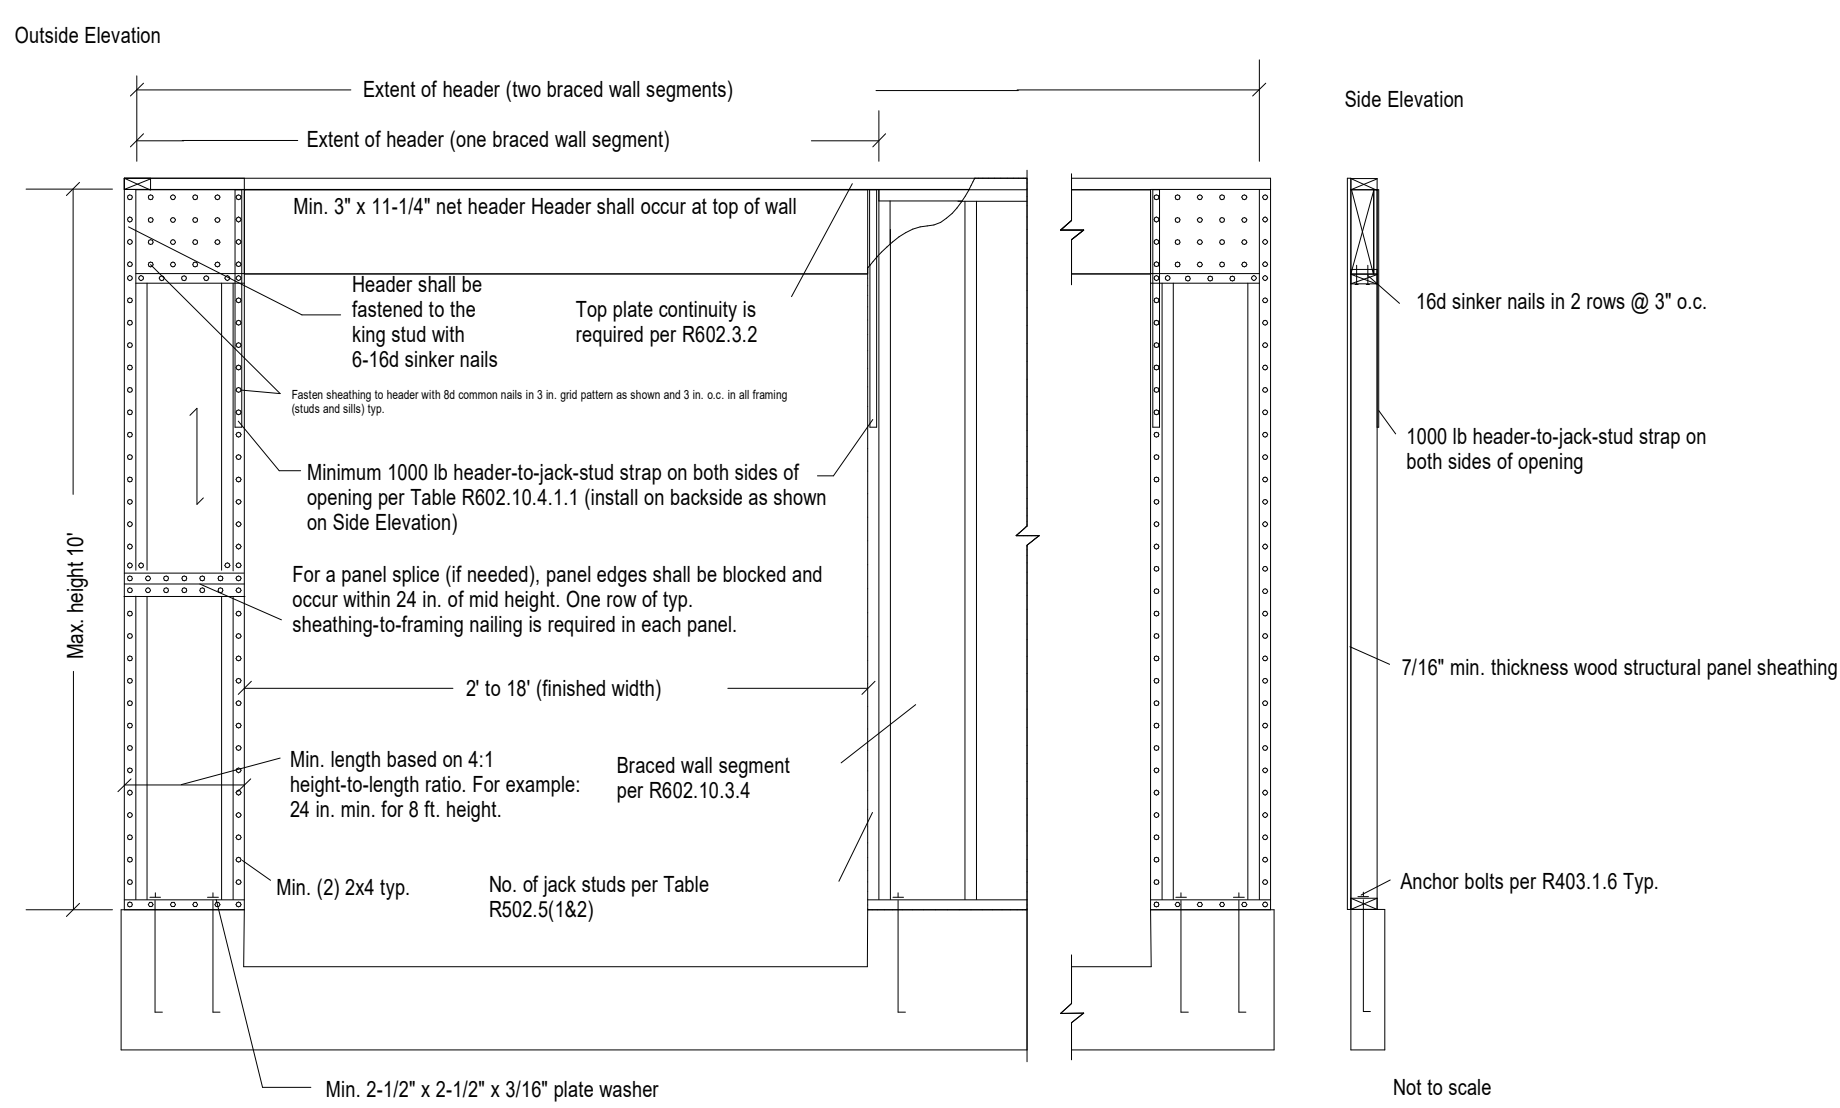


4 PFG DETAIL
1/2" = 1'-0"

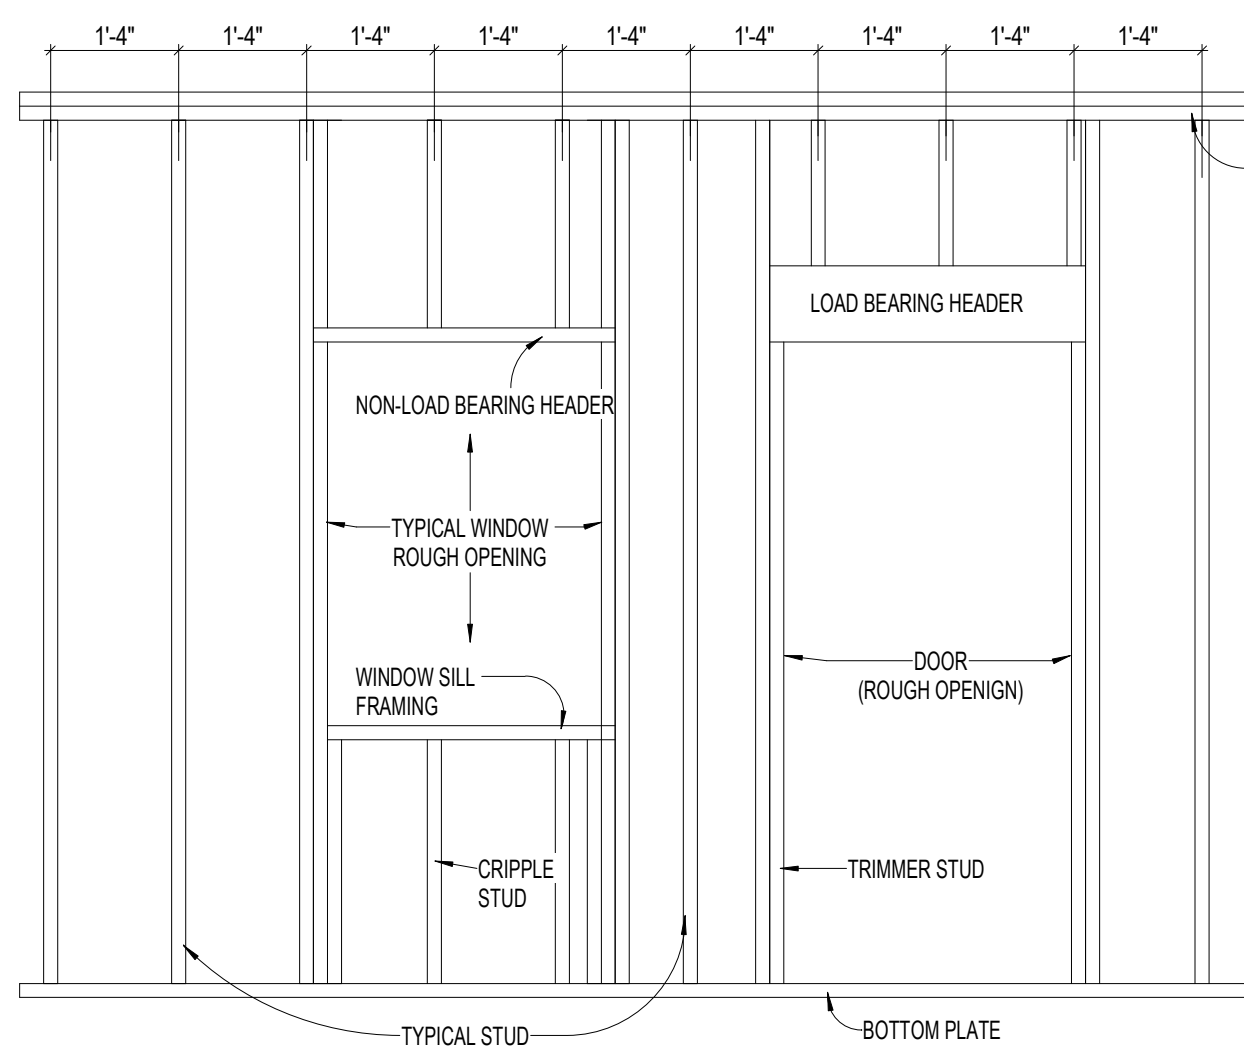


2 FRAMING DETAIL
1/2" = 1'-0"

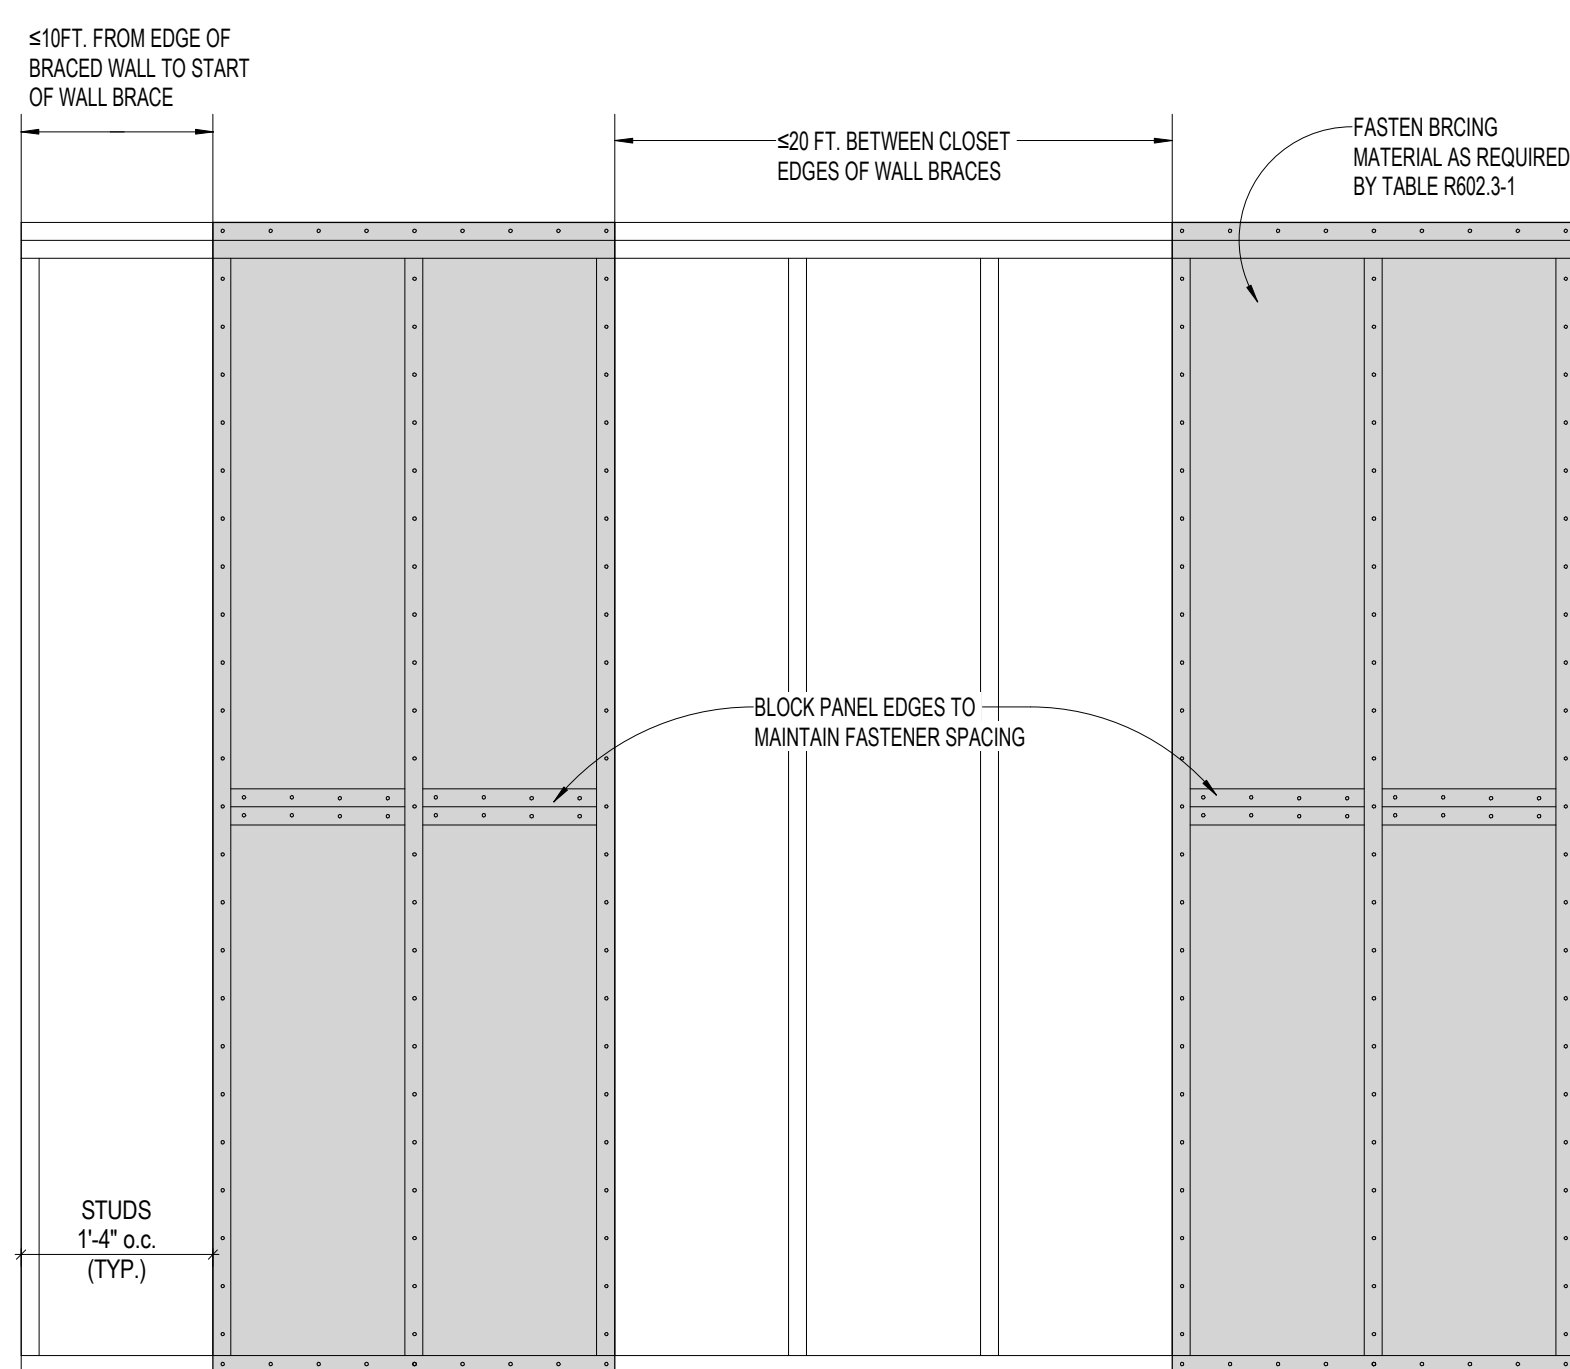

5 WSP DETAIL
3/4" = 1'-0"

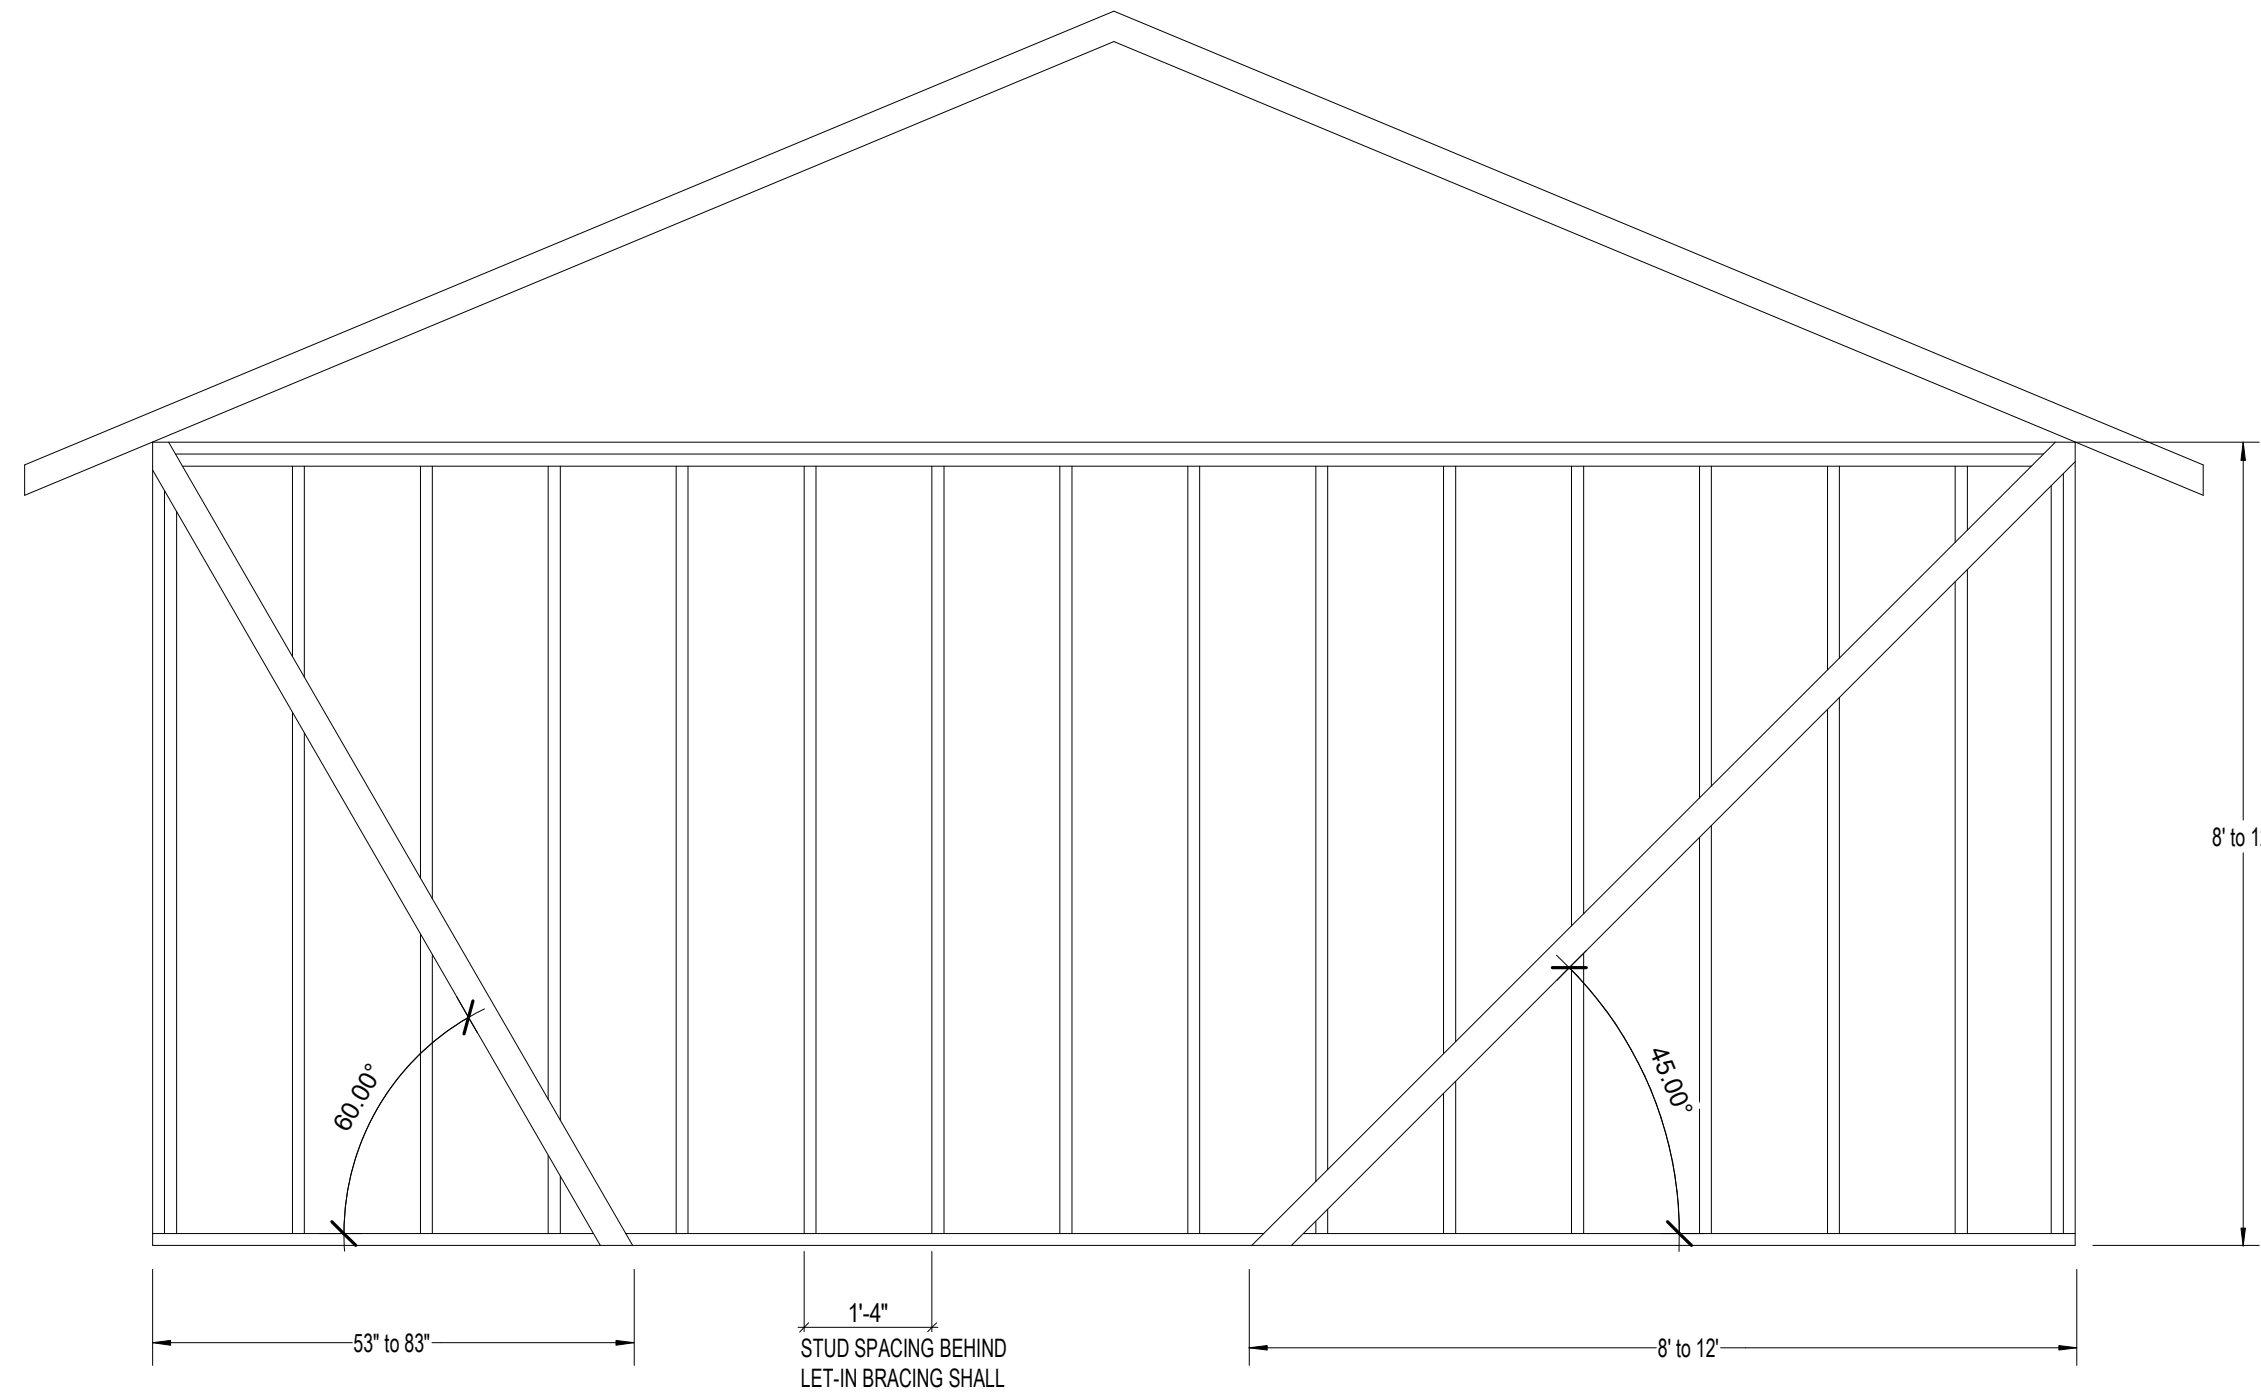

3 LIB DETAIL
1/2" = 1'-0"

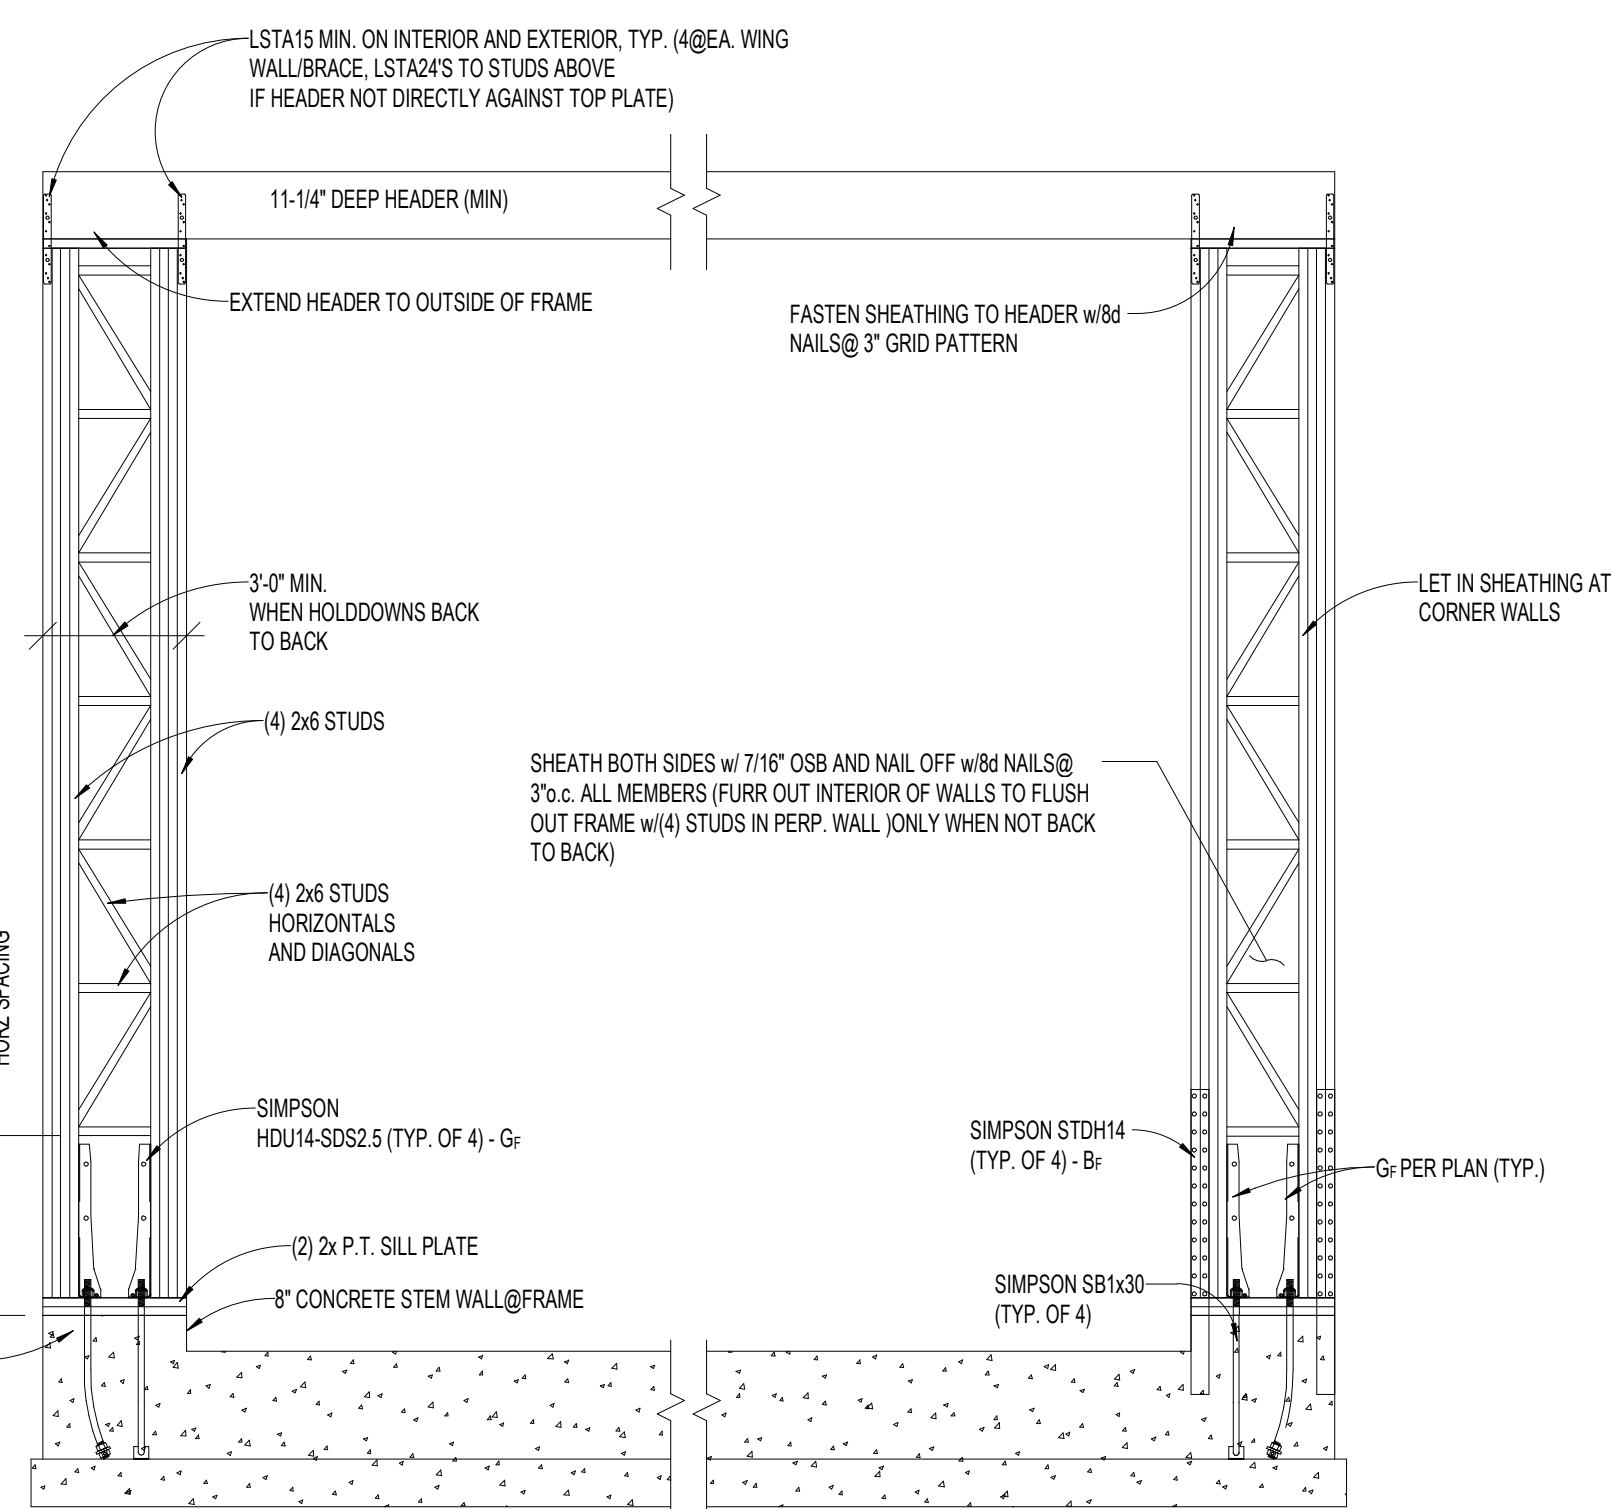

6 PORTAL FRAME DETAIL
3/8" = 1'-0"

NOTE: RISEN HOME DESIGN PLANS DO NOT CARRY AN ENGINEER'S AND/OR ARCHITECT'S STAMP(S) SOME CONDITIONS MAY ARISE DURING DESIGN, AND/OR CONSTRUCTION THAT MAY REQUIRE AN ARCHITECT'S AND/OR ENGINEER'S STAMP TO COMPLY WITH LOCAL BUILDING CODES. THE CONTRACTOR IS TO VERIFY THESE CONDITIONS AND SECURE REQUIRED STAMPS PRIOR TO CONSTRUCTION

DRAWINGS & SPECIFICATIONS	
GENERAL CONDITIONS	
IT IS THE INTENT OF THE DRAWINGS AND SPECIFICATIONS TO BE GUIDELINES FOR CONSTRUCTION. THE CONTRACTOR IS RESPONSIBLE FOR DETERMINING ANY QUESTIONS AND MEANINGS IN THE WORKING DRAWINGS AND SPECIFICATIONS AND THE CONTRACTOR SHALL NOTIFY THE DESIGNER IN WRITING OF ANY ERRORS, OMISSIONS, OR UNSUITABLE DETAILING WHICH MAY CAUSE CONSTRUCTION PROBLEMS. THE DESIGNER'S LIABILITY REGARDING ERRORS AND/OR OMISSIONS WILL BE LIMITED TO THE CORRECTION OF THE ORIGINAL DRAWINGS. CONSULTANT'S LIABILITY IS THE SAME.	




WHITESTONE
LOT#7 BLK#2 RIVERWALK CROSSING
MIDDLETON, ID
DETAILS

These Drawings contain confidential proprietary information and are the property of Risen Home Design. These drawings are NOT to be reproduced, copied whole or in part, disclosed, used for construction or any other purpose without prior written permission from Risen Home Design.




REVISIONS	
NO.	DESCRIPTION
0	ISSUE FOR CONSTRUCTION
1	ISSUE FOR CONSTRUCTION

SHEET TITLE	
DETAILS	
RHD PROJECT NUMBER: RHD-1169	
DRAWN BY: RMC	DATE: 7/10/2024
CHECKED BY: MM	DATE: 7/10/2024
DRAWING NUMBER: A8.0	REV: 1

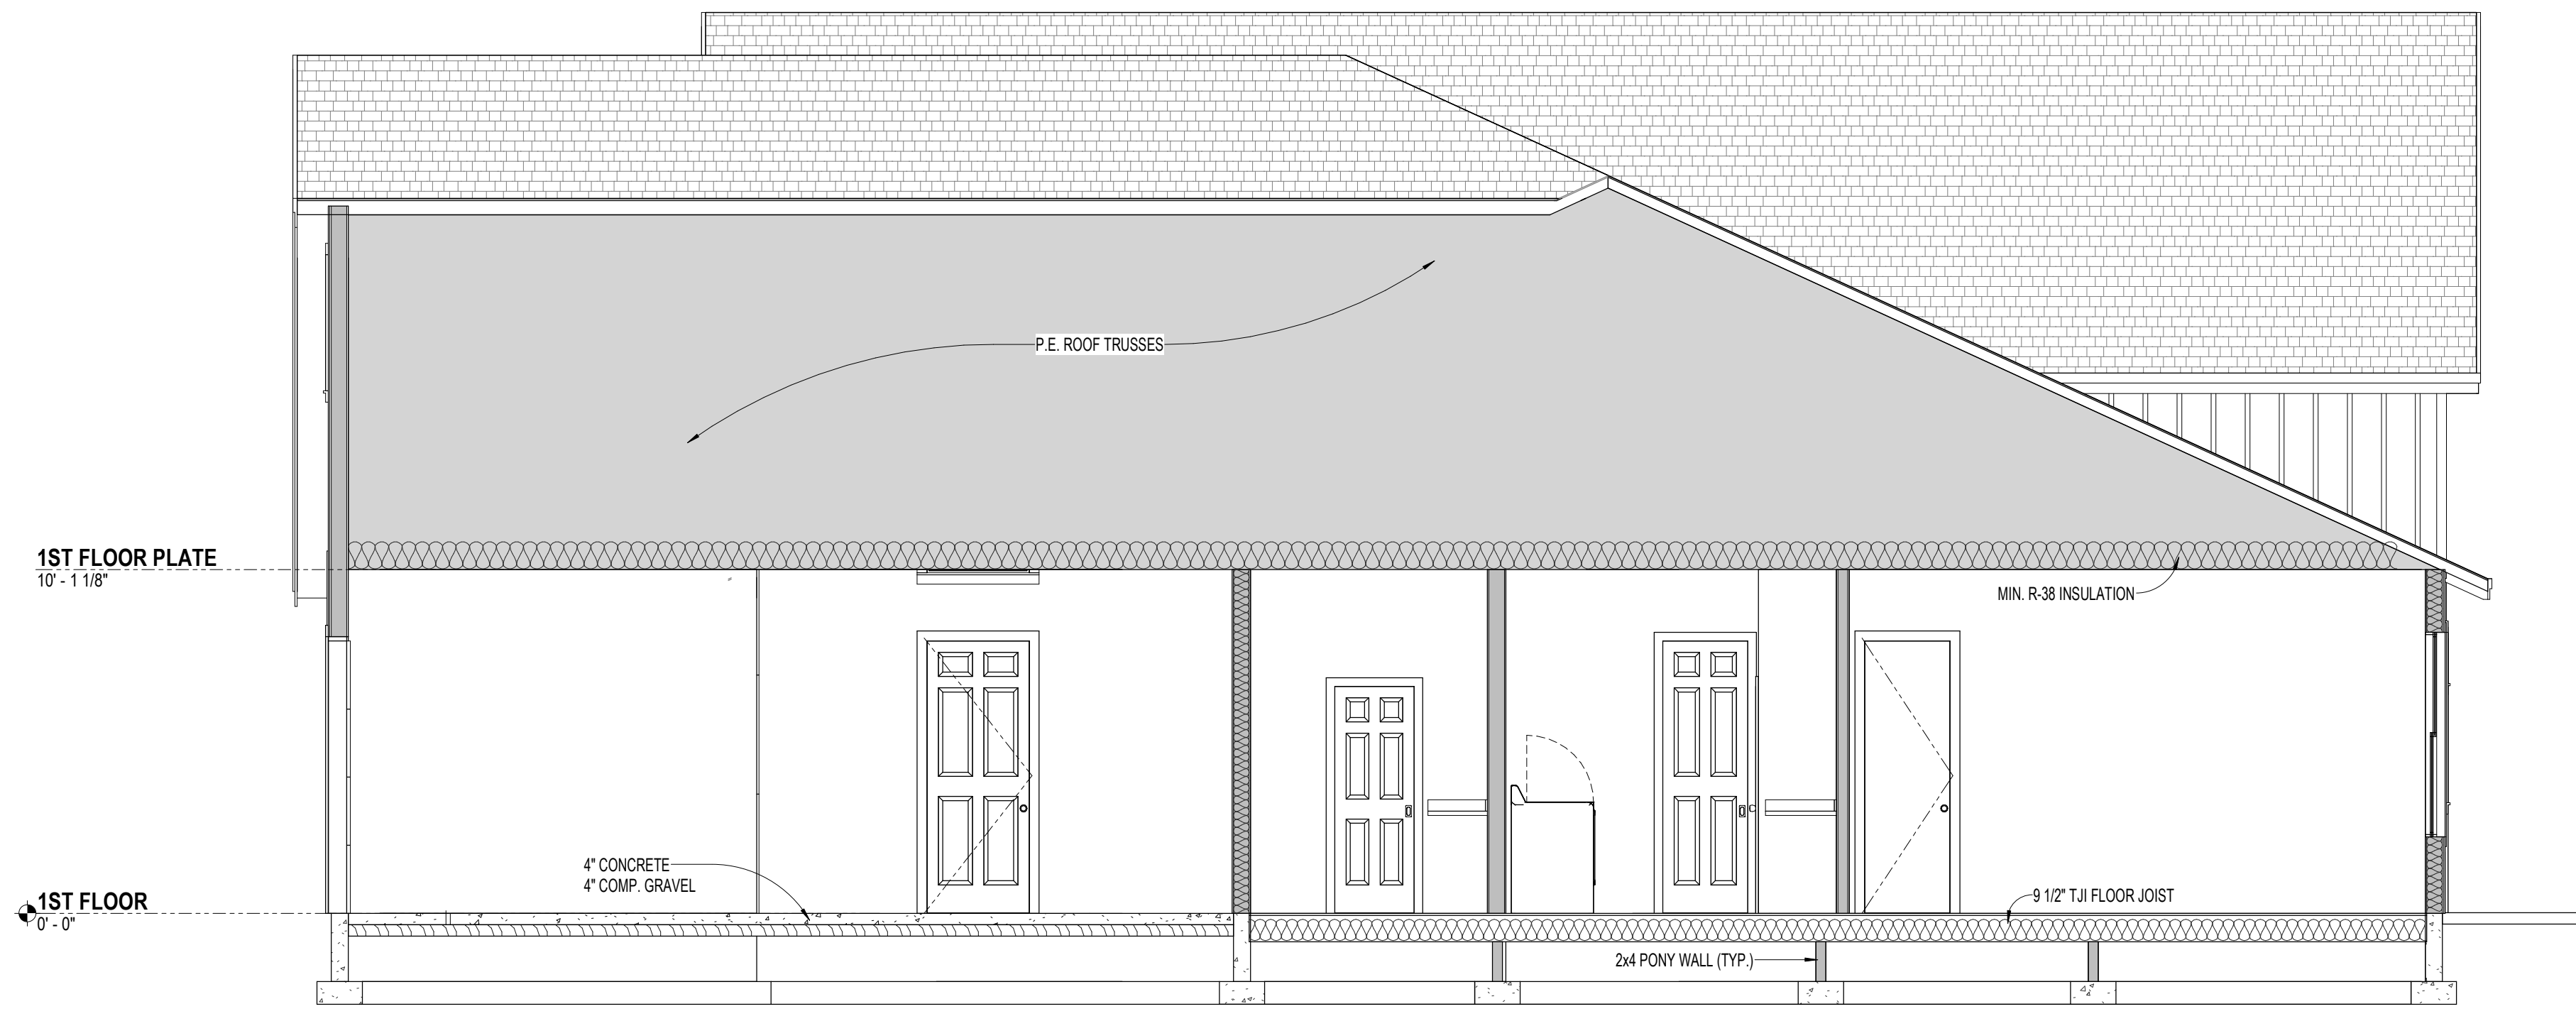

1 BUILDING SECTION-1
1/4" = 1'-0"

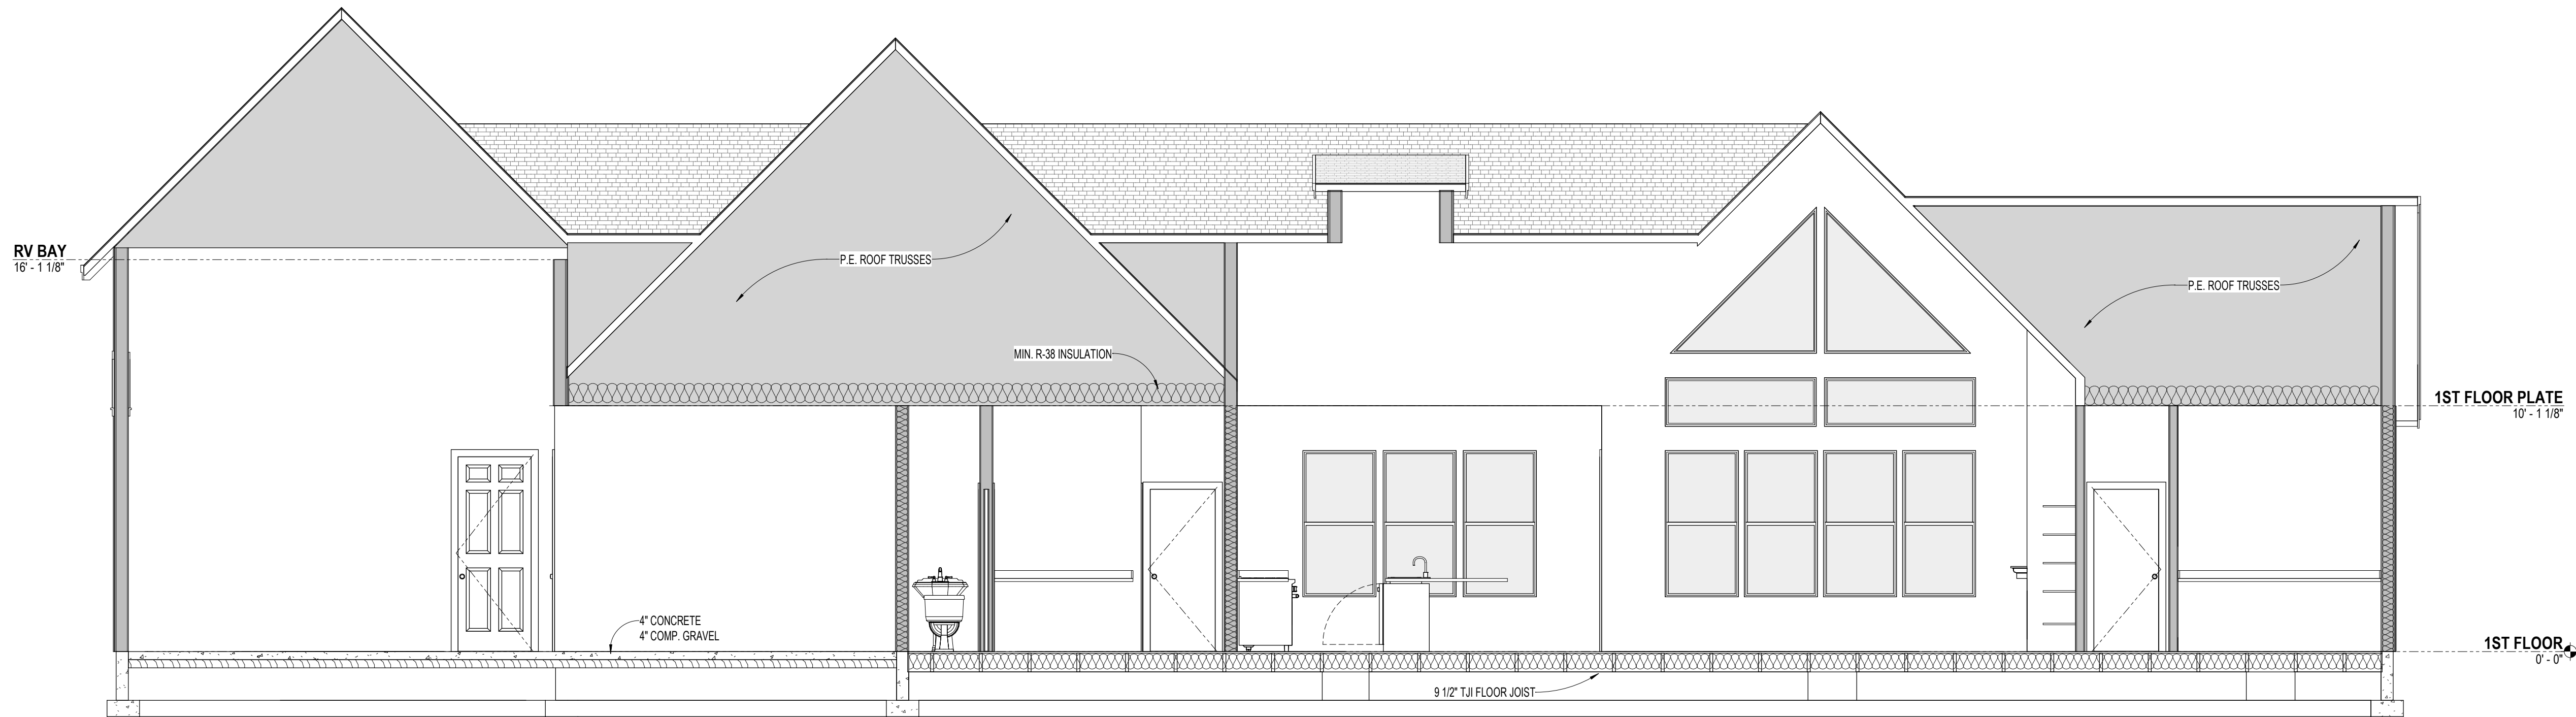

2 BUILDING SECTION-2
1/4" = 1'-0"

NOTE: RISEN HOME DESIGN PLANS DO NOT CARRY AN ENGINEER'S AND/OR ARCHITECT'S STAMP(S) SOME CONDITIONS MAY ARISE DURING DESIGN, AND/OR CONSTRUCTION THAT MAY REQUIRE AN ARCHITECT'S AND/OR ENGINEER'S STAMP TO COMPLY WITH LOCAL BUILDING CODES. THE CONTRACTOR IS TO VERIFY THESE CONDITIONS AND SECURE REQUIRED STAMPS PRIOR TO CONSTRUCTION

GENERAL CONDITIONS
DRAWINGS & SPECIFICATIONS
IT IS THE INTENT OF THE DRAWINGS AND SPECIFICATIONS TO BE GUIDELINES FOR CONSTRUCTION. THE CONTRACTOR IS RESPONSIBLE FOR DETERMINING ANY QUESTIONS AND MEANINGS IN THE WORKING DRAWINGS AND SPECIFICATIONS AND THE CONTRACTOR SHALL NOTIFY THE DESIGNER IN WRITING OF ANY ERRORS, OMISSIONS, OR UNSUITABLE DETAILING WHICH MAY CAUSE CONSTRUCTION PROBLEMS. THE DESIGNER'S LIABILITY REGARDING ERRORS AND/OR OMISSIONS WILL BE LIMITED TO THE CORRECTION OF THE ORIGINAL DRAWINGS. CONSULTANT'S LIABILITY IS THE SAME.



WHITESTONE
LOT#7 BLK#2 RIVERWALK CROSSING
MIDDLETON, ID
CUT SECTION VIEWS

BLACKSTONE
HOMES

These Drawings contain confidential proprietary information and are the property of Risen Home Design. These drawings are NOT to be reproduced, copied whole or in part, disclosed, used for construction or any other purpose without prior written permission from Risen Home Design.

REVISIONS	
NO.	DATE
0	7/10/2024
DESCRIPTION	
ISSUE FOR CONSTRUCTION	

SHEET TITLE
CUT SECTION
VIEWS

RHD PROJECT NUMBER: RHD-1169

DRAWN BY: RMC DATE: 7/10/2024

CHECKED BY: MM DATE: 7/10/2024

DRAWING NUMBER: A8.1 REV: 0